


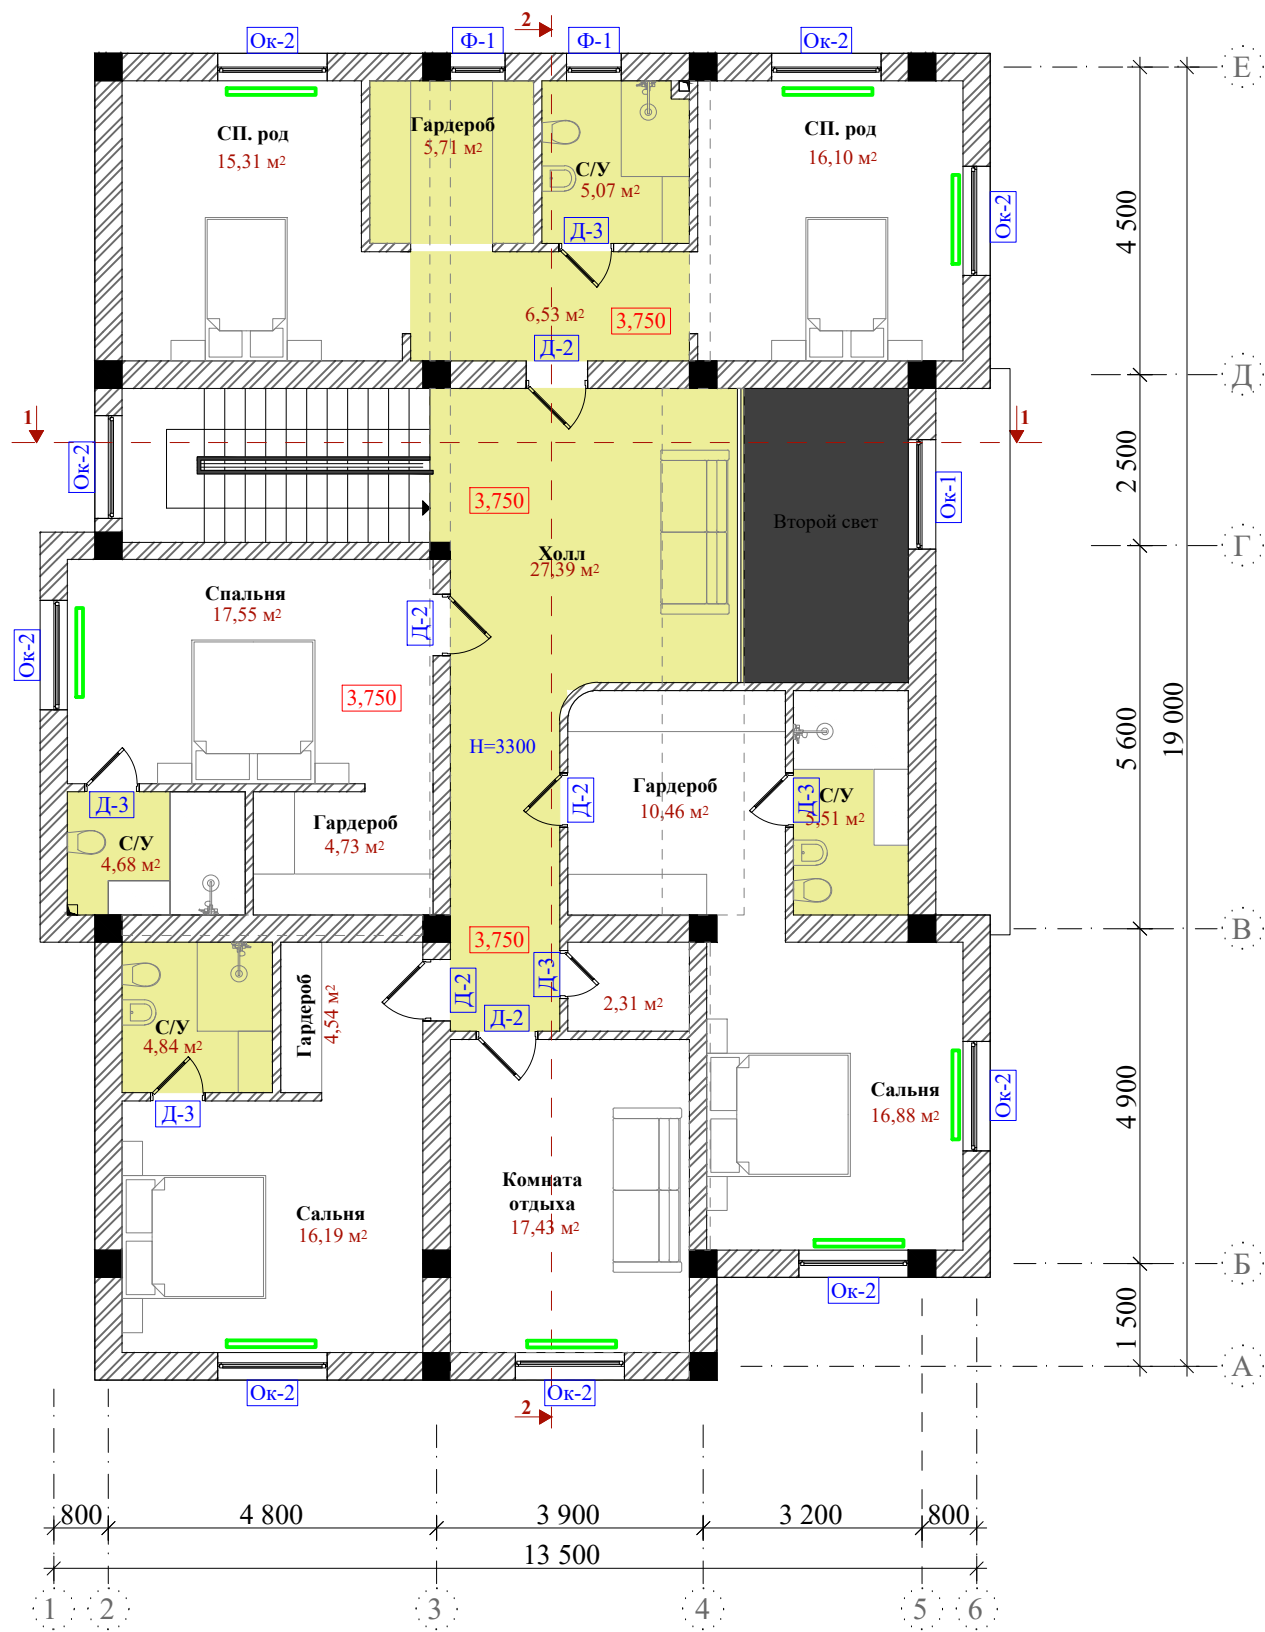

Условные обозначения

- Рadiator
- Водяной теплый пол

						АР			
Изм.	Кол.	Лист	№ док.	Подпись	Дата	Хонаи истиқоматӣ			
							Стадия	Лист	Листов
ГИП		Раҷабов С.					РП	20	26
ГАП		Раҷабов С.							
Разраб.		Холов С.				План 2-го этажа			