

Ведомость рабочих чертежей марки АР

Лист	Наименование	Примечание
АР-1	Общие данные	
АР-2	Экспликация полов, основные показатели	
АР-3	Спецификация дверных проемов	
АР-4	Ситуационная схема	
АР-5	Разбивка ген. плана	
АР-6	Общий вид	
АР-7	Общий вид	
АР-8	Общий вид	
АР-9	Общий вид	
АР-10	Общий вид	
АР-11	Общий вид	
АР-12	Фасад в осях 1-6	
АР-13	Фасад в осях 6-1	
АР-14	Фасад в осях А-Е	
АР-15	Фасад в осях Е-А	
АР-16	План подвального этажа на отметке -2,950	
АР-17	Разбивочный план подвального этажа на отметке -2,950	
АР-18	План 1-го этажа на отметке 0,000	
АР-19	Разбивочный план 1-го этажа на отметке 0,000	
АР-20	План 2-го этажа на отметке +3,750	
АР-21	Разбивочный план 2-го этажа на отметке +3,750	
АР-22	План кровли	
АР-23	Разбивочный план кровли	
АР-24	Разрез 1-1	
АР-25	Разрез 2-2	
АР-26	Фрагменты фасадов	

Пояснительная записка

Проектируемое здание "Индивидуальный жилой дом"
Проектируемое здание состоит из 2-х этажей с подвальным этажом с размерами в осях 13,500 x 19,000м.
Высота этажей принято:
-высота подвала- 2,950 м;
-высота 1-го этажа - 3,750 м;
-высота 2-го этажа - 3,250 м;
Кровля - многоскатная из металлочерепицы.

Исходные данные

1. Климатический подрайонIVГ
2. Расчётная температура наружного воздуха-15 °С
3. Нормативное значение ветрового давления52 кгс/м2
4. Нормативное значение веса снегового покрова84 кг/м2
5. Сейсмичность участка строительства8 баллов
6. Степень огнестойкостиII

						АР			
Изм.	Кол.	Лист	№ док.	Подпись	Дата	Хонаи истиқоматӣ			
							Стадия	Лист	Листов
ГИП		Рачабов С.					РП	1	26
ГАП		Рачабов С.							
Разраб.		Холов С.				Общие данные			





Основные объемно - планировочные показатели

№ п/п	Наименования показателей	Единица измерения	Количество
1	Этажность	этаж	2
2	Высота этажей	М	3,75 и 3,25
3	Полезная площадь	М²	289,92
4	Площадь застройки	М²	250,65
5	Строительный объем , в том числе подземной части	М³	2243,31 368,75
6	Общая площадь	М²	424,17

Технические характеристики строительных конструкций

№ п/п	Наименование конструкции и виды работ	Характеристика конструкций и виды работ
1	Фундаменты	Мон. ж/б ленточного типа
2 3	Стены наружные	Жженный кирпич
	Перегородки	Жженный кирпич
4	Каркас	Мон. ж/б колонны
5	Перекрытие	Мон. ж/б
6	Кровля	Многоскатная из металлочерепицы
7	Окна	Тёплый алюминий
8	Двери	Металлопластиковые, деревянные
9	Полы	Деревянный , керамогранит, керамич. плитка , бетонные-160-180мм
10	Внутренняя отделка	Стены и перегородки-улучшенная штукатурка, шпатлевка, окраска ВА В гардеробно-душ. блоках - улучшенная штукатурка, глазурованная плитка
11	Наружняя отделка	Цоколь - облицовочная цокольная плитка Стены - вентилируемый фасад из камня травертино ,цвет по проекту.



Экспликация полов

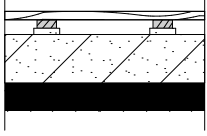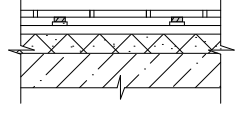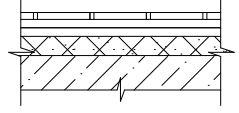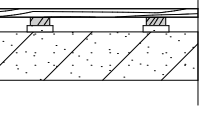Наименов. помещений или номер по проекту	Тип пола	Схема пола или номер узла по серии	Элементы пола и их толщина, мм	Площадь, м²
1	2	3	4	5
Холл			1. "Керамогранит" шероховатой поверхности δ= 10мм; (a=600, b=600) 2. Клей на цементной основе δ=10мм; 3. Цементно-песч.р-р. М-150 δ=30мм; 4. Ж/Б плита перекрытия	
Летняя кухня			1. "Керамогранит" шероховатой поверхности δ= 10мм; (a=600, b=600) 2. Клей на цементной основе δ=10мм; 3. Теплоизоляция Технониколь δ=100мм 4. Цементно-песч.р-р. М-150 δ=30мм; 5. Ж/Б плита перекрытия	
Комната отдыха Спальная Гардеробная			1. Ламинат, δ=10; 2. Подложка под ламинат, δ=3мм 3. Стяжка из цементно-песчанного раствора, М 150, δ = 30мм; 4. Звукоизоляционный слой из полистеролбетона, δ = 40мм; D=400кг/м³; 5. Ж/Б плита перекрытия.	
Сан.узлы Душевая			1. "Керамогранит" шероховатой поверхности δ= 8мм; (a=150, b=150) 2. Клей на цементной основе δ=10мм; 3. Цементно-песч.р-р. М-150 δ=30мм; 4. Ж/Б плита перекрытия.	

						АР			
Изм.	Кол.	Лист	№ док.	Подпись	Дата	Хонаи истиқоматӣ			
							Стадия	Лист	Листов
ГИП		Рачабов С.					РП	2	26
ГАП		Рачабов С.							
						Экспликация полов			
Разраб.		Холов С.							

Спецификация заполнения дверных и оконных проемов


№ поз.	Наименование	Размер проема (мм×мм)	Количество					
			-1 этаж	1 этаж	2 этаж	Всего		
Двери								
1	Д-1	900х2200	3	2	5	10	Металло-пластик	
2	Д-2	900х2400		3		3	Деревянный	
3	Д-3	800х2400		1		1		
4	Д-4	1800х2800		1		1		
5	Д-5	1900х900	2			2		
5	Д-6	1900х900		2	5	7		
6	До-1	4400х3250		1		1	Металлопластик (тёплый алюминий)	
7	До-2	1300х2400		1		1		
8	До-3	2250х2400		1		1		
9	До-4	900х2800		1		1		
Окна								
1	Ок-1	1600х2200		7	2	9	Металлопластик (тёплый алюминий)	
2	Ок-2	1600х2200			8	8		
3	Ок-3	1600х2800		2		2		
4	Ок-4	1600х2200			2	2		
5	Ок-5	2250х2200			1	1		
Фрамуги								
1	Фр-1	600х800		2	3	5	Металлопластик (тёплый алюминий)	

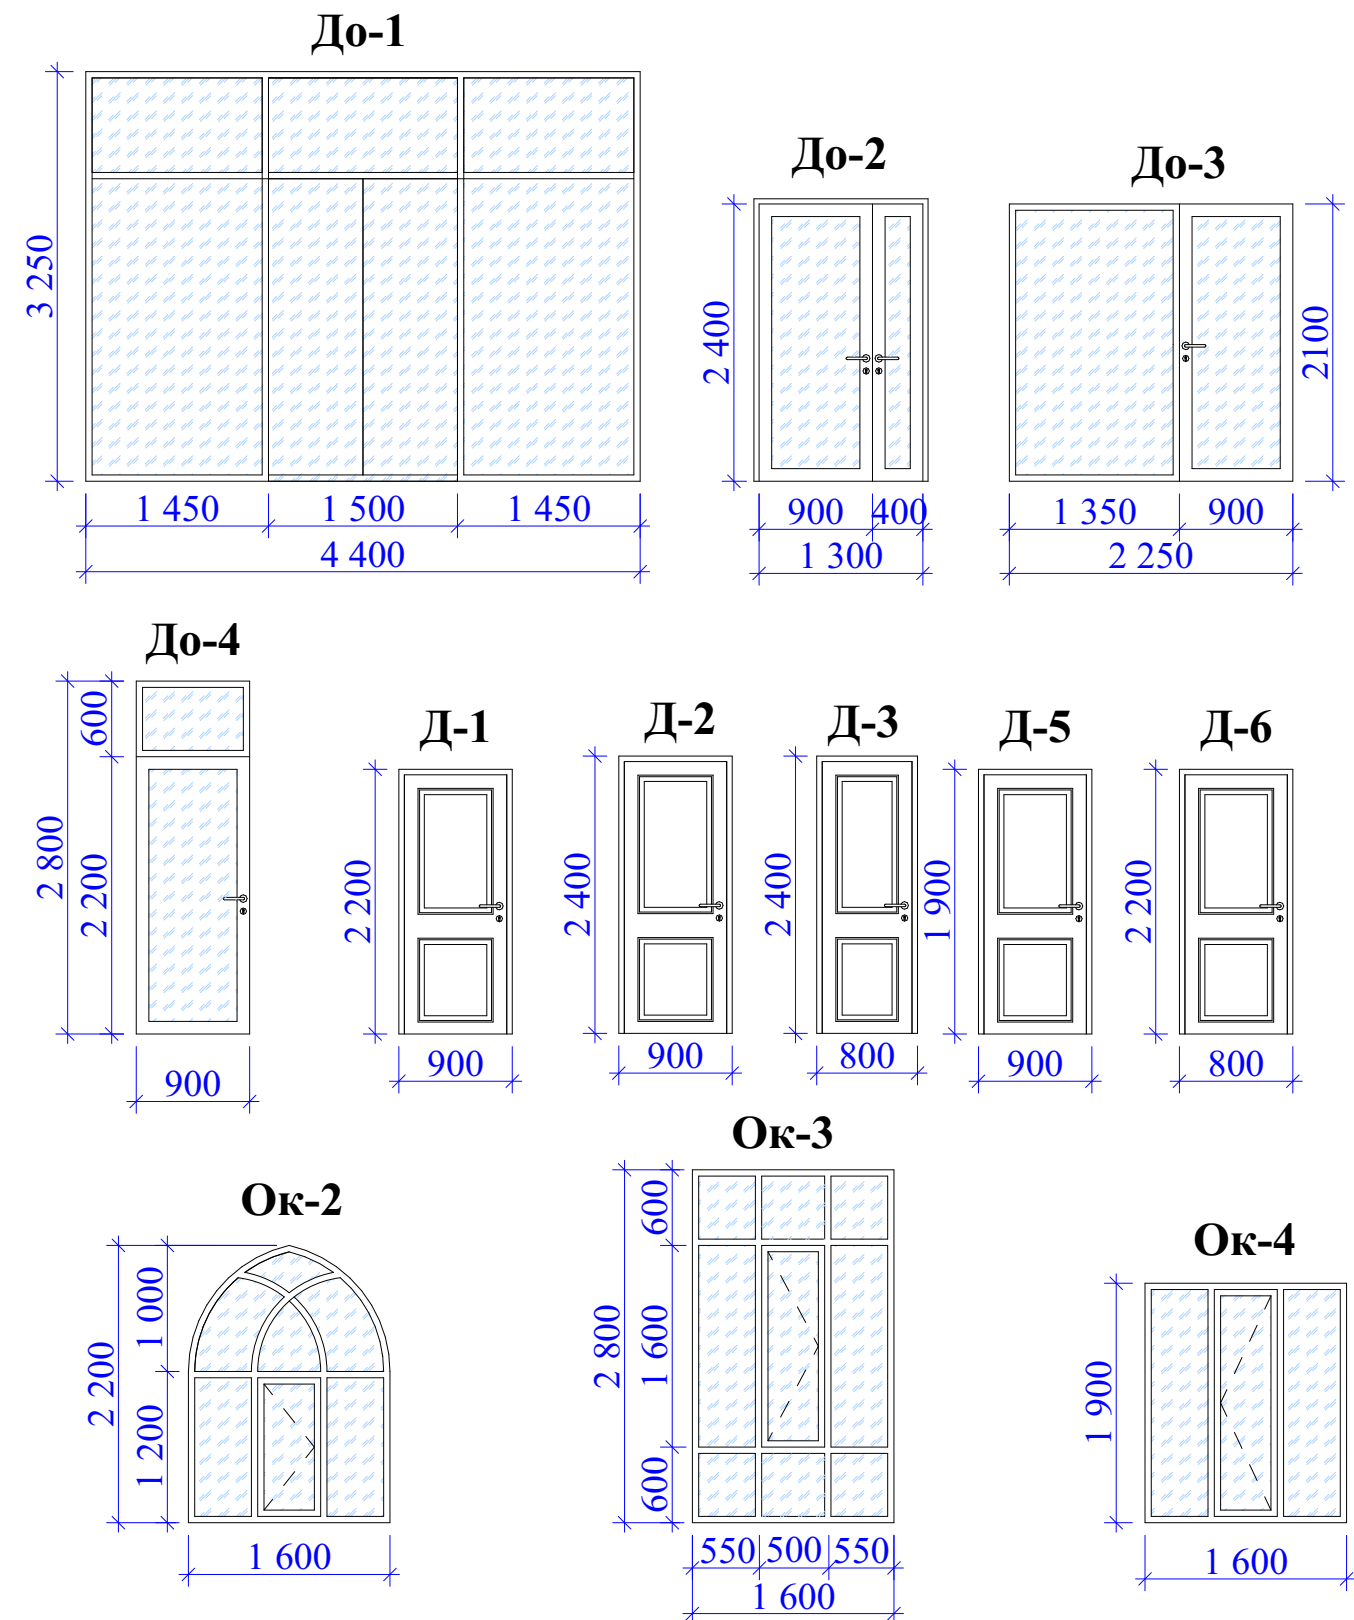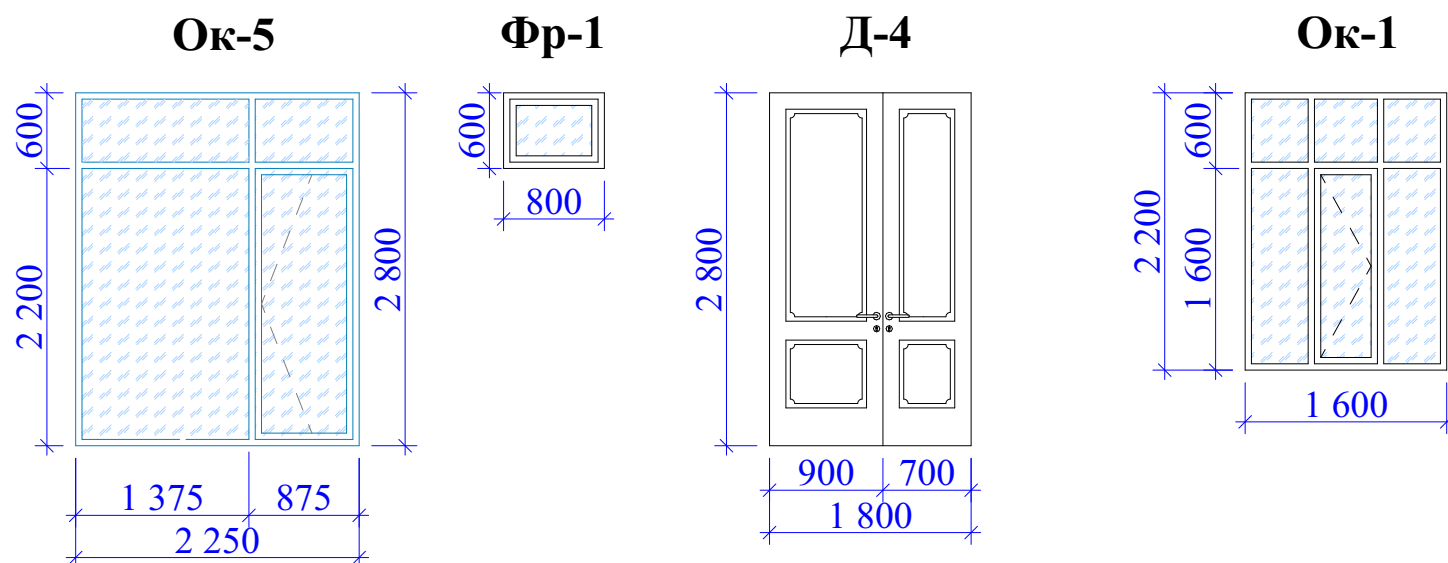

						АР			
Изм.	Кол.	Лист	№ док.	Подпись	Дата	Хонаи истиқоматӣ			
							Стадия	Лист	Листов
ГИП		Раҷабов С.					РП	3	26
ГАП		Раҷабов С.							
						Спецификация заполнения дверных и оконных проемов			
Разраб.		Холов С.							



НАҚШАИ ГЕНЕРАЛӢ

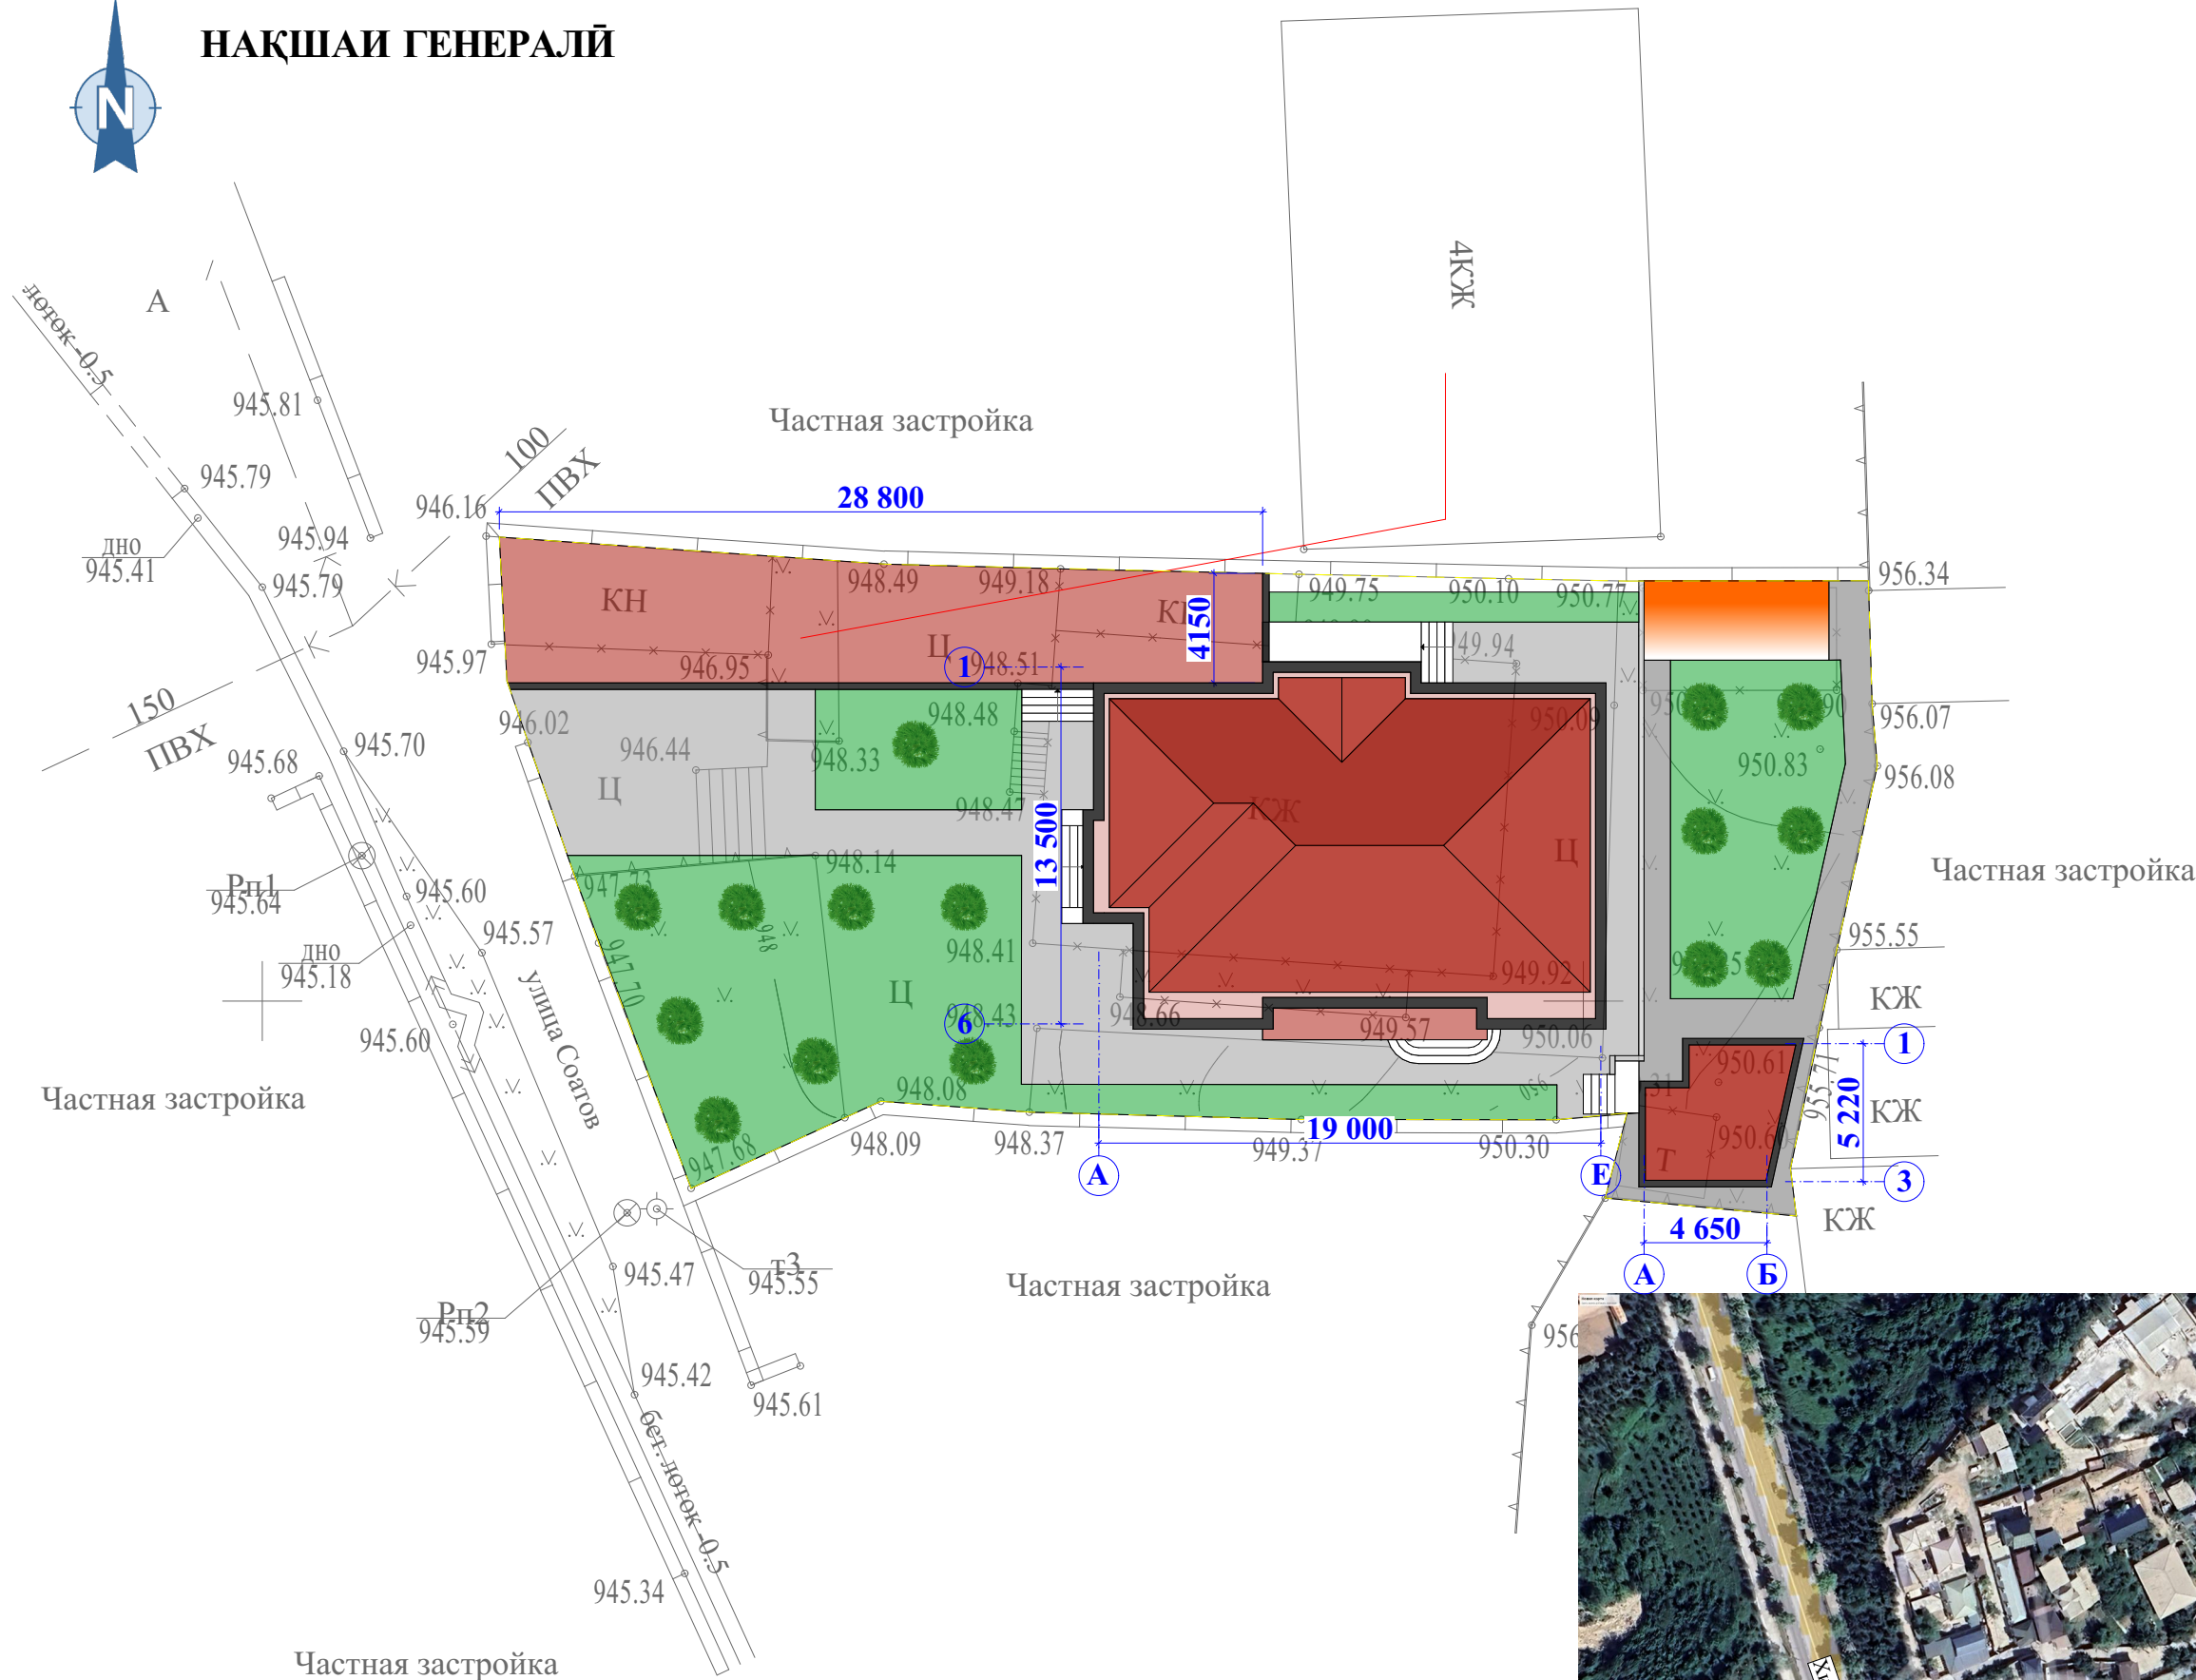

АЛОМАТҲОИ ШАРТӢ

- САРҲАДИ ҚИТЪАИ ЗАМИН
- БИНОИ ЛОИҲАВӢ (асосӢ)
- САБЗАЗОРКУНӢ
- БИНОИ ЁРИРАСОН
- САНГҲОИ ОРОИШӢ
- ДАРАХТҲОИ ОРОИШӢ
- ГАРМХОНА

НАҚШАИ ЧОӢГИРШАВӢ АЗ МОҲВОРА



















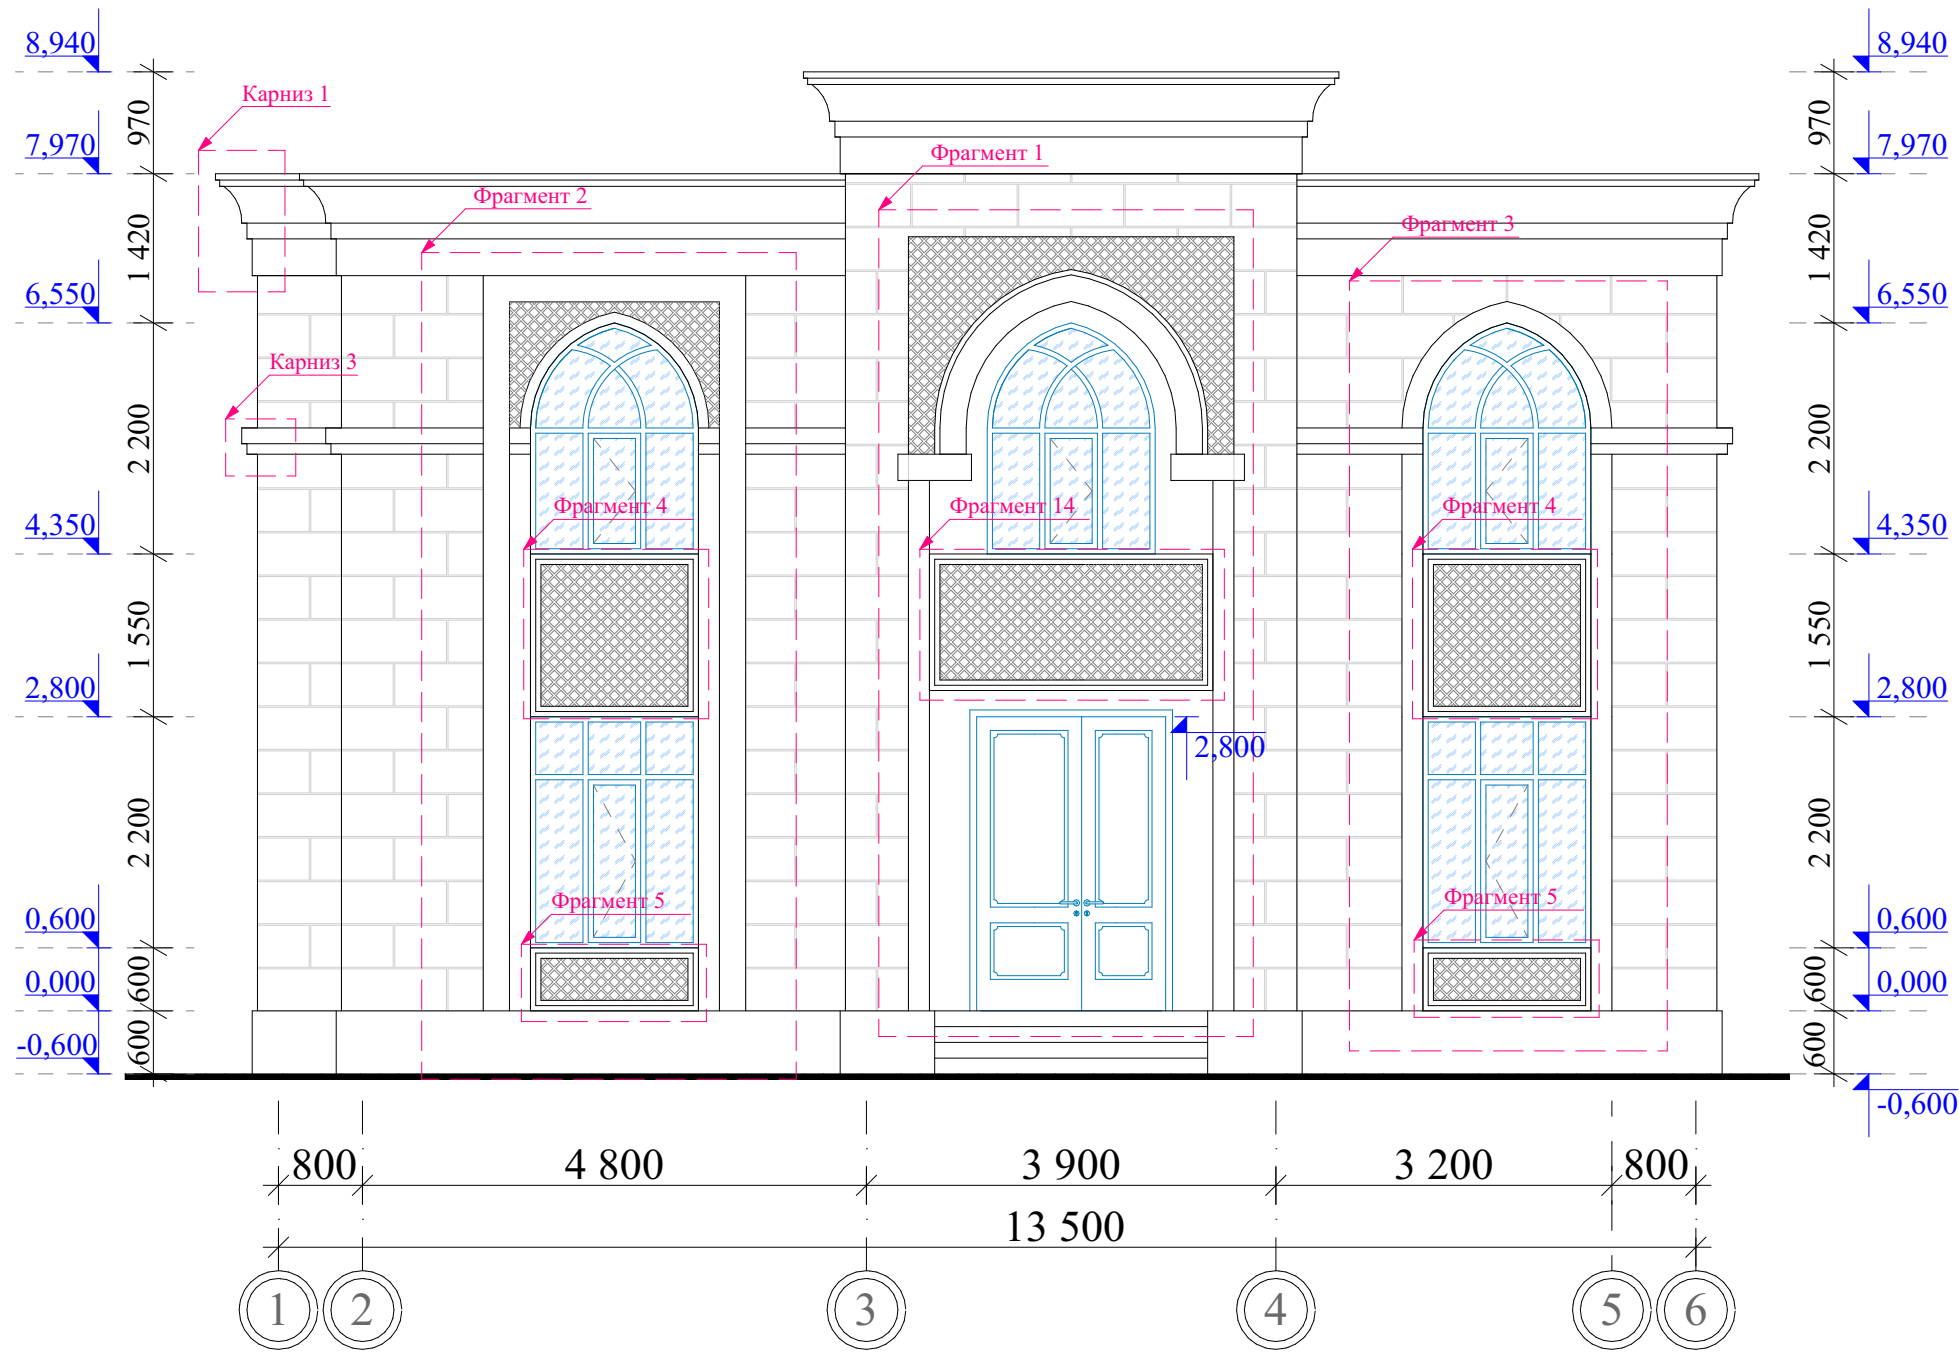


						АР			
Изм.	Кол.	Лист	№ док.	Подпись	Дата	Хонаи истиқоматӣ			
							Стадия	Лист	Листов
ГИП		Рачабов С.					РП	12	26
ГАП		Рачабов С.				Фасад в осях 1-6			
Разраб.		Холов С.							

Фасад в осях А-Е

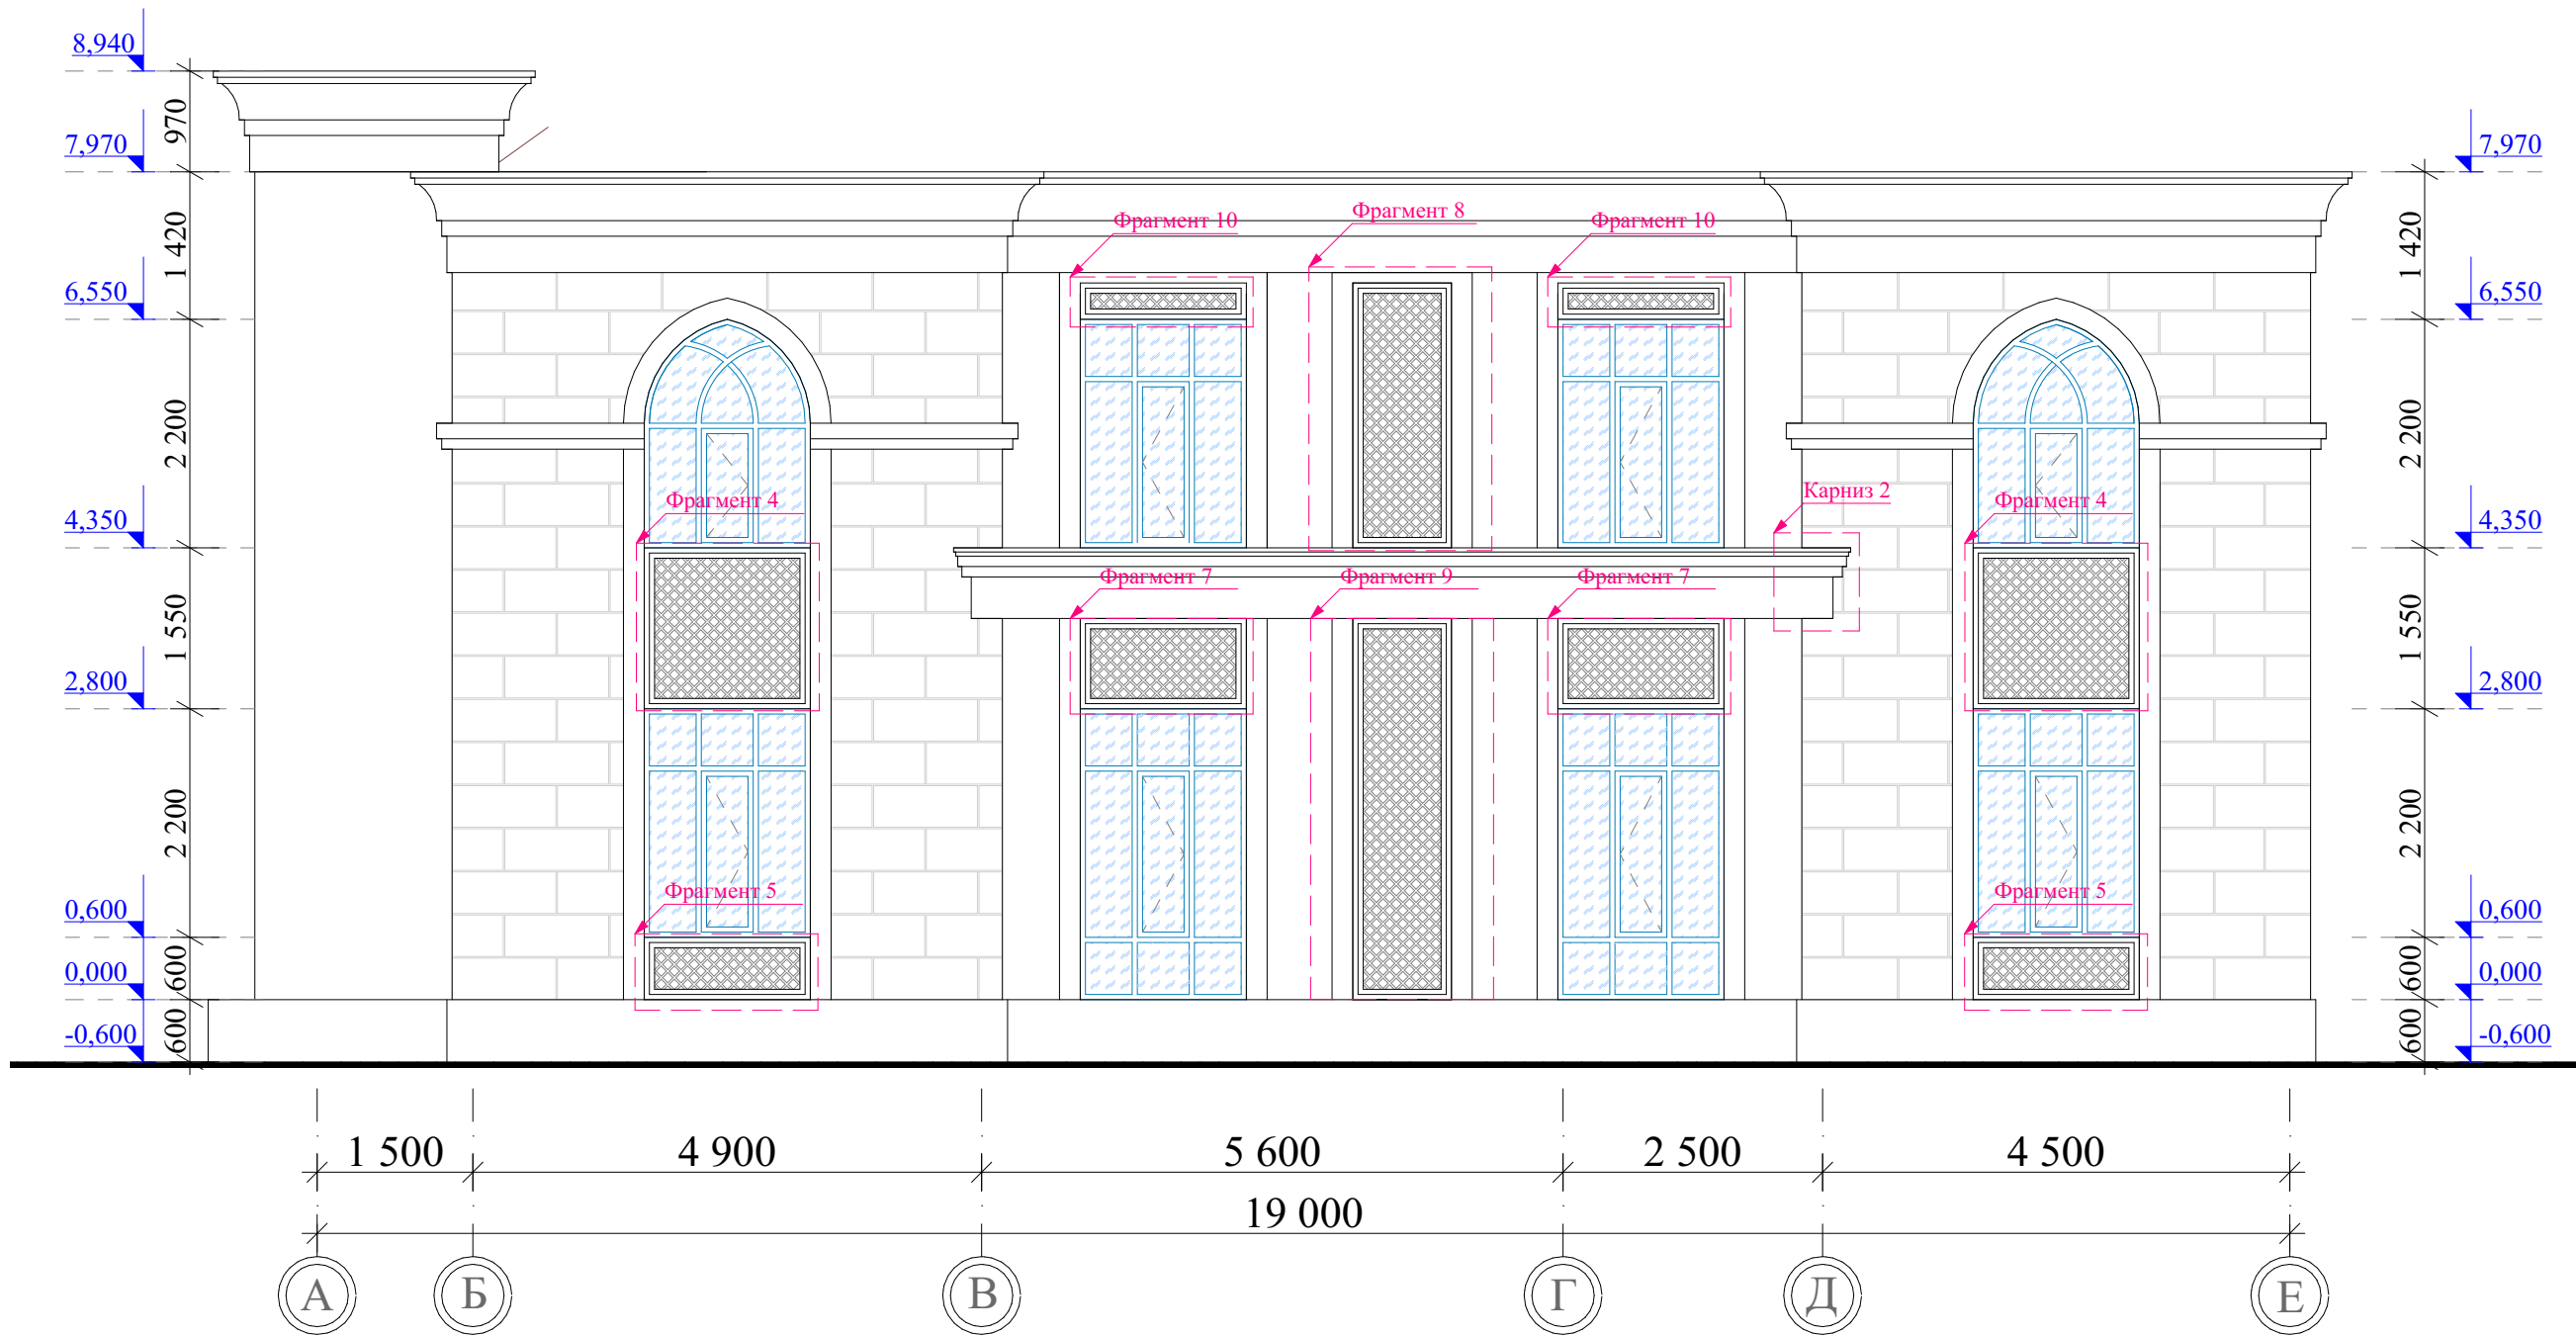

						АР			
Изм.	Кол.	Лист	№ док.	Подпись	Дата	Хонаи истиқоматӣ			
							Стадия	Лист	Листов
ГИП		Раҷабов С.					РП	14	26
ГАП		Раҷабов С.				Фасад в осях А-Е			
Разраб.		Холов С.							

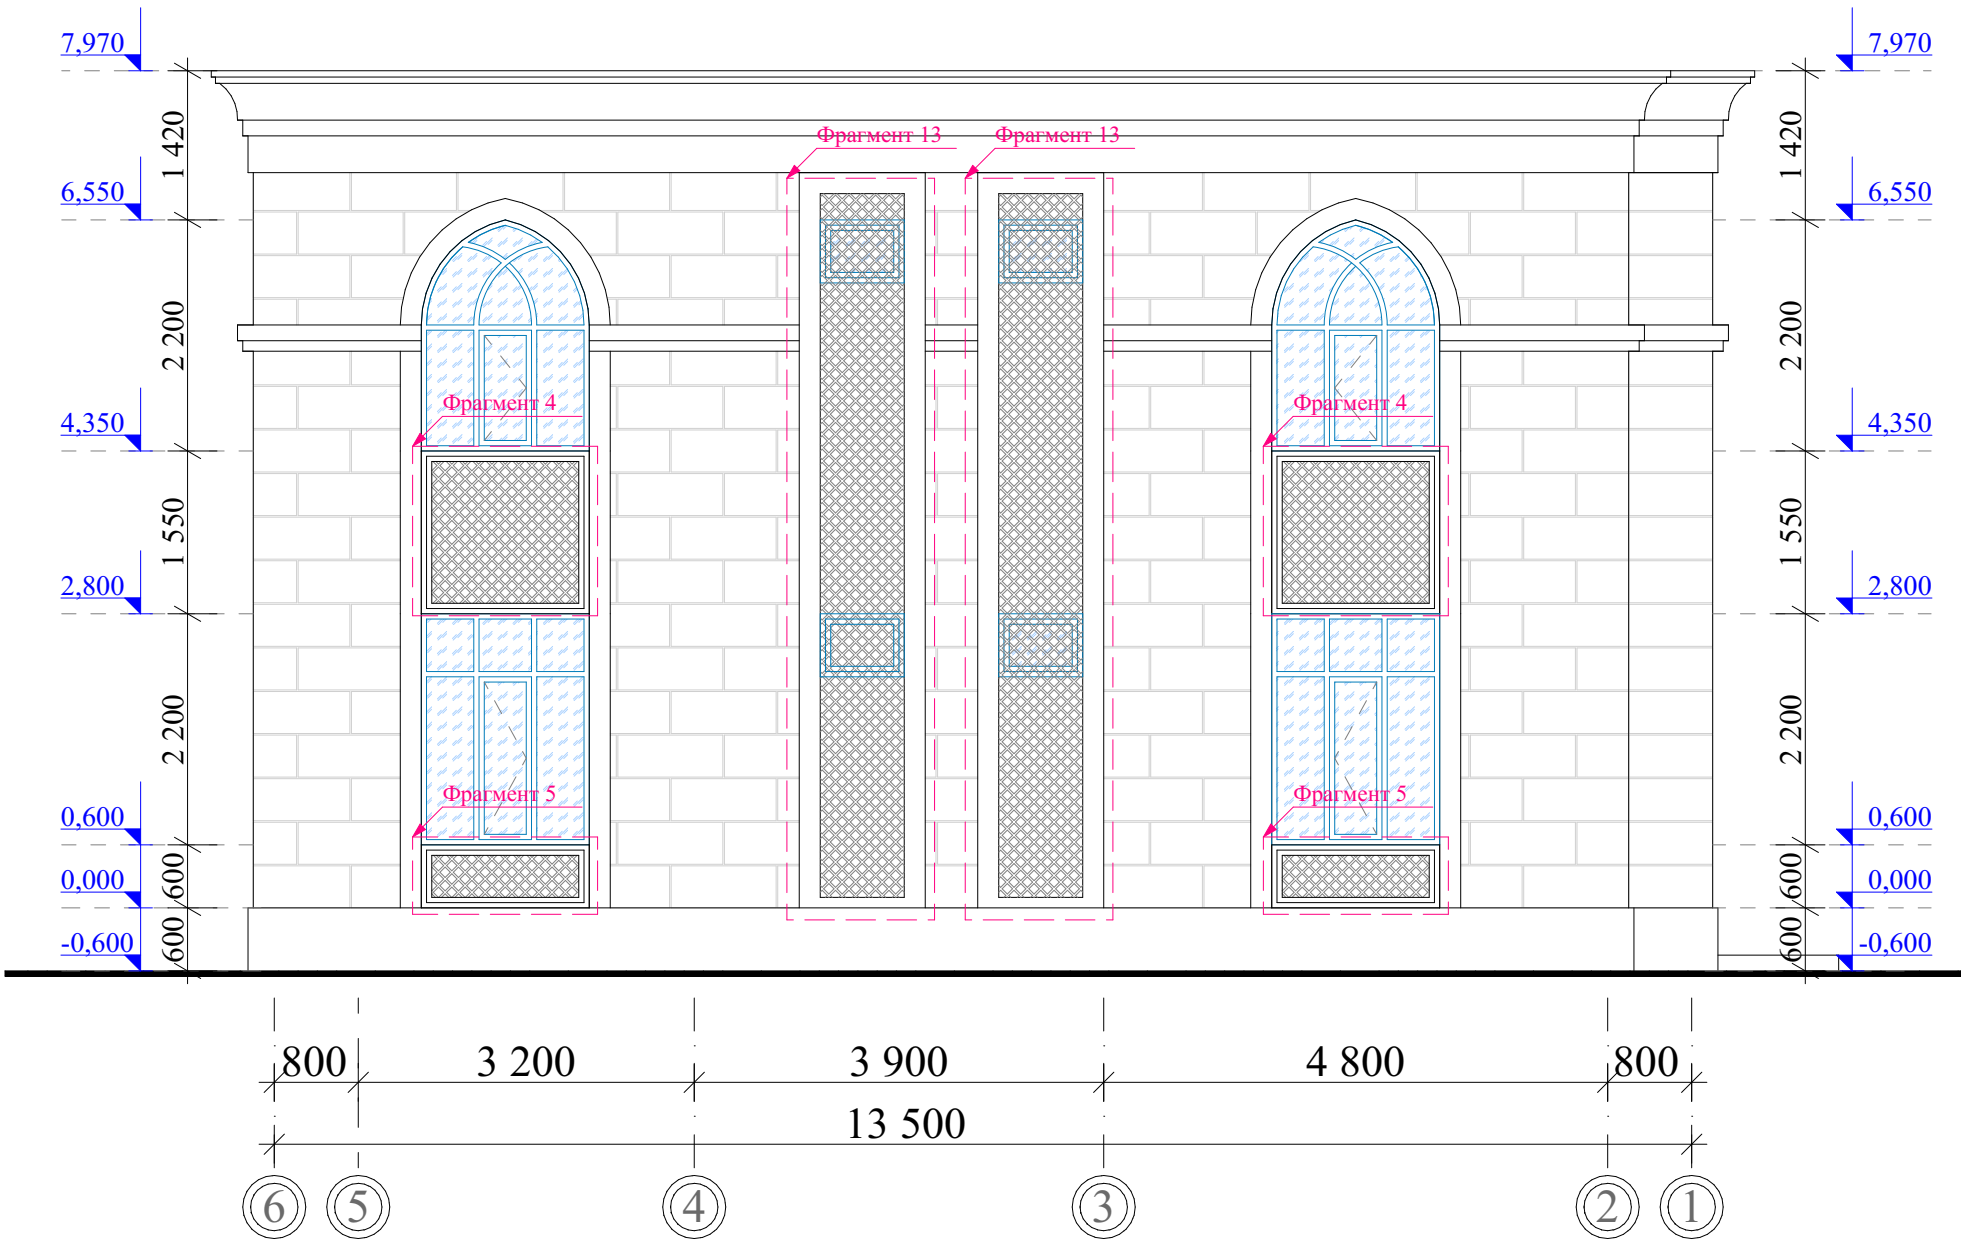


						АР			
Изм.	Кол.	Лист	№ док.	Подпись	Дата	Хонаи истиқоматӣ			
							Стадия	Лист	Листов
ГИП		Рачабов С.					РП	13	26
ГАП		Рачабов С.				Фасад в осях 6-1			
Разраб.		Холов С.							

Фасад в осях Е-А




						АР			
Изм.	Кол.	Лист	№ док.	Подпись	Дата	Хонаи истиқоматӣ			
							Стадия	Лист	Листов
ГИП		Рачабов С.					РП	15	26
ГАП		Рачабов С.				Фасад в осях Е-А			
Разраб.		Холов С.							

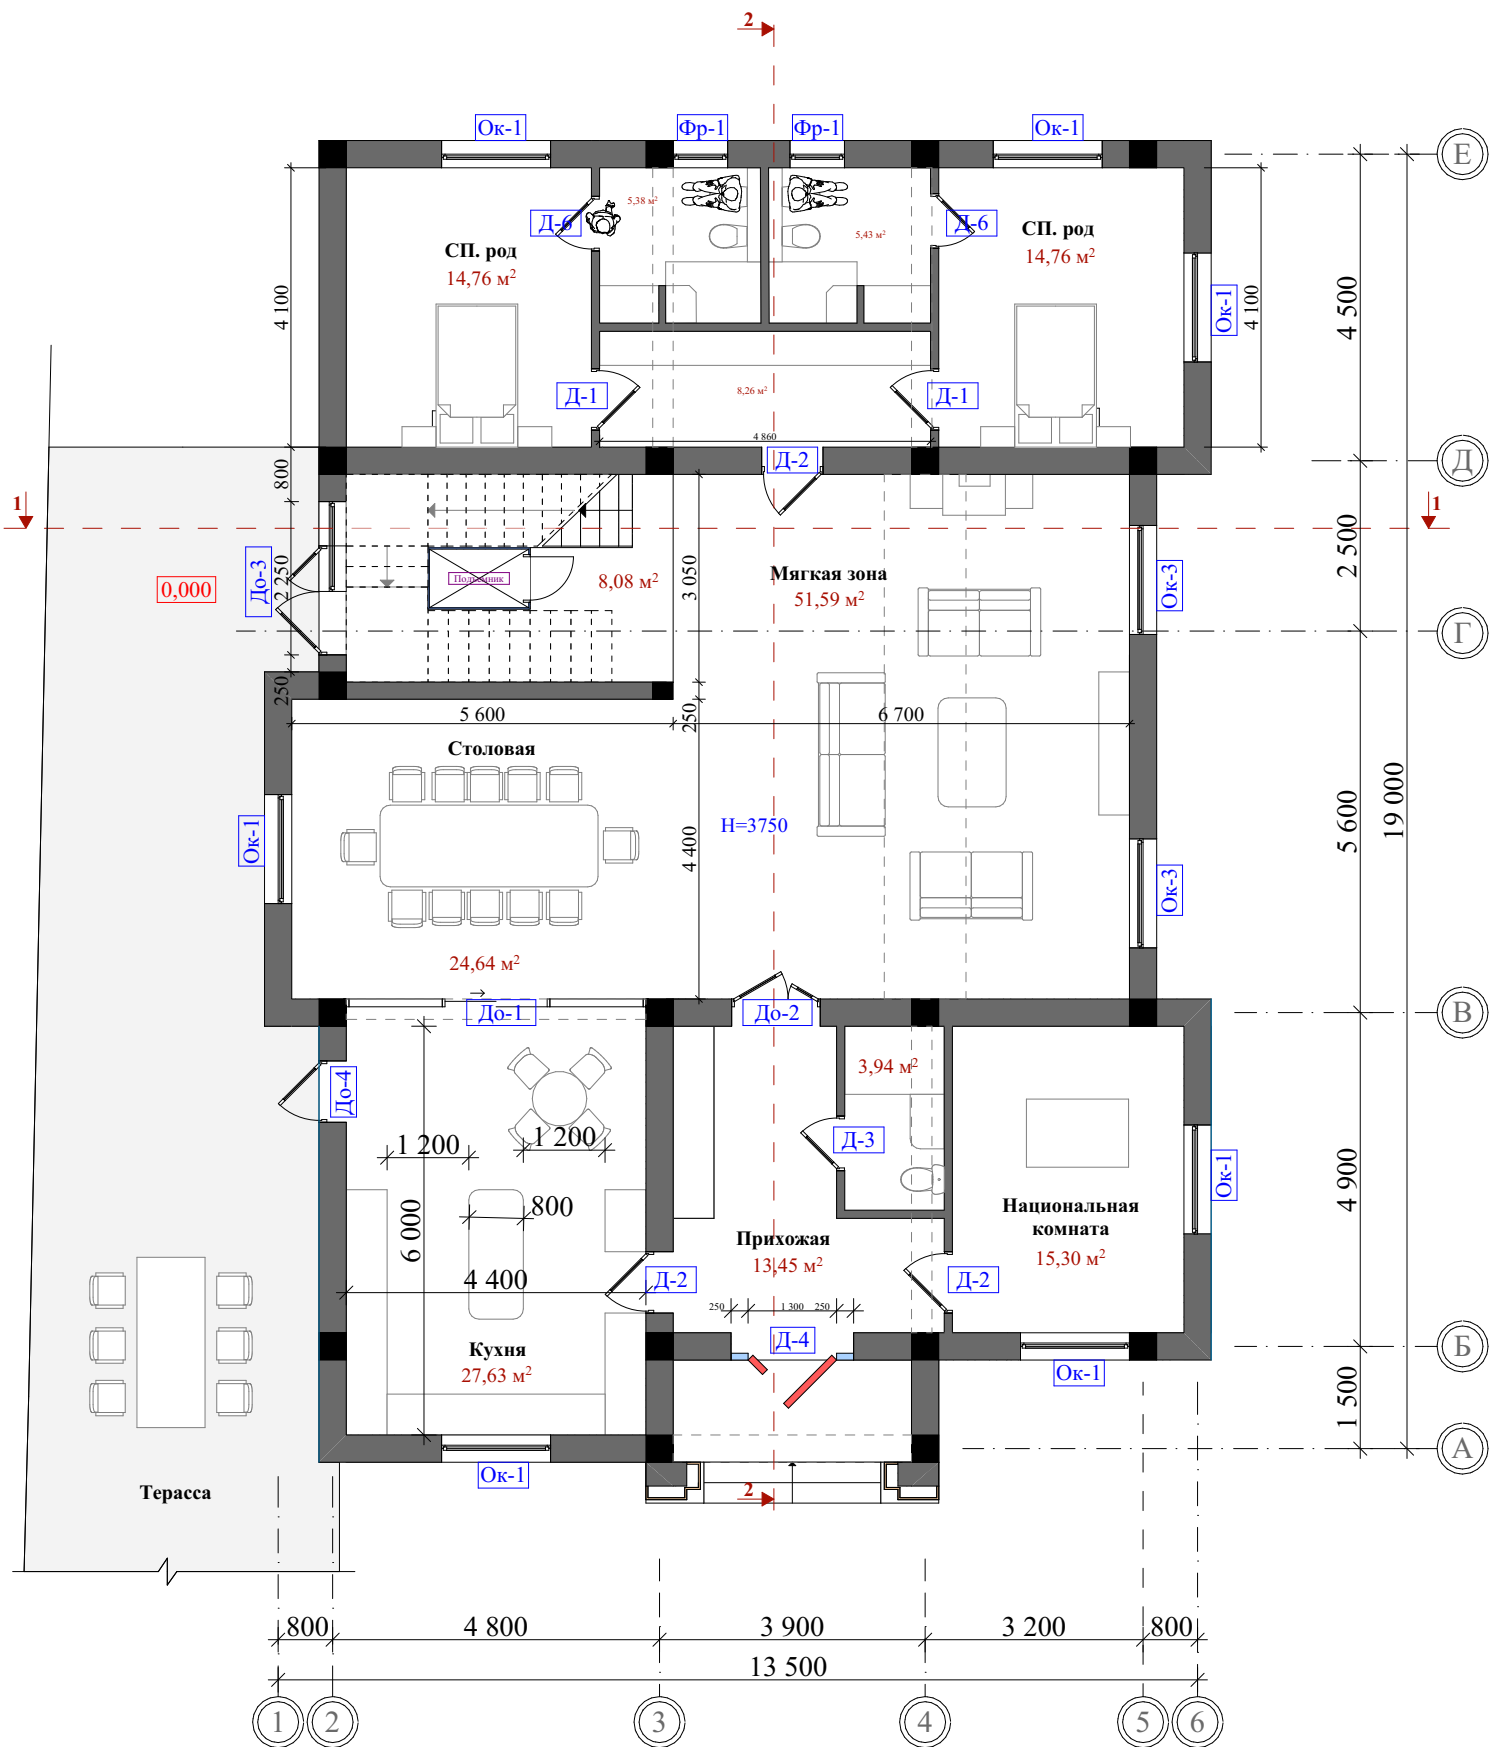


						АР			
Изм.	Кол.	Лист	№ док.	Подпись	Дата	Хонаи истиқоматӣ			
						План 1-го этажа на отм. +0,000	Стадия	Лист	Листов
ГИП		Рацабов С.					РП	18	26
ГАП		Рацабов С.							
Разраб.		Холов С.							

Разбивочный план 1-го этажа
на отм. 0,000

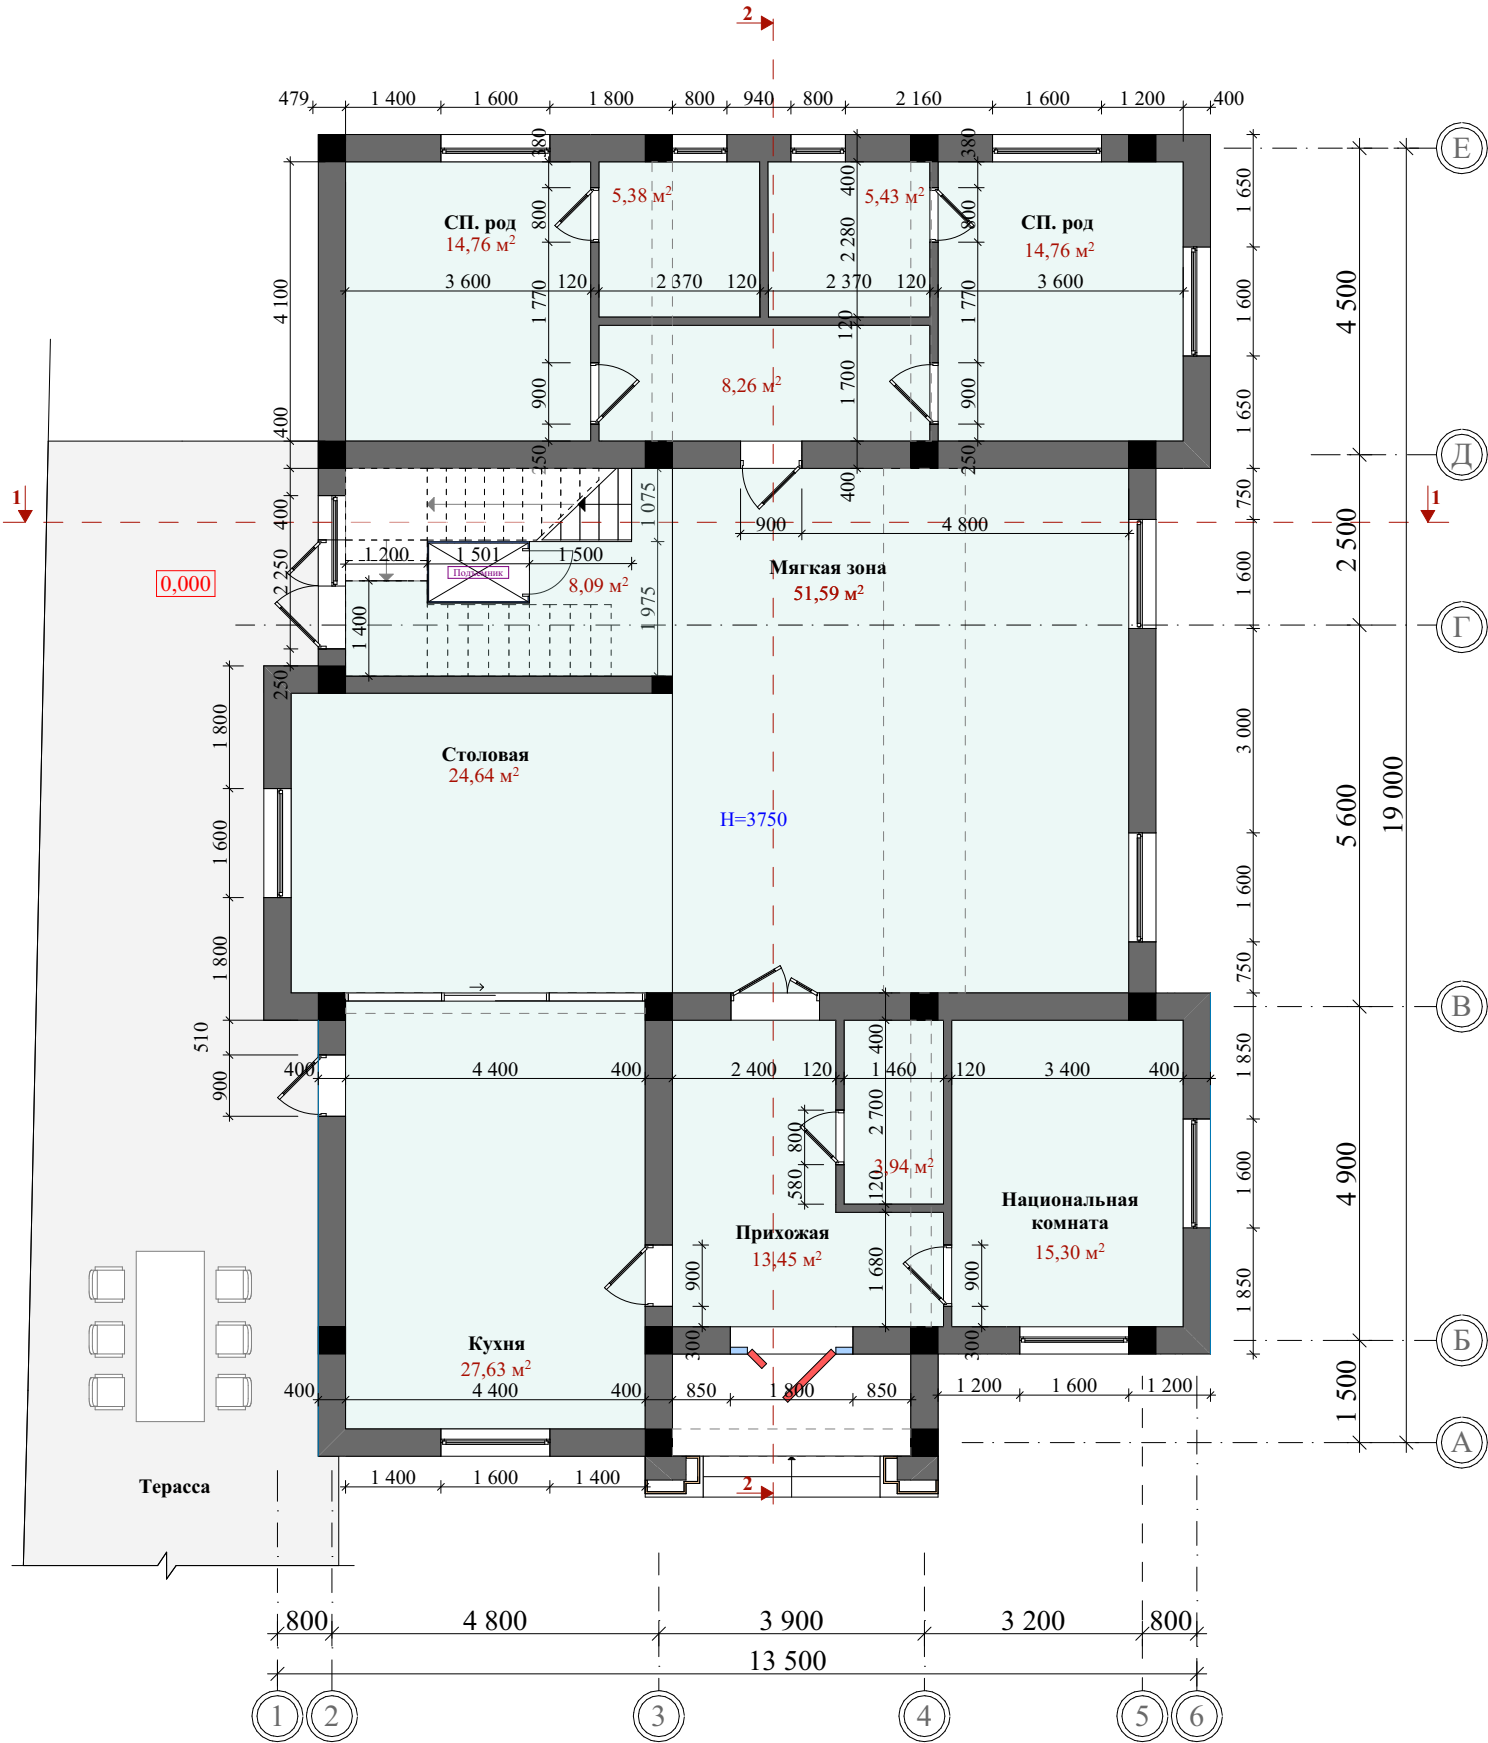


						АР			
Изм.	Кол.	Лист	№ док.	Подпись	Дата	Хонаи истиқоматӣ			
						Разбивочный план 1-го этажа	Стадия	Лист	Листов
ГИП		Рацабов С.					РП	19	26
ГАП		Рацабов С.							
Разраб.		Холов С.							

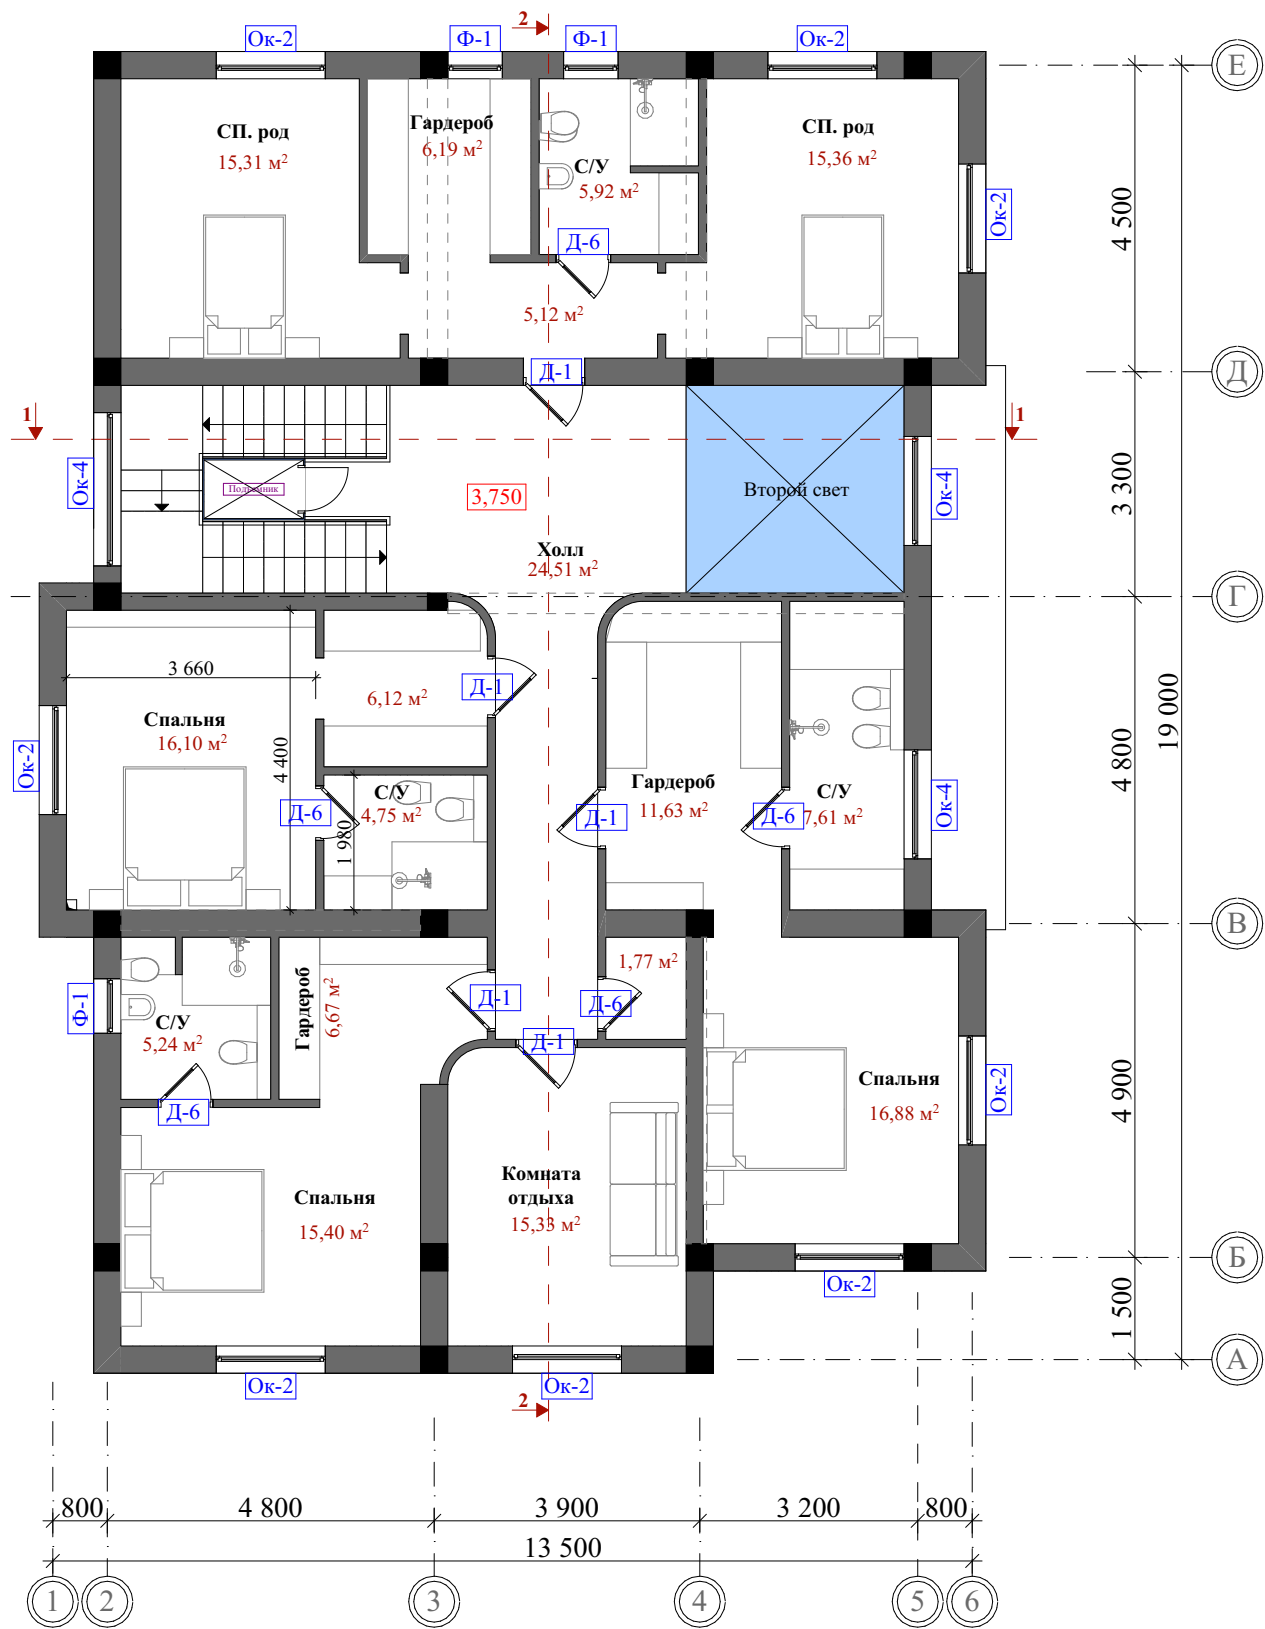


						АР			
Изм.	Кол.	Лист	№ док.	Подпись	Дата	Хонаи истиқоматӣ			
							Стадия	Лист	Листов
ГИП		Раҷабов С.					РП	20	26
ГАП		Раҷабов С.							
Разраб.		Холов С.				План 2-го этажа			

Разбивочный план 2-го этажа
на отм. +3,750

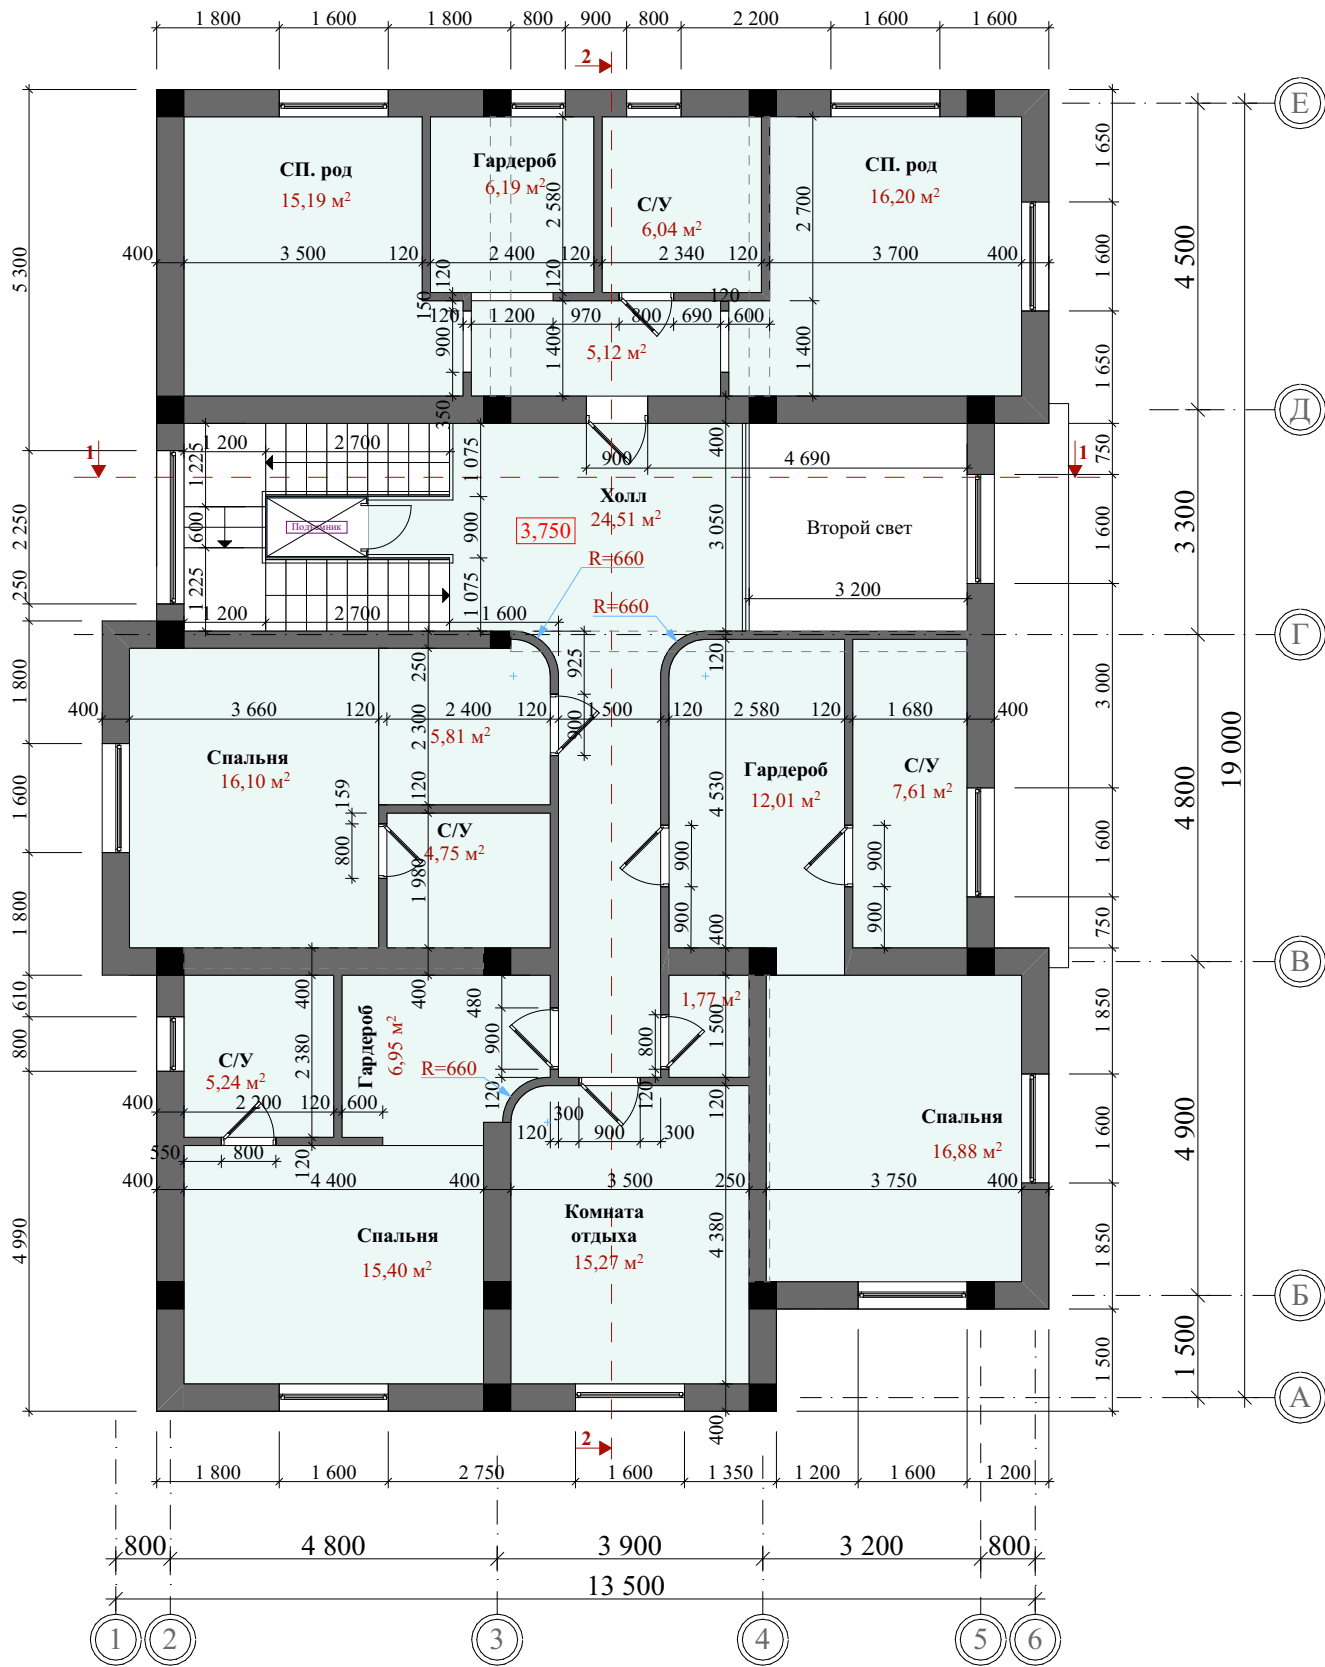

						АР			
Изм.	Кол.	Лист	№ док.	Подпись	Дата	Хонаи истиқоматӣ			
						Разбивочный план 2-го этажа	Стадия	Лист	Листов
ГИП		Рацабов С.					РП	21	26
ГАП		Рацабов С.							
Разраб.		Холов С.							

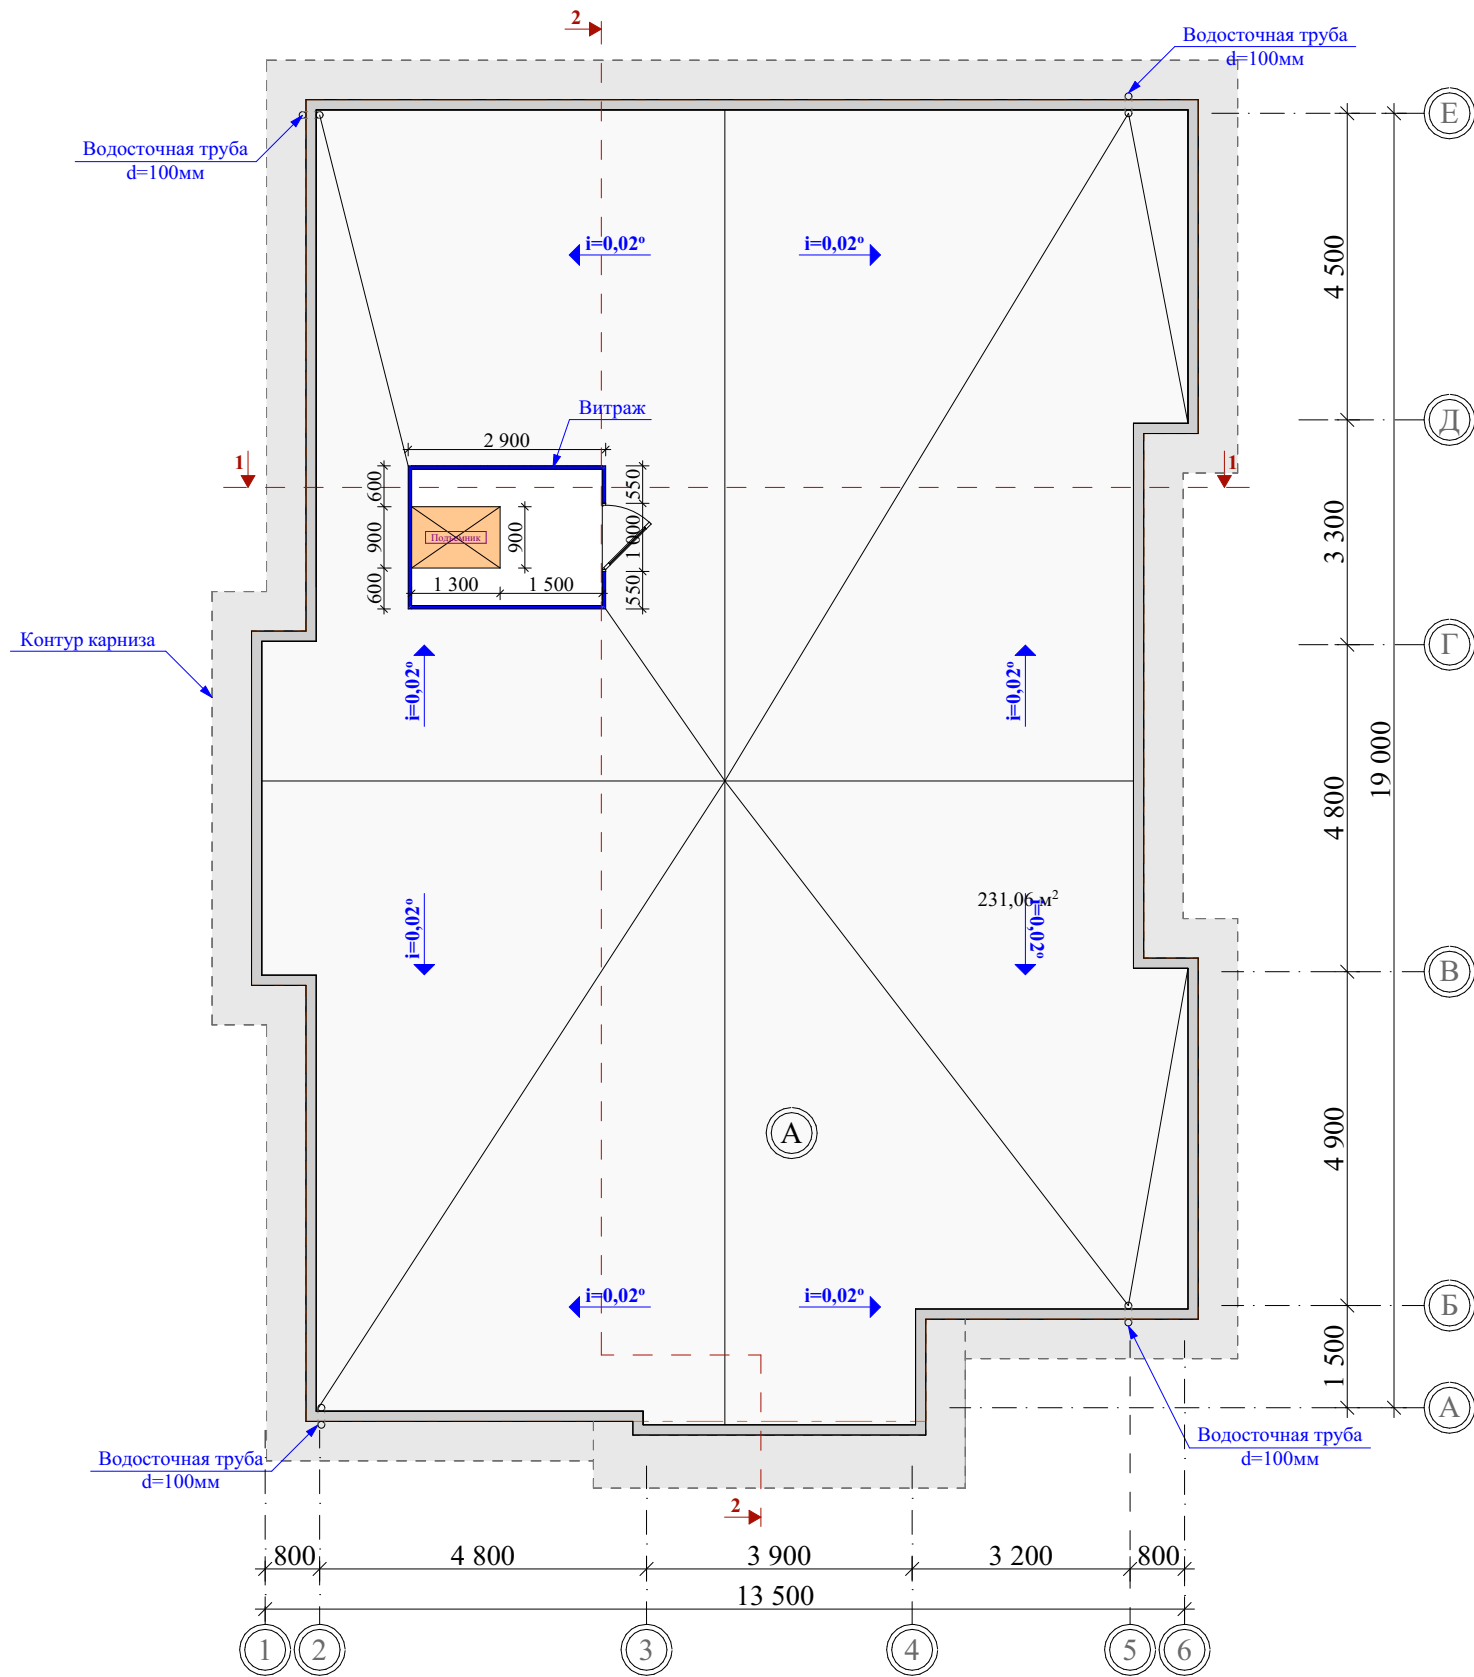


А

- 1-слой фальгоизол на битумной мастике
- 2-слоя рубероида на битумной мастике.
- Цементно-песчаная стяжка, $\delta=40$ мм.
- Керамзитовый гравий, $\rho=400$ кг/м³, $\delta=150\text{мм}-270\text{мм}$.
- Пароизоляция - обмазка горячим битумом.
- Монолитная ж/б плита перекрытия.

							АР			
Изм.	Кол.	Лист	№ док.	Подпись	Дата		Хонаи истиқоматӣ			
								Стадия	Лист	Листов
ГИП		Рацабов С.						РП	22	26
ГАП		Рацабов С.								
Разраб.		Холов С.					План кровли			

Разбивочный план кровли

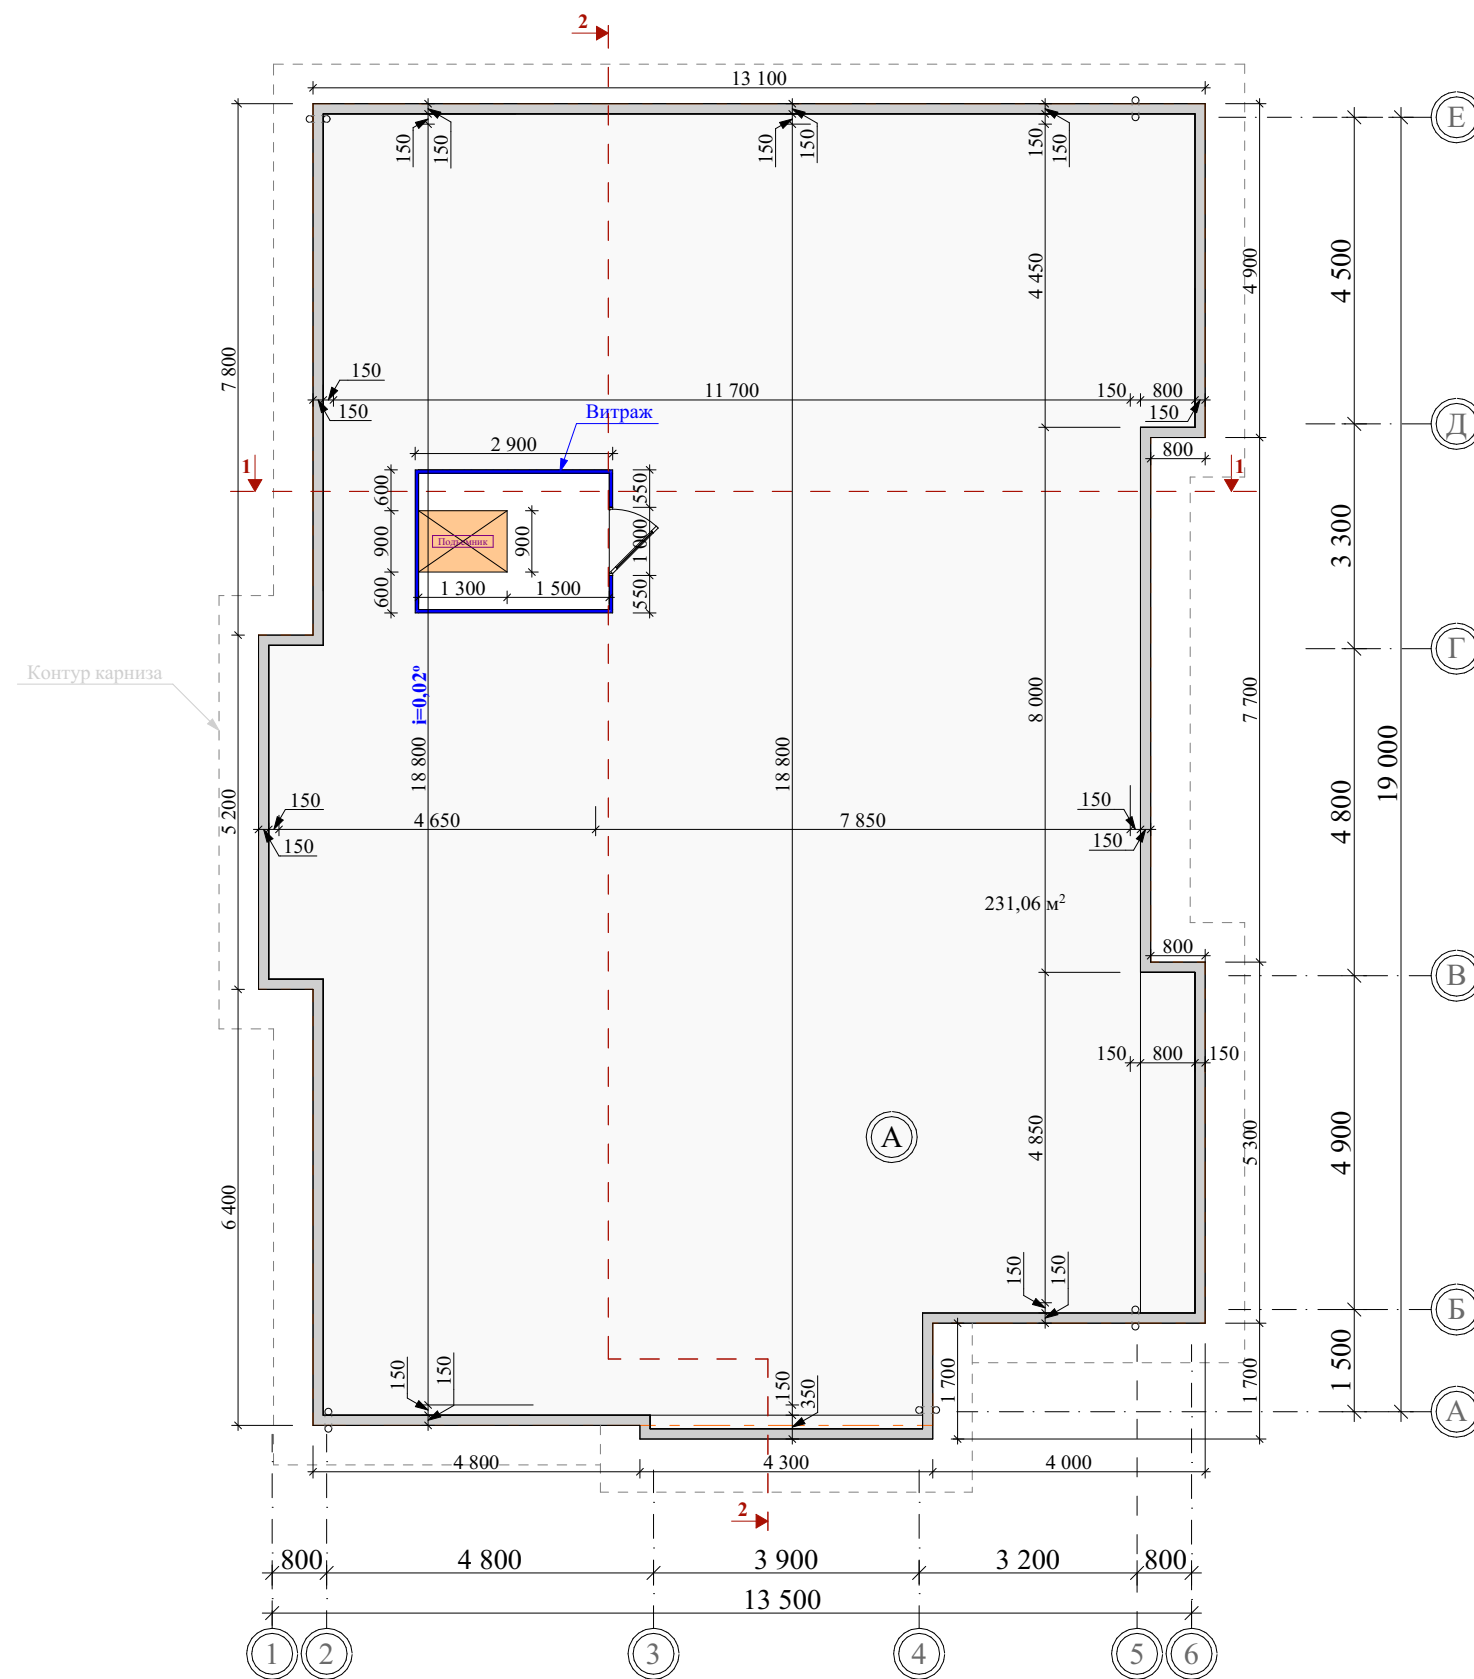


A


- | |
|---|
| 1. 1-слой фальгоизол на битумной мастике |
| 2. 2-слоя рубероида на битумной мастике. |
| 3. Цементно-песчаная стяжка, $\delta=40$ мм. |
| 4. Керамзитовый гравий, $\rho=400$ кг/м ³ , $\delta=150$ мм-270мм. |
| 5. Пароизоляция - обмазка горячим битумом. |
| 6. Монолитная ж/б плита перекрытия. |

						АР			
Изм.	Кол.	Лист	№ док.	Подпись	Дата	Хонаи истиқоматӣ			
						Стадия	Лист	Листов	
ГИП		Раҷабов С.				РП	23	26	
ГАП		Раҷабов С.							
						Разбивочный план кровли			
Разраб.		Холов С.							





Разрез 2-2

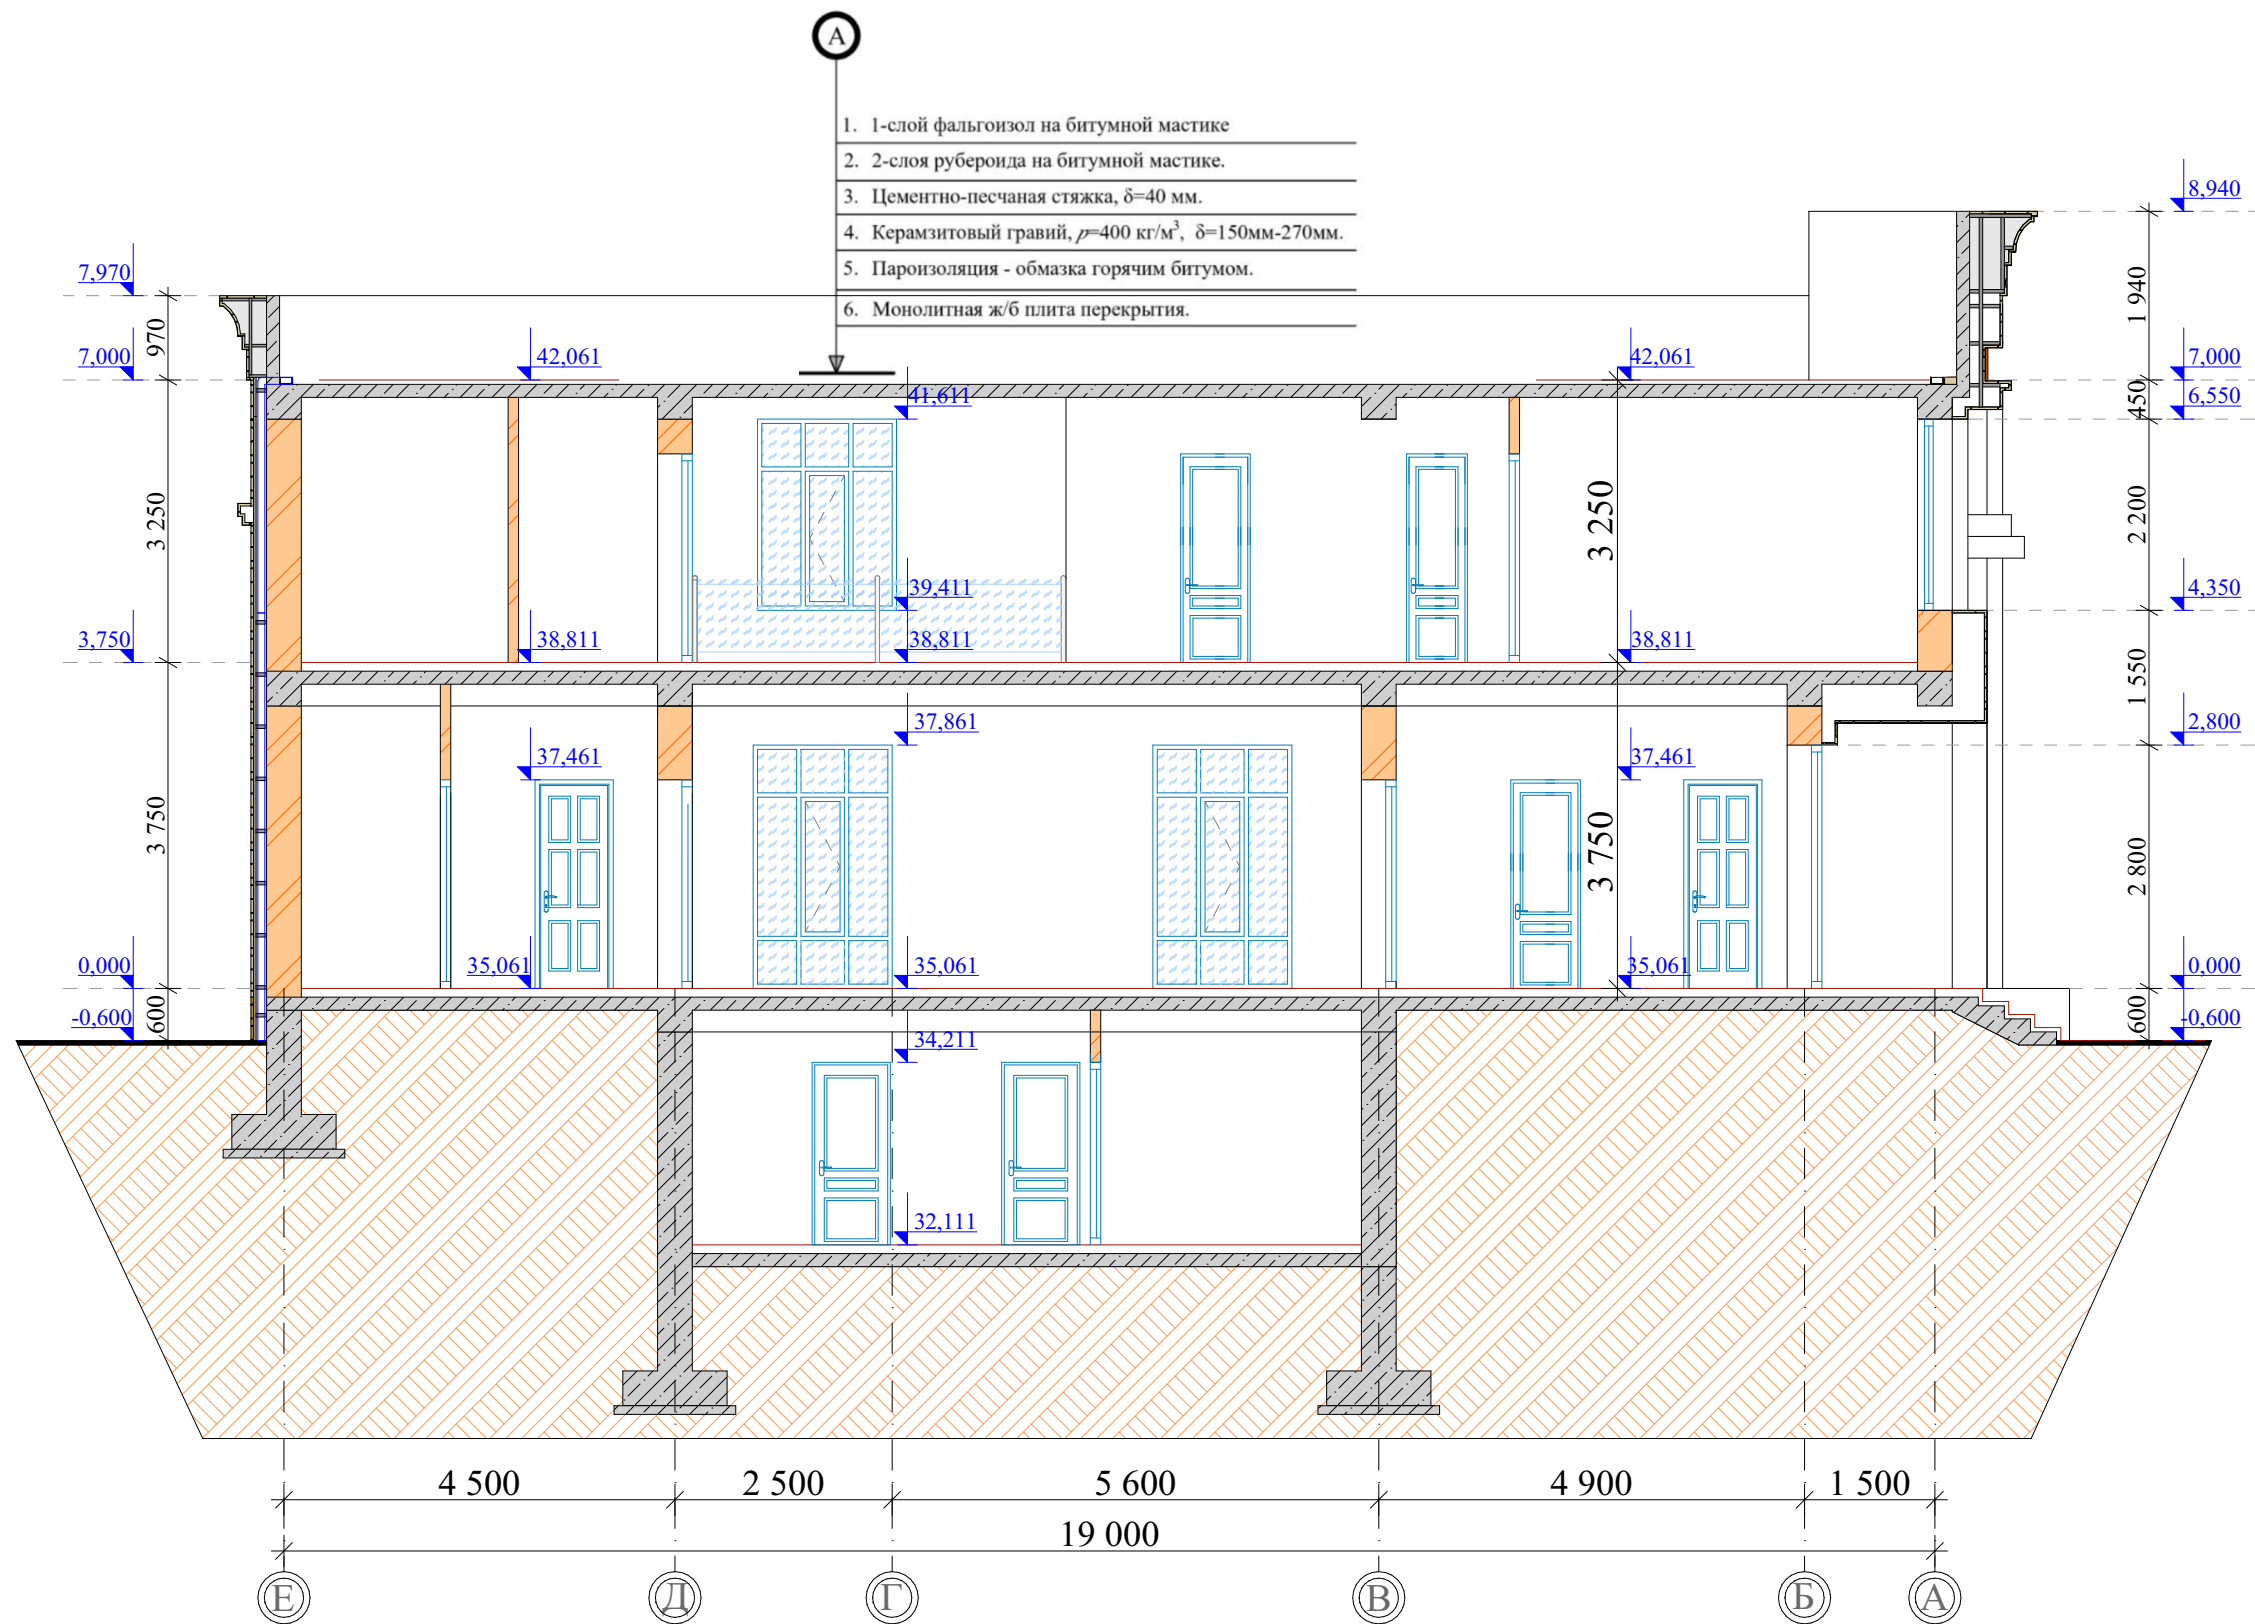














Узлы скрытого водостока под вентилируемый фасад

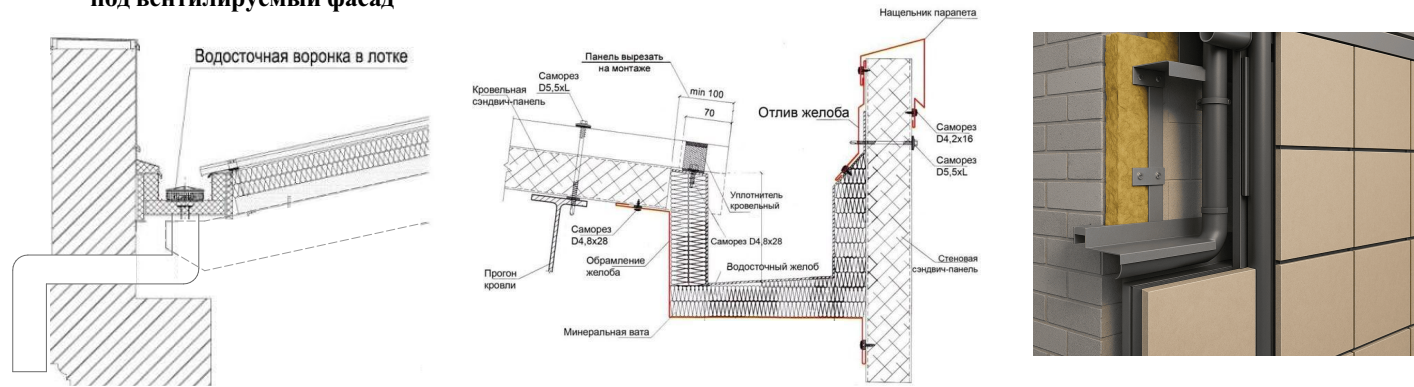

						АР				
Изм.	Кол.	Лист	№ док.	Подпись	Дата	Хонаи истиқоматӣ				
						Разрез 2-2				
ГИП	Рачабов С.									
ГАП	Рачабов С.									
								Стадия	Лист	Листов
								РП	25	26
Разраб.	Холов С.									

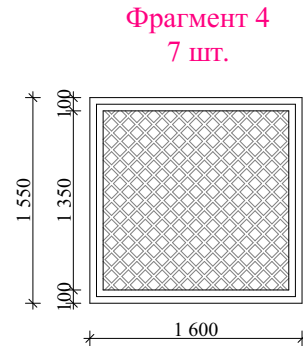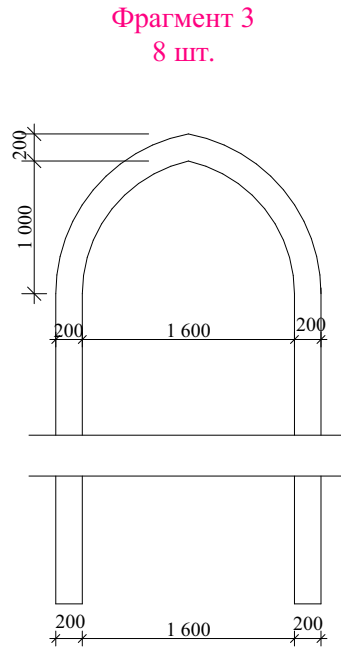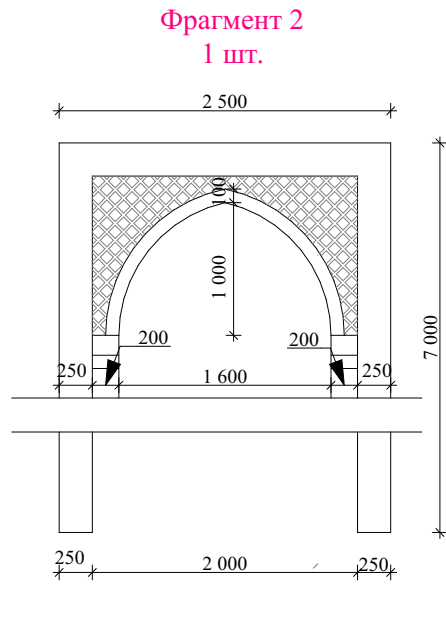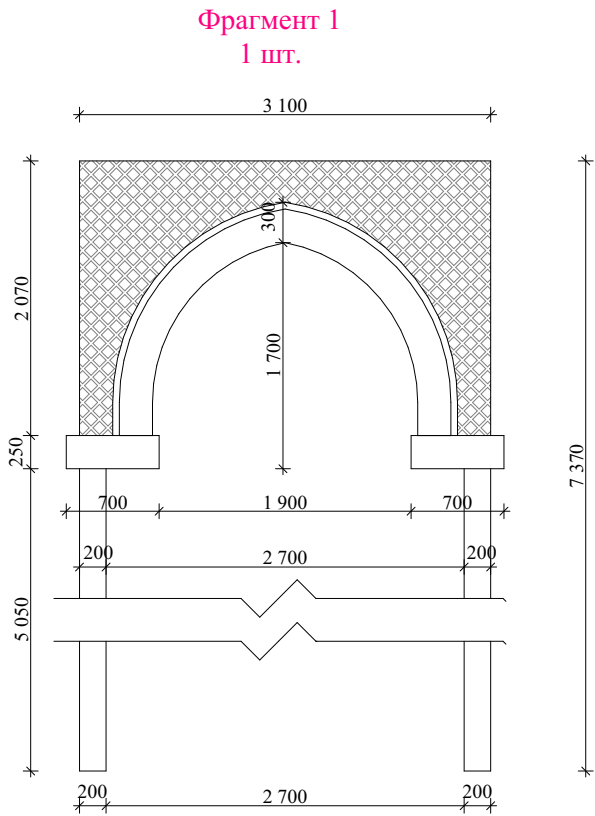

Ведомость отделки
фасадов

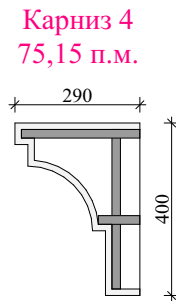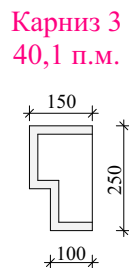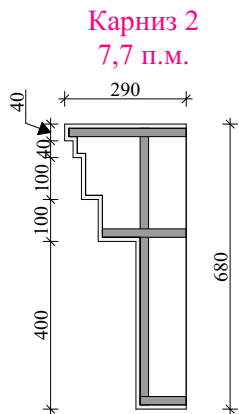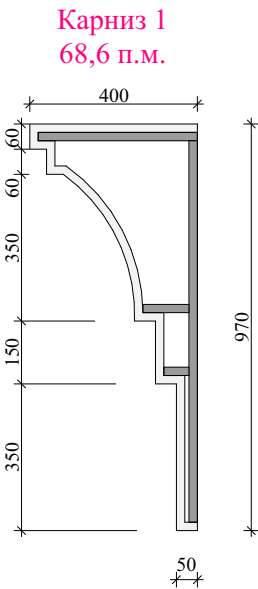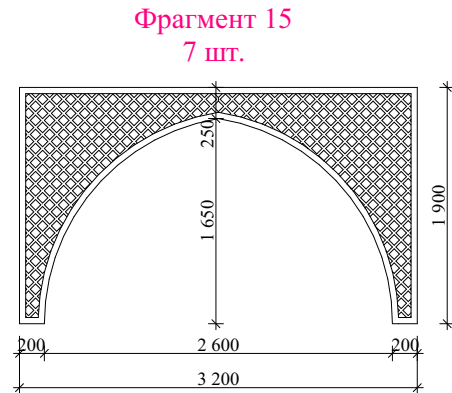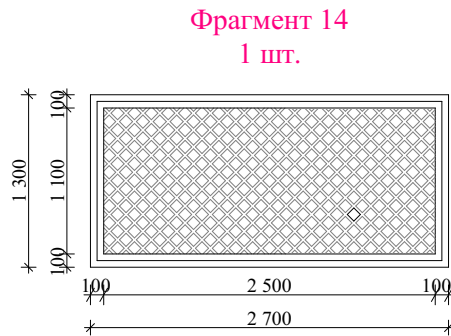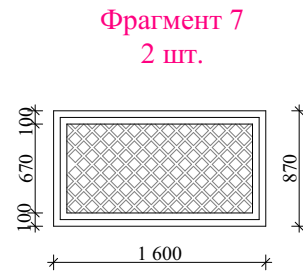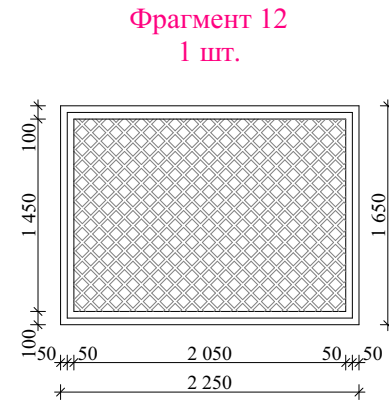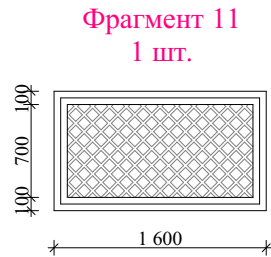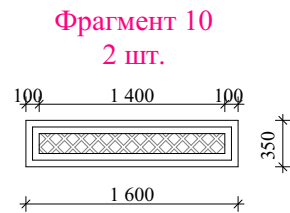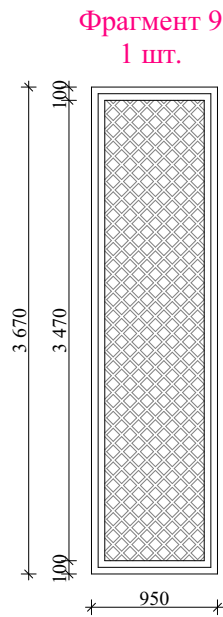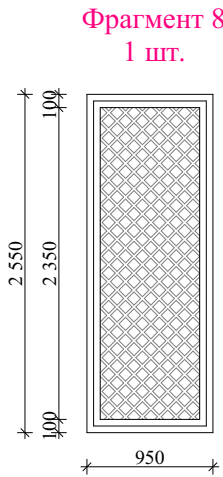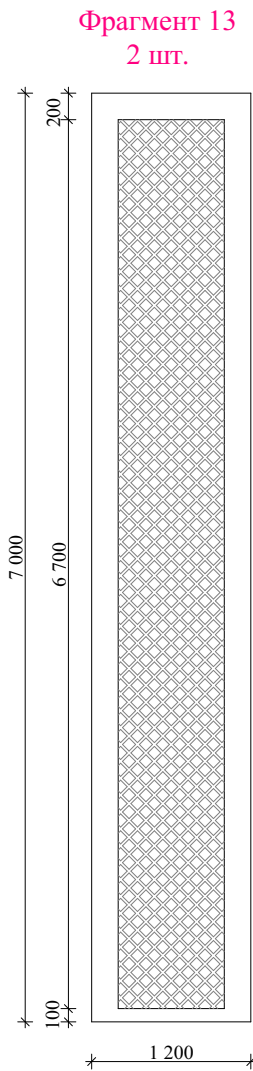

						АР			
Изм.	Кол.	Лист	№ док.	Подпись	Дата	Хонаи истиқоматӣ			
							Стадия	Лист	Листов
ГИП		Рачабов С.					РП	26	26
ГАП		Рачабов С.							
						Ведомость отделки фасадов			
Разраб.		Холов С.							