

Ведомость рабочих чертежей марки АР


| Лист  | Наименование                    | Примечание |
|-------|---------------------------------|------------|
| АР-1  | Общие данные                    |            |
| АР-2  | План гаража                     |            |
| АР-3  | Разрез гаража                   |            |
| АР-4  | Фасад навеса                    |            |
| АР-5  | План навеса                     |            |
| АР-6  | План кровли навеса              |            |
| АР-7  | Разрезы навеса                  |            |
| АР-8  | План вспомогательного помещения |            |
| АР-9  | Разбивочный план всп. помещения |            |
| АР-10 | План кровли всп. помещения      |            |
| АР-11 | Разрезы всп. помещения          |            |

Спецификация заполнения дверных и оконных проемов



| № поз. | Наименование | Размер проема<br>(мм×мм ) | Количество |        |       |                 |  |
|--------|--------------|---------------------------|------------|--------|-------|-----------------|--|
|        |              |                           | Гараж      | 1 этаж | Всего |                 |  |
| Двери  |              |                           |            |        |       |                 |  |
| 1      | Д-1          | 1200x2100                 | 2          |        | 2     | Металлический   |  |
| 2      | Д-2          | 2000x2100                 | 1          |        | 1     | Металлический   |  |
| 3      | Д-3          | 800x2400                  |            | 5      | 5     | Металло-пластик |  |
| 4      | Д-3'         | 800x2100                  | 1          |        | 1     | Металло-пластик |  |
| Окна   |              |                           |            |        |       |                 |  |
| 1      | Ок-1         | 1200x1500                 |            | 1      | 1     | Металло-пластик |  |

Исходные данные

|                                                |           |
|------------------------------------------------|-----------|
| 1. Климатический подрайон                      | IVГ       |
| 2. Расчётная температура наружного воздуха     | -15 °С    |
| 3. Нормативное значение ветрового давления     | 52 кгс/м2 |
| 4. Нормативное значение веса снегового покрова | 84 кг/м2  |
| 5. Сейсмичность участка строительства          | 8 баллов  |
| 6. Степень огнестойкости                       | II        |

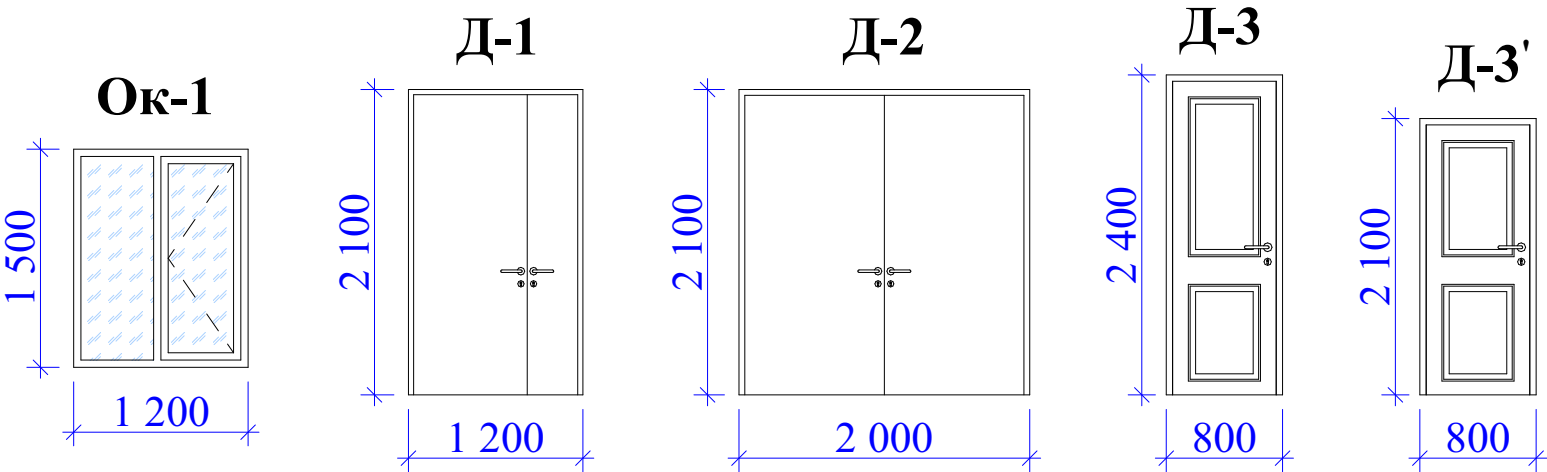


|         |      |            |        |         |      |                  |  |        |      |        |
|---------|------|------------|--------|---------|------|------------------|--|--------|------|--------|
|         |      |            |        |         |      | АР               |  |        |      |        |
| Изм.    | Кол. | Лист       | № док. | Подпись | Дата | Хонаи истиқоматӣ |  |        |      |        |
|         |      |            |        |         |      |                  |  |        |      |        |
|         |      |            |        |         |      |                  |  |        |      |        |
|         |      |            |        |         |      | Общие данные     |  | Стадия | Лист | Листов |
| ГИП     |      | Рачабов С. |        |         |      |                  |  | РП     | 1    | 11     |
| ГАП     |      | Рачабов С. |        |         |      |                  |  |        |      |        |
|         |      |            |        |         |      |                  |  |        |      |        |
| Разраб. |      | Холов С.   |        |         |      |                  |  |        |      |        |
|         |      |            |        |         |      |                  |  |        |      |        |

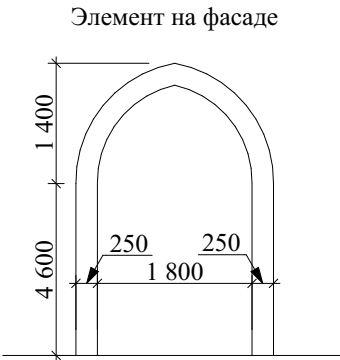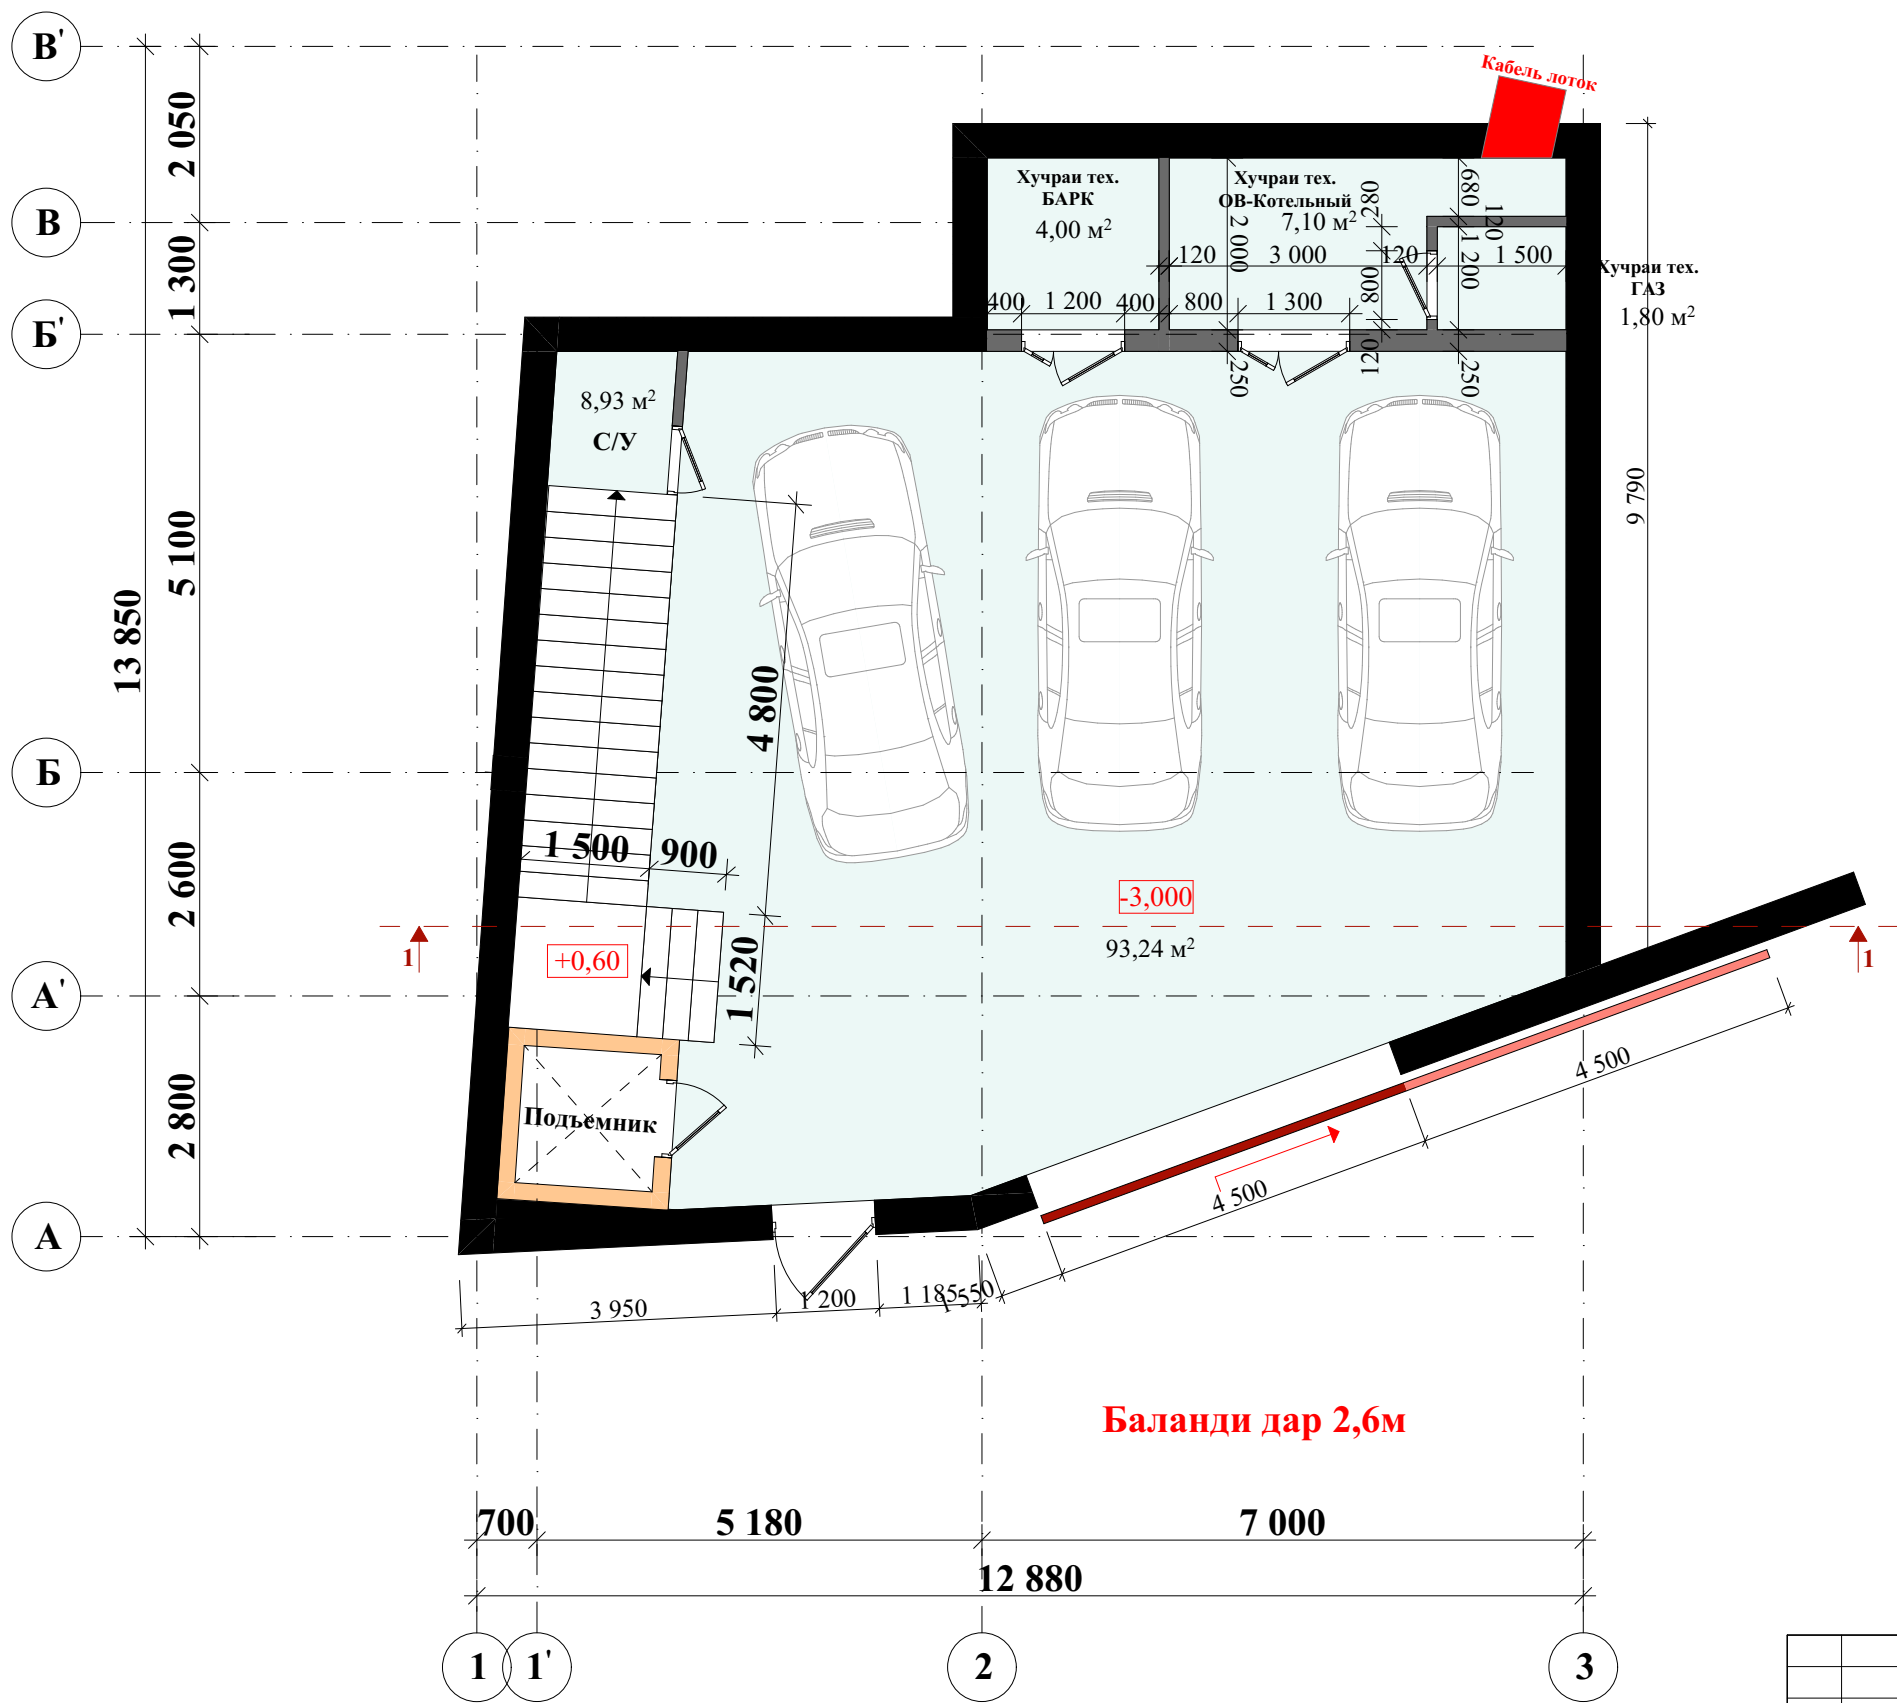


|         |      |            |        |         |      |                  |        |      |        |
|---------|------|------------|--------|---------|------|------------------|--------|------|--------|
|         |      |            |        |         |      | АР               |        |      |        |
| Изм.    | Кол. | Лист       | № док. | Подпись | Дата | Хонаи истиқоматӣ |        |      |        |
|         |      |            |        |         |      |                  |        |      |        |
|         |      |            |        |         |      | План гаража      | Стадия | Лист | Листов |
| ГИП     |      | Раҷабов С. |        |         |      |                  | РП     | 2    | 11     |
| ГАП     |      | Раҷабов С. |        |         |      |                  |        |      |        |
| Разраб. |      | Холов С.   |        |         |      |                  |        |      |        |

Разрез гаража 1-1

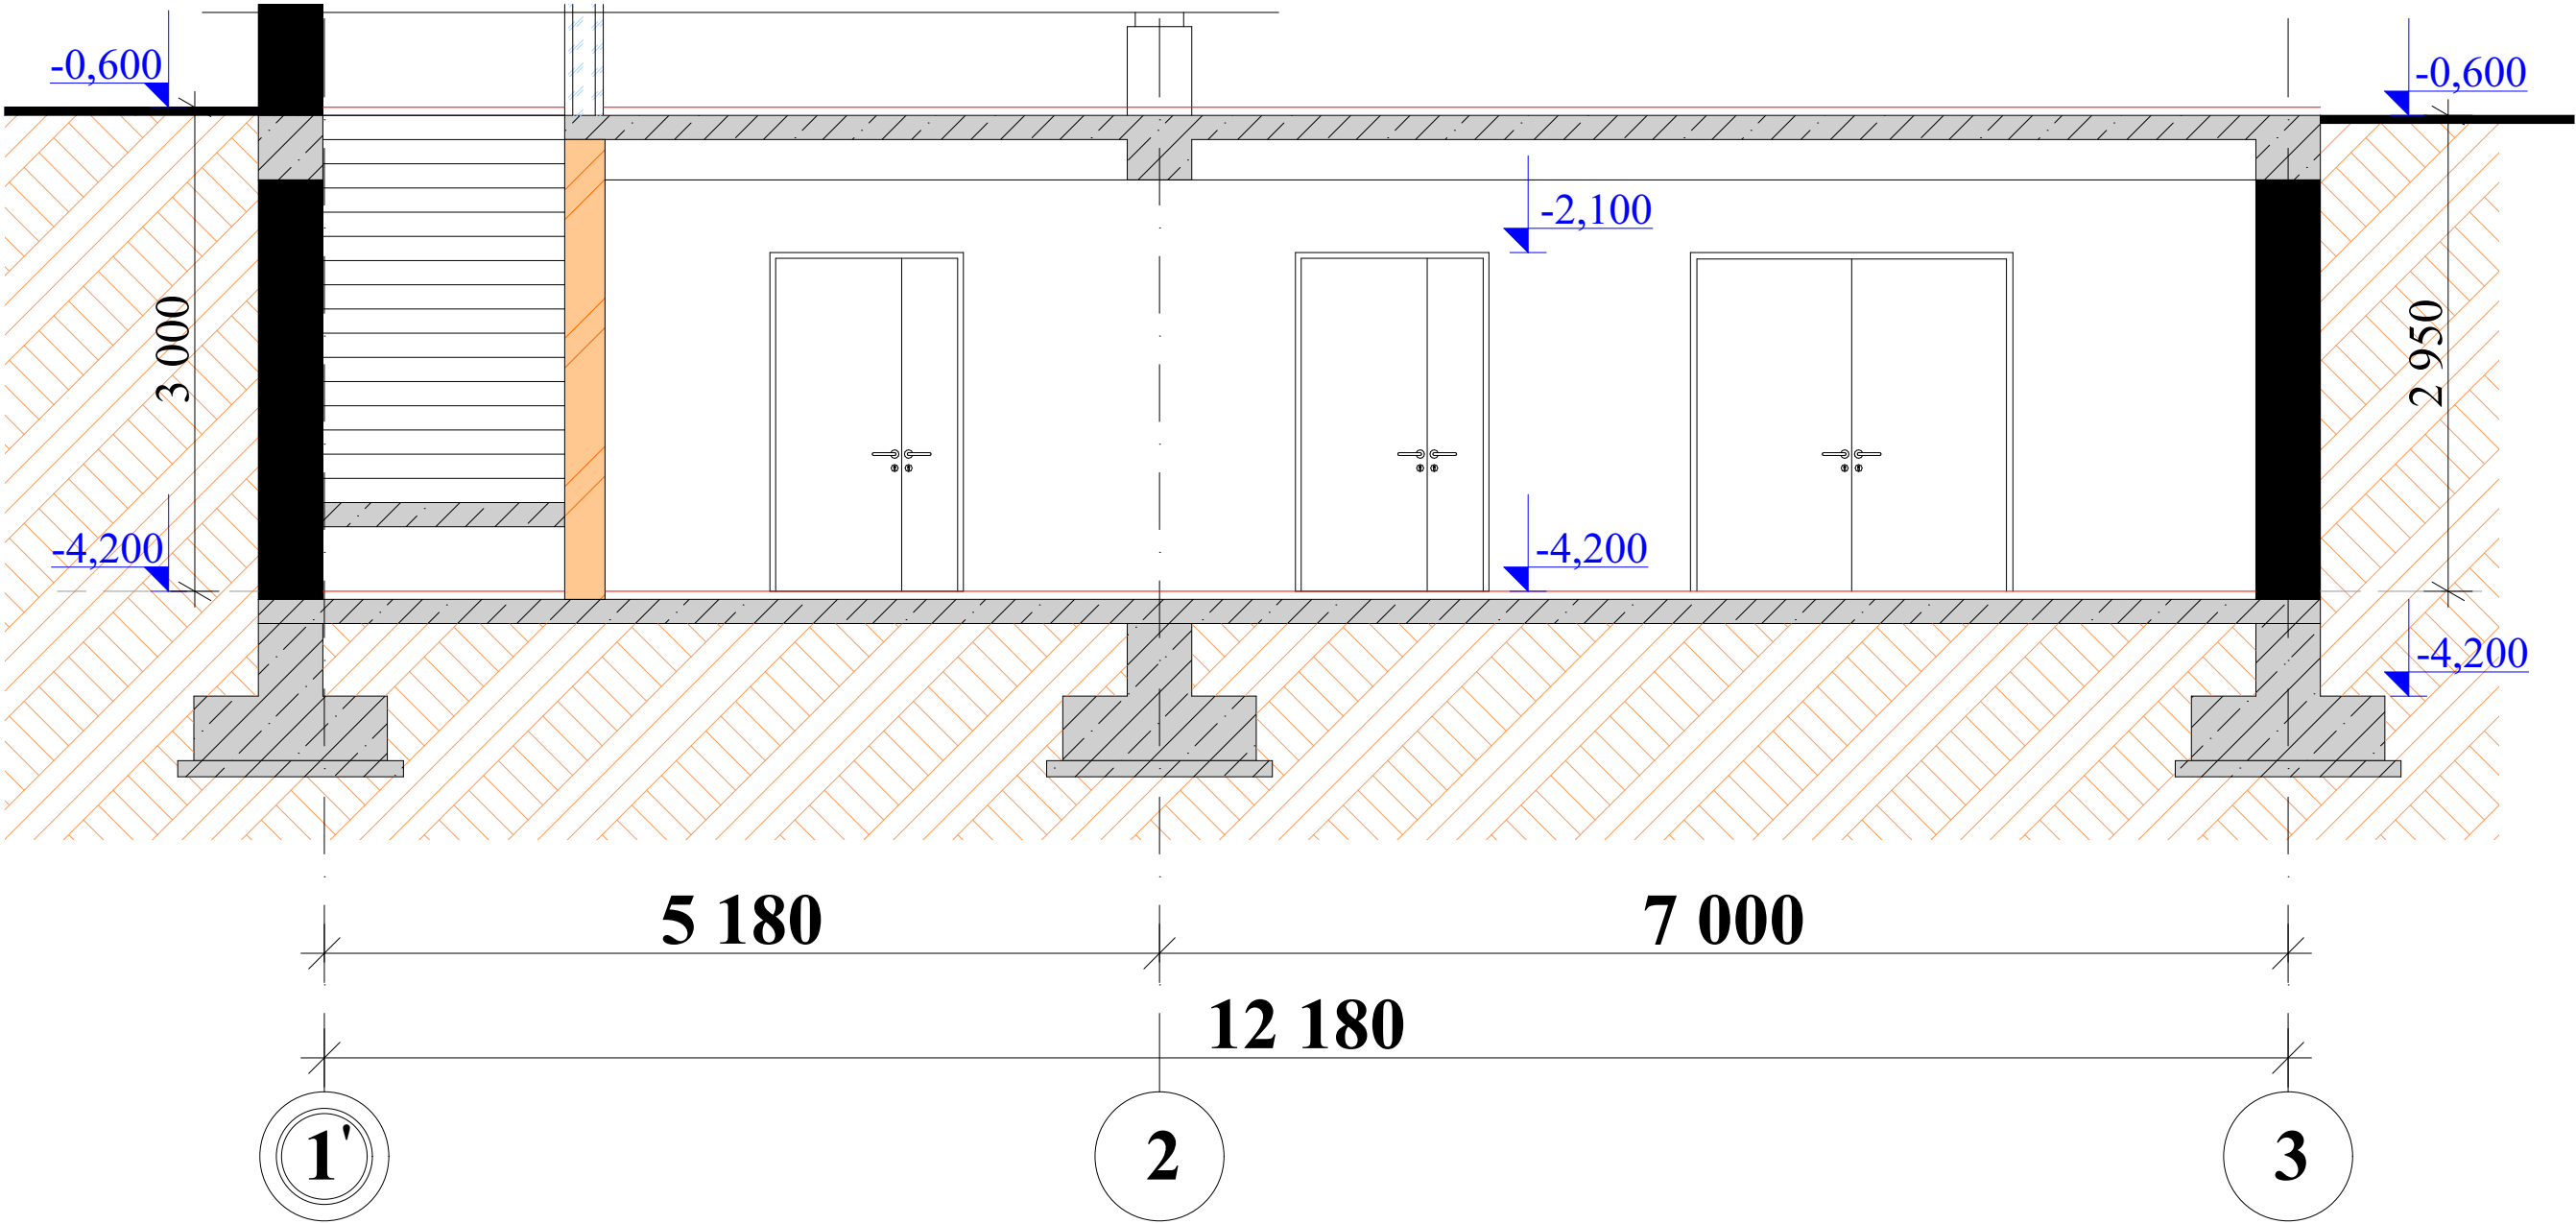


|         |      |            |        |         |      |                   |        |      |        |
|---------|------|------------|--------|---------|------|-------------------|--------|------|--------|
|         |      |            |        |         |      | АР                |        |      |        |
| Изм.    | Кол. | Лист       | № док. | Подпись | Дата | Хонаи истиқоматӣ  |        |      |        |
|         |      |            |        |         |      |                   |        |      |        |
|         |      |            |        |         |      |                   |        |      |        |
| ГИП     |      | Рачабов С. |        |         |      |                   | Стадия | Лист | Листов |
| ГАП     |      | Рачабов С. |        |         |      |                   | РП     | 3    | 11     |
|         |      |            |        |         |      | Разрез гаража 1-1 |        |      |        |
| Разраб. |      | Холов С.   |        |         |      |                   |        |      |        |
|         |      |            |        |         |      |                   |        |      |        |

План навеса

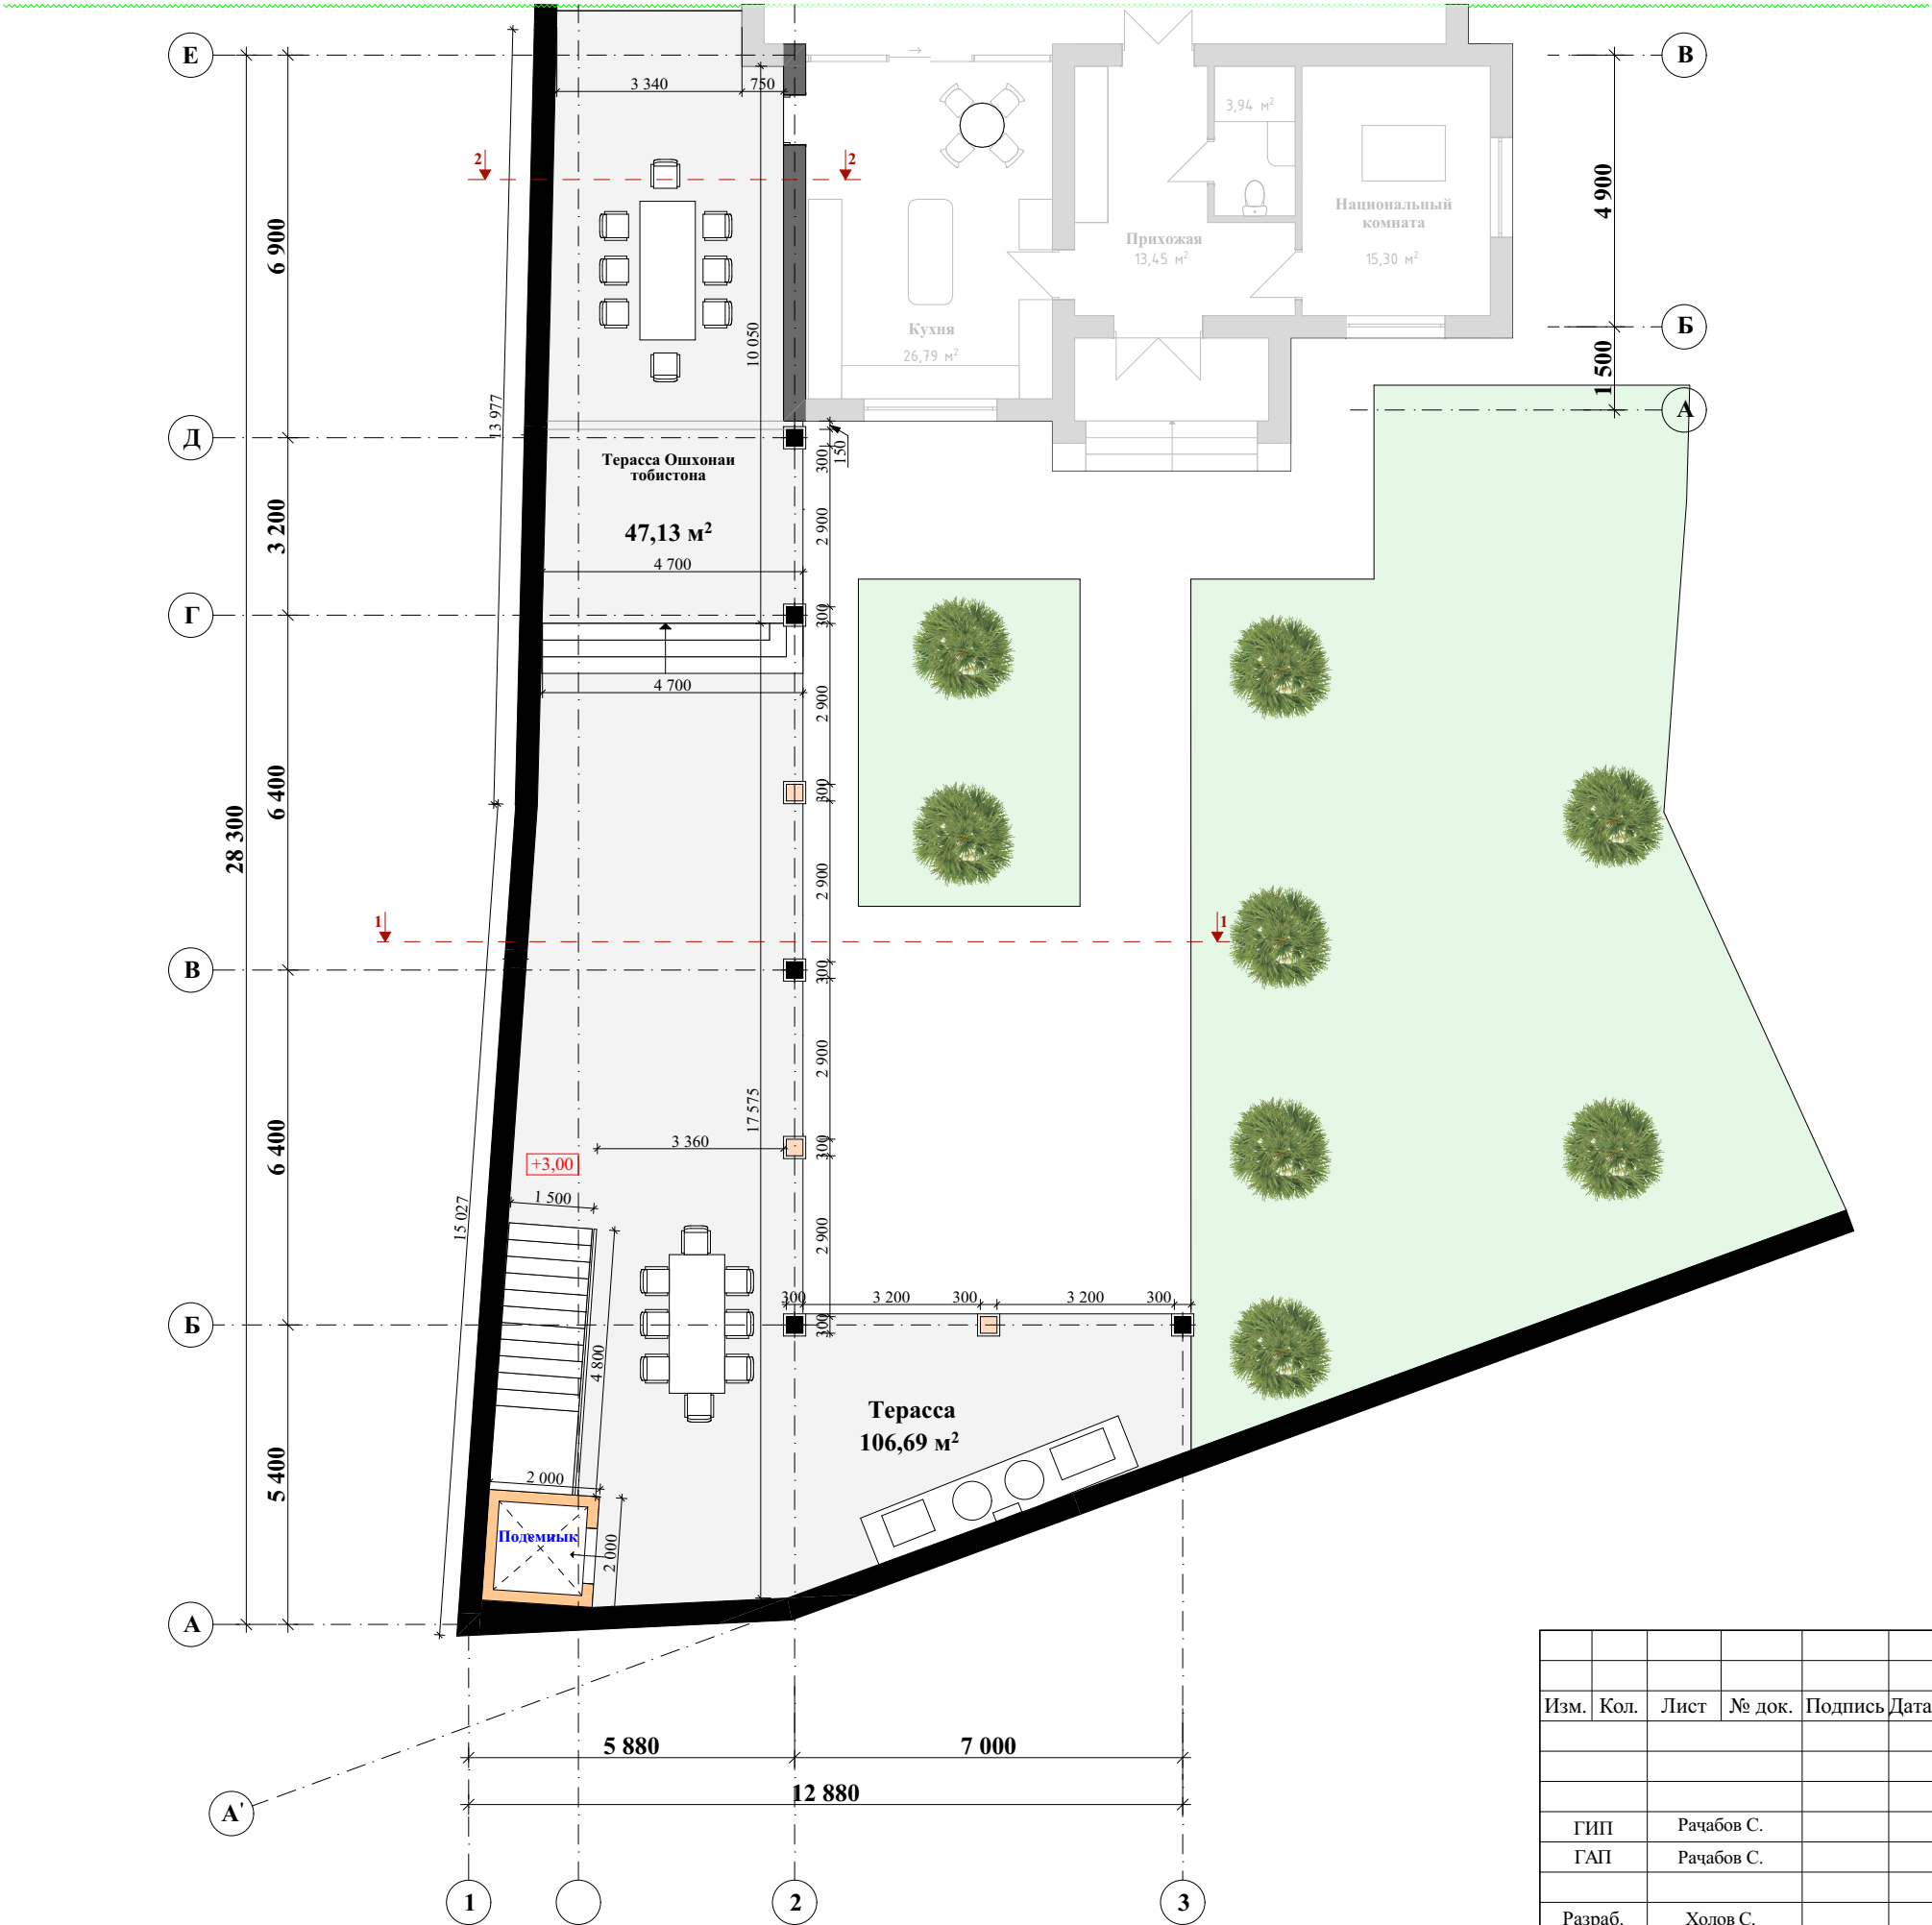

|         |      |            |        |         |      |                  |        |      |        |
|---------|------|------------|--------|---------|------|------------------|--------|------|--------|
|         |      |            |        |         |      | АР               |        |      |        |
| Изм.    | Кол. | Лист       | № док. | Подпись | Дата | Хонаи истиқоматӣ |        |      |        |
|         |      |            |        |         |      |                  |        |      |        |
|         |      |            |        |         |      |                  | Стадия | Лист | Листов |
| ГИП     |      | Раҷабов С. |        |         |      |                  | РП     | 5    | 11     |
| ГАП     |      | Раҷабов С. |        |         |      |                  |        |      |        |
| Разраб. |      | Холов С.   |        |         |      | План навеса      |        |      |        |

План кровли навеса

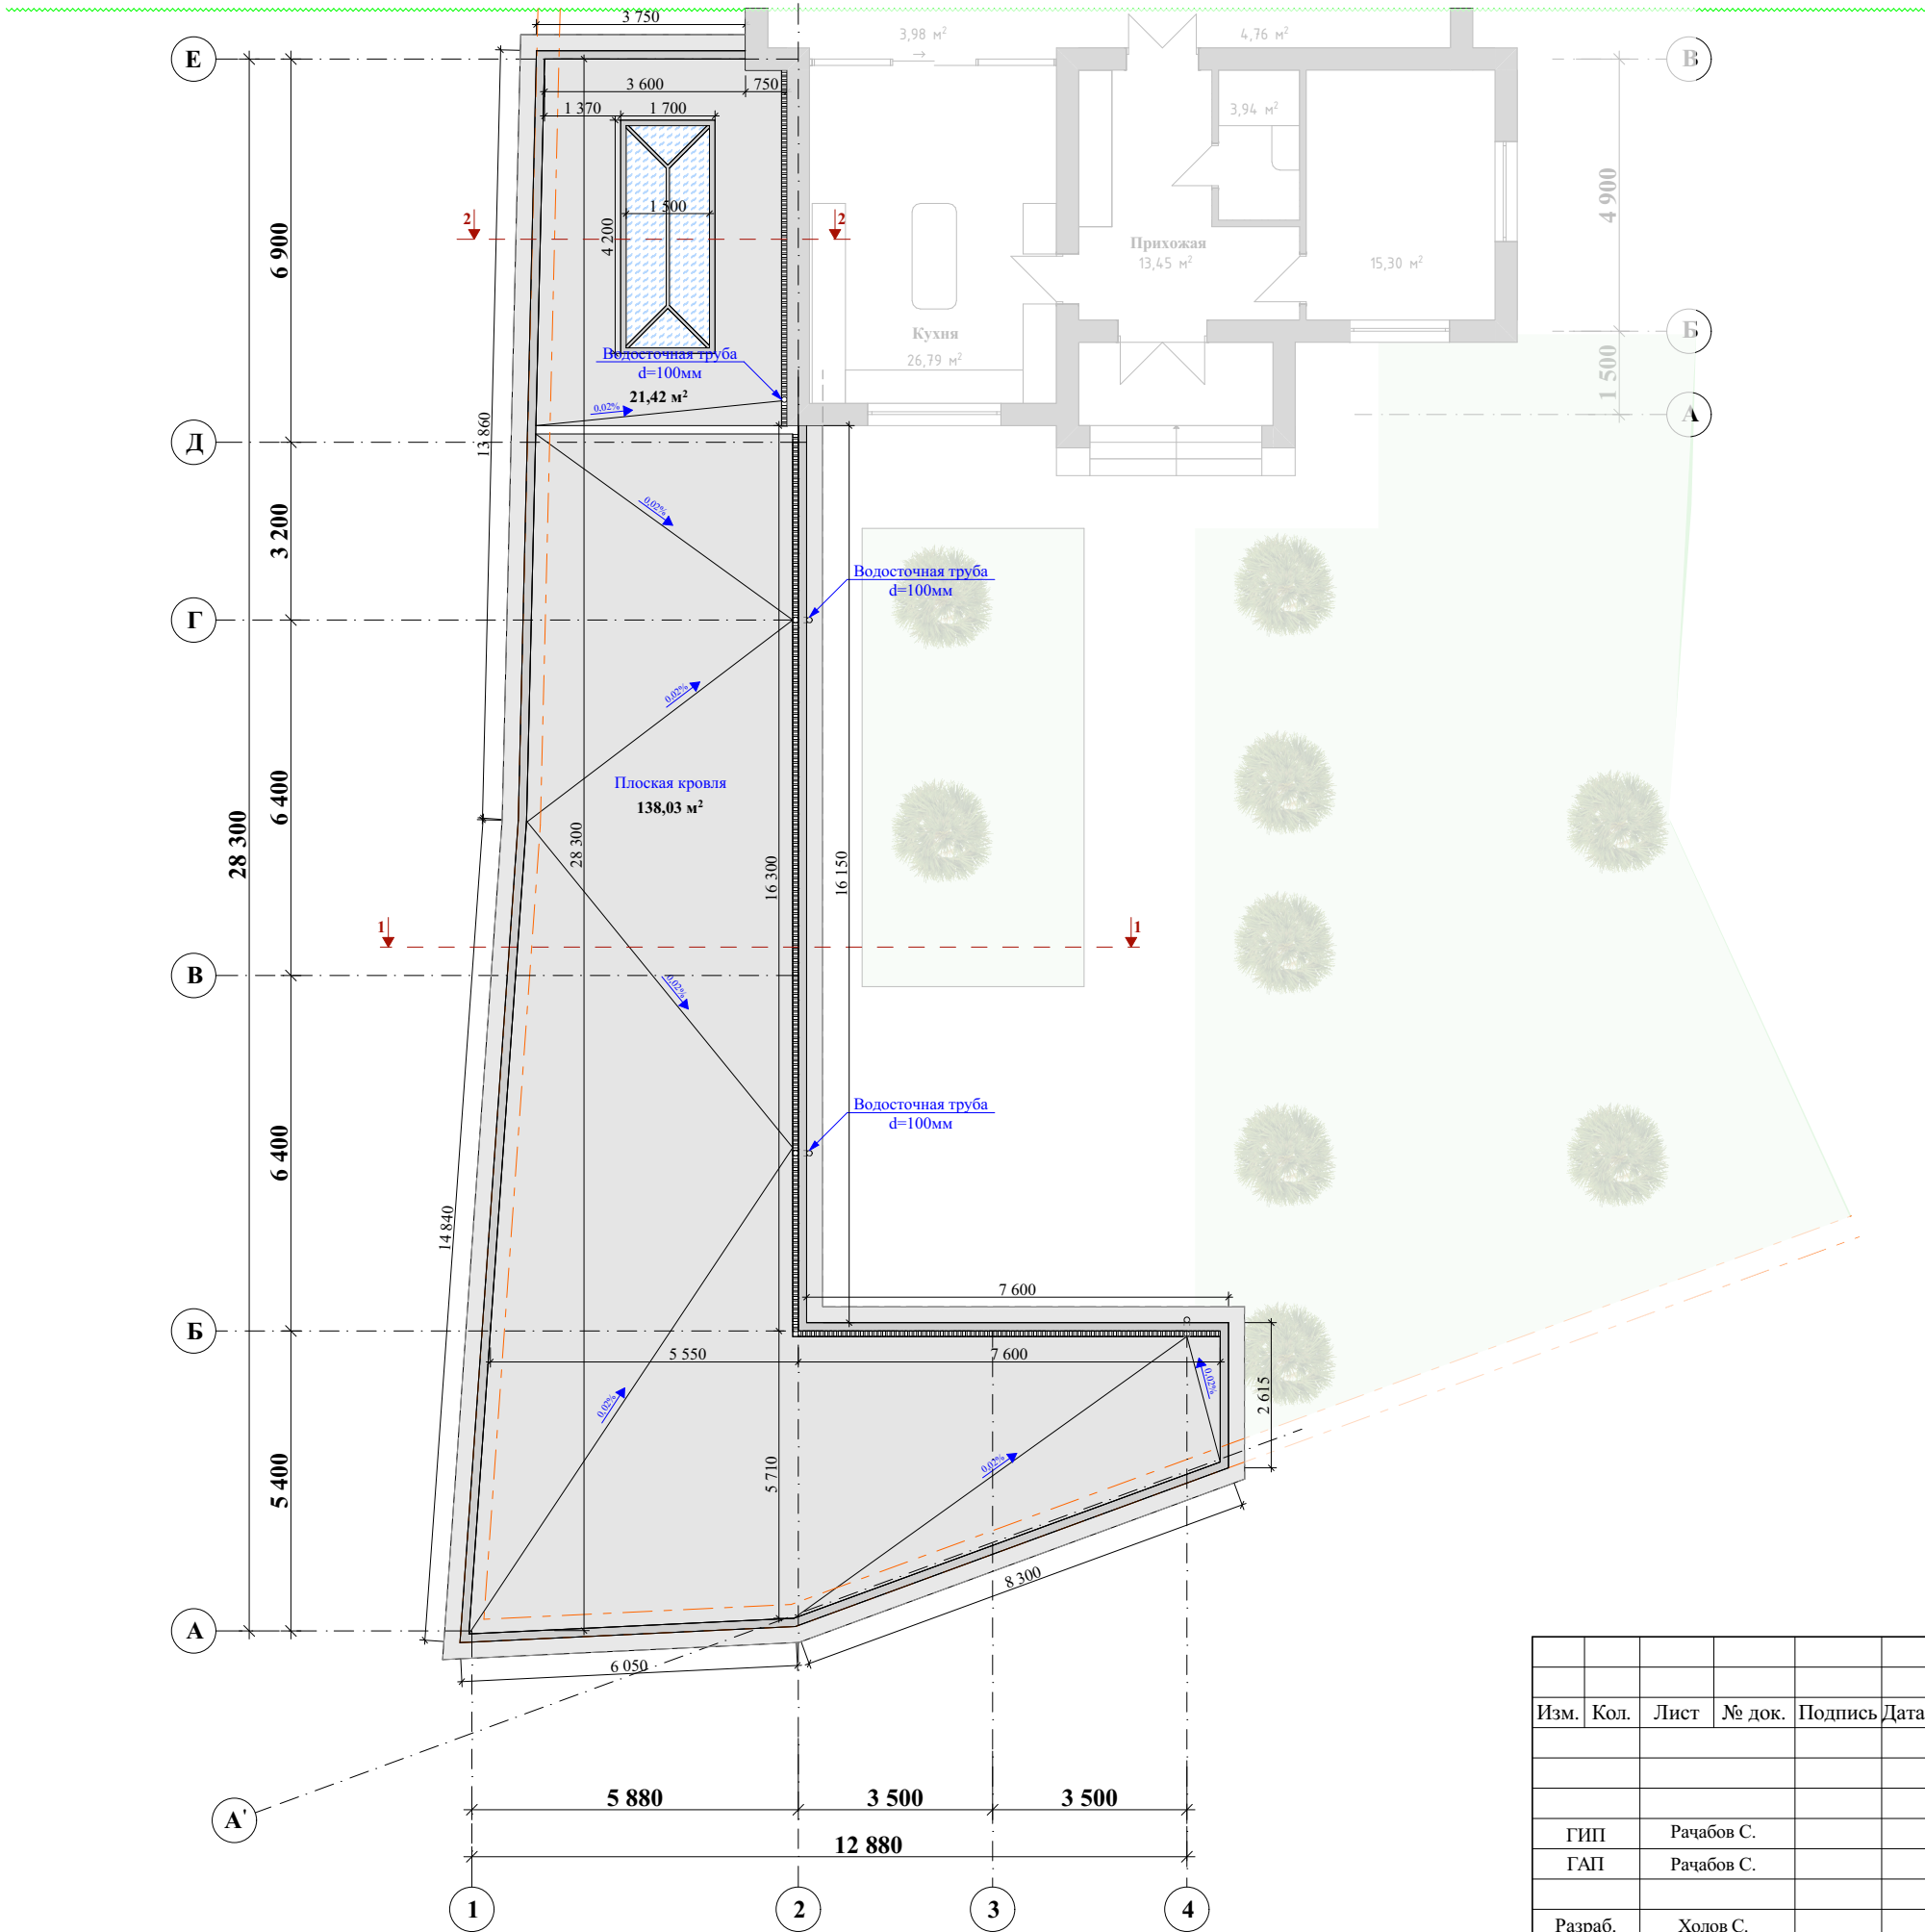

|         |      |            |        |         |      |                    |        |      |        |
|---------|------|------------|--------|---------|------|--------------------|--------|------|--------|
|         |      |            |        |         |      | АР                 |        |      |        |
| Изм.    | Кол. | Лист       | № док. | Подпись | Дата | Хонаи истиқоматӣ   |        |      |        |
|         |      |            |        |         |      |                    |        |      |        |
|         |      |            |        |         |      |                    | Стадия | Лист | Листов |
| ГИП     |      | Раҷабов С. |        |         |      |                    | РП     | 6    | 11     |
| ГАП     |      | Раҷабов С. |        |         |      |                    |        |      |        |
| Разраб. |      | Холов С.   |        |         |      | План кровли навеса |        |      |        |