



[illegible]

План подвального этажа на отм. -2,950

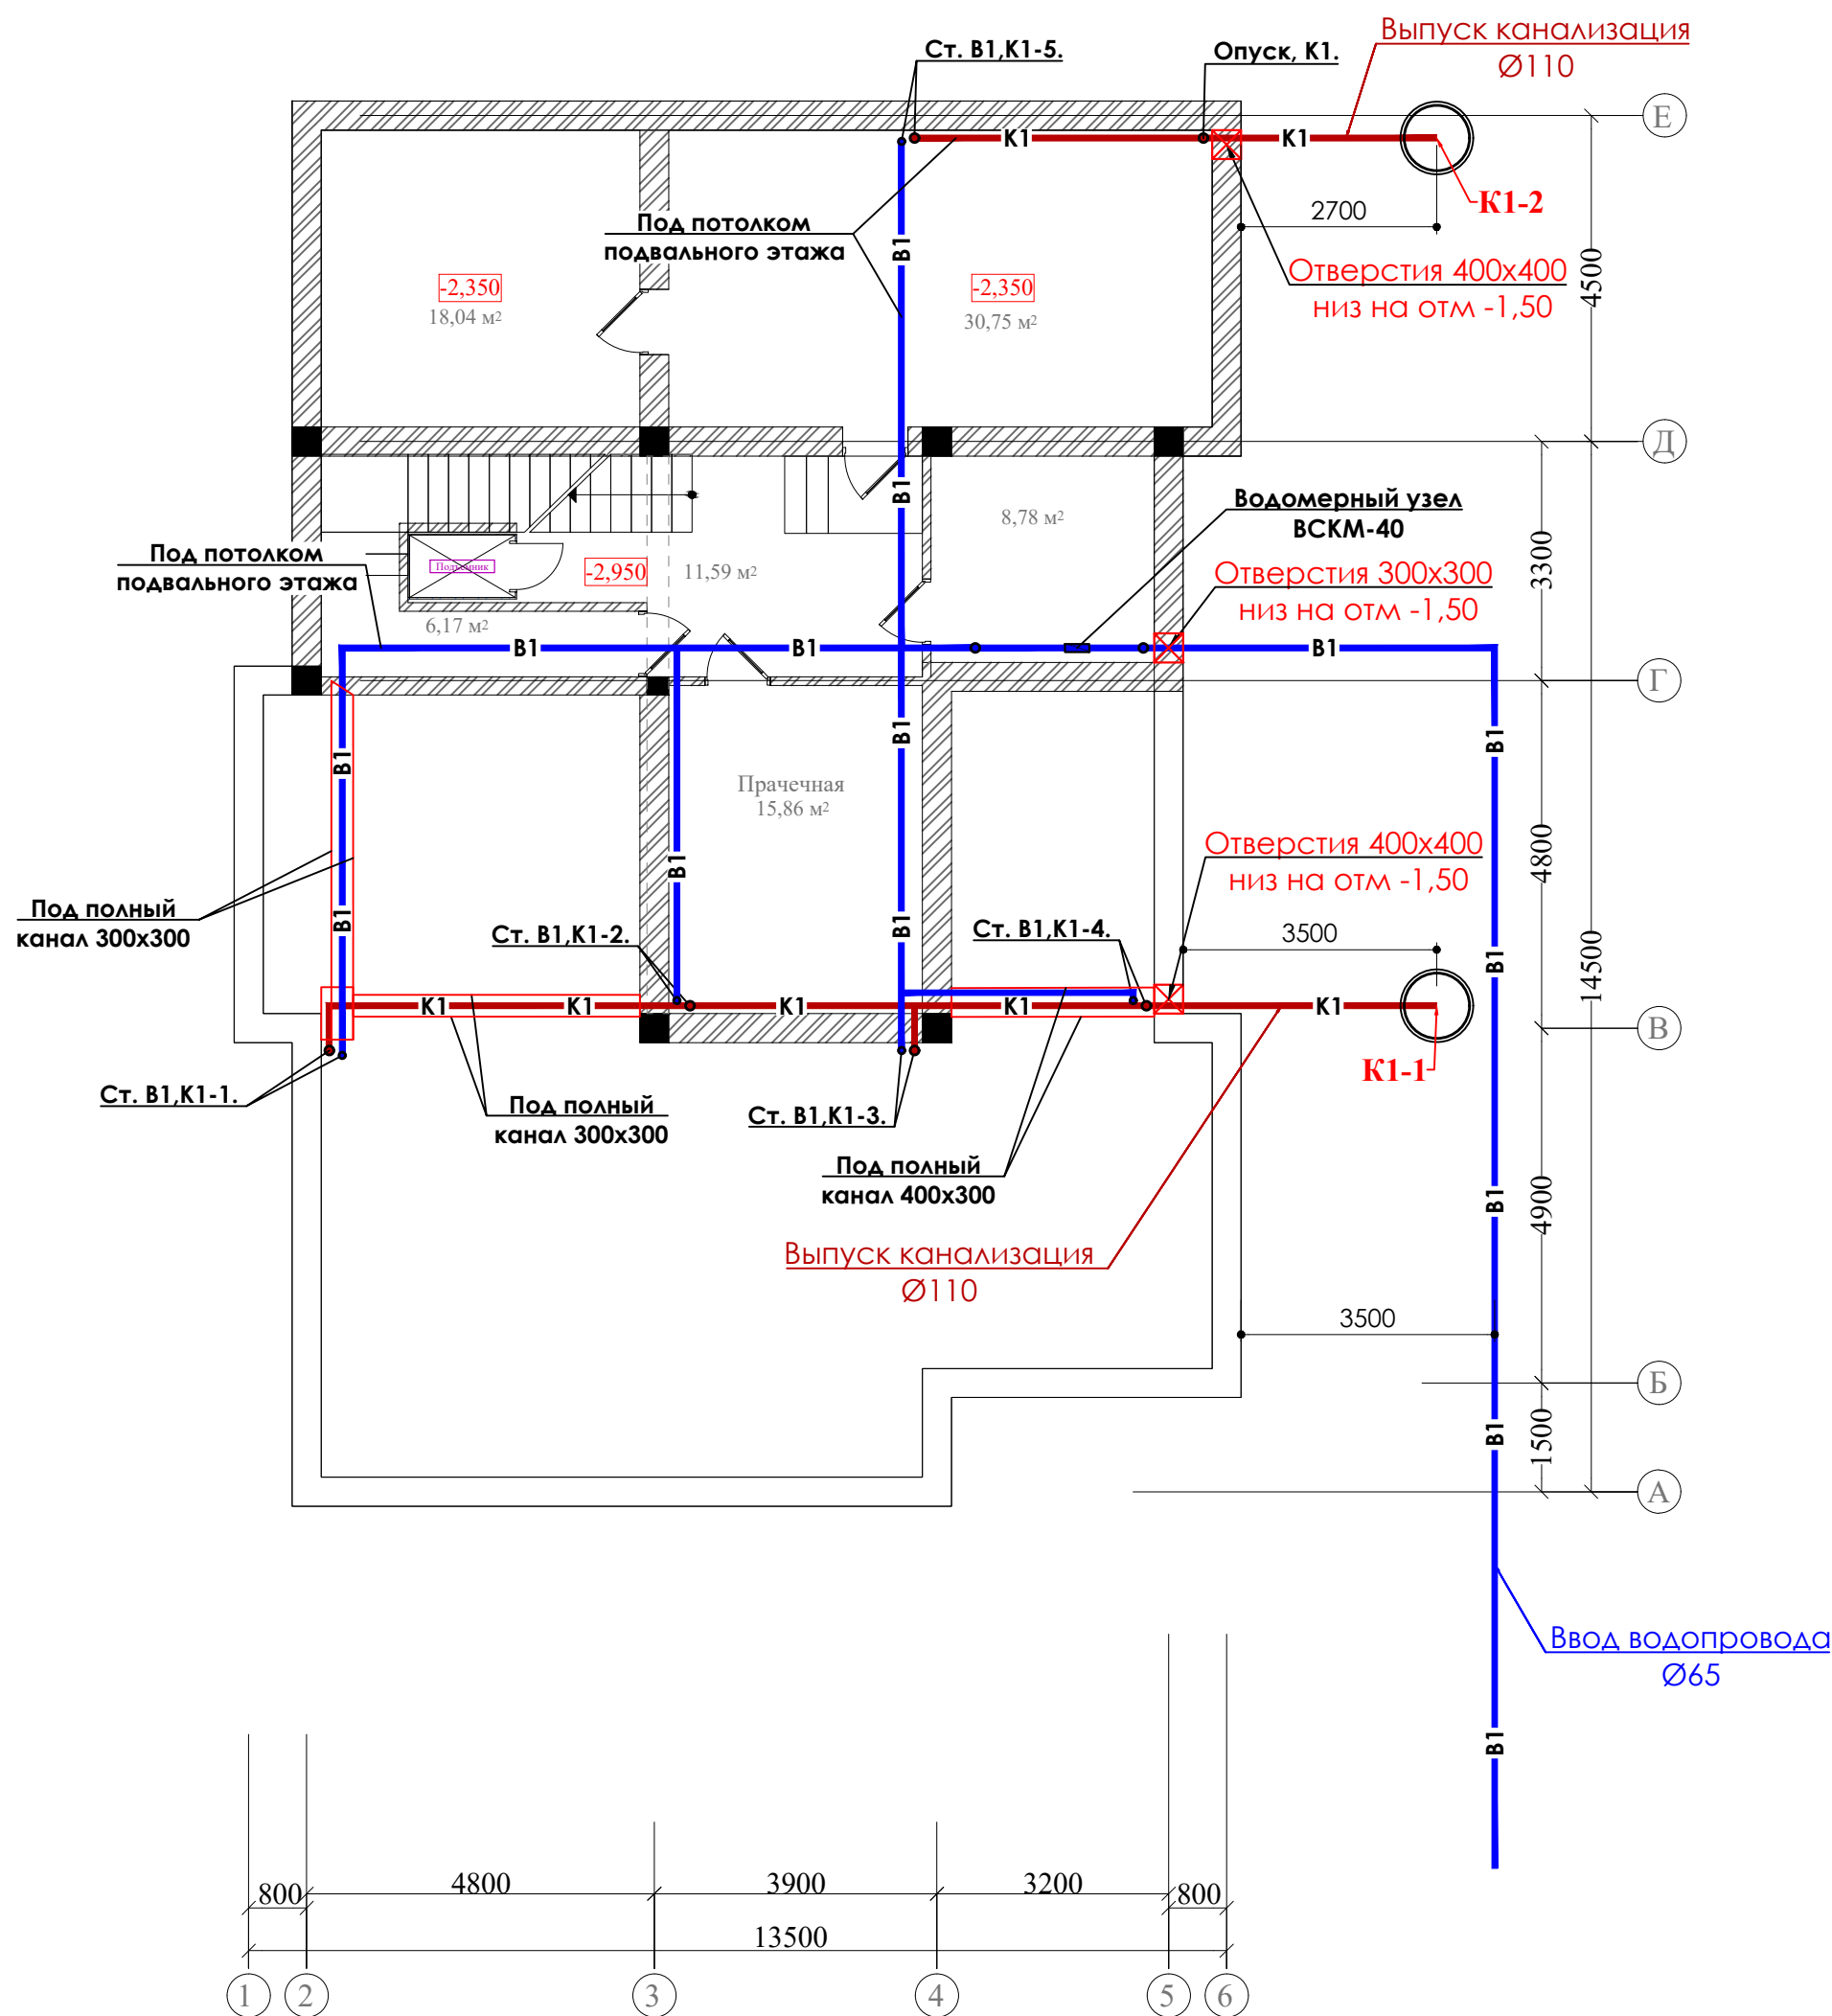


						ВК			
						"Соҳтмони биноҳои истикомати (Котедж)"			
Изм.	Кол.	Лист	№ док.	Подпись	Дата	Кисми обтаъминкуни ва корези.	Стадия	Лист	Листов
ГИП		00000			2026		РП	2	7
Разраб.		Халимов С			2026				

План 1-го этажа на отм. 0,000

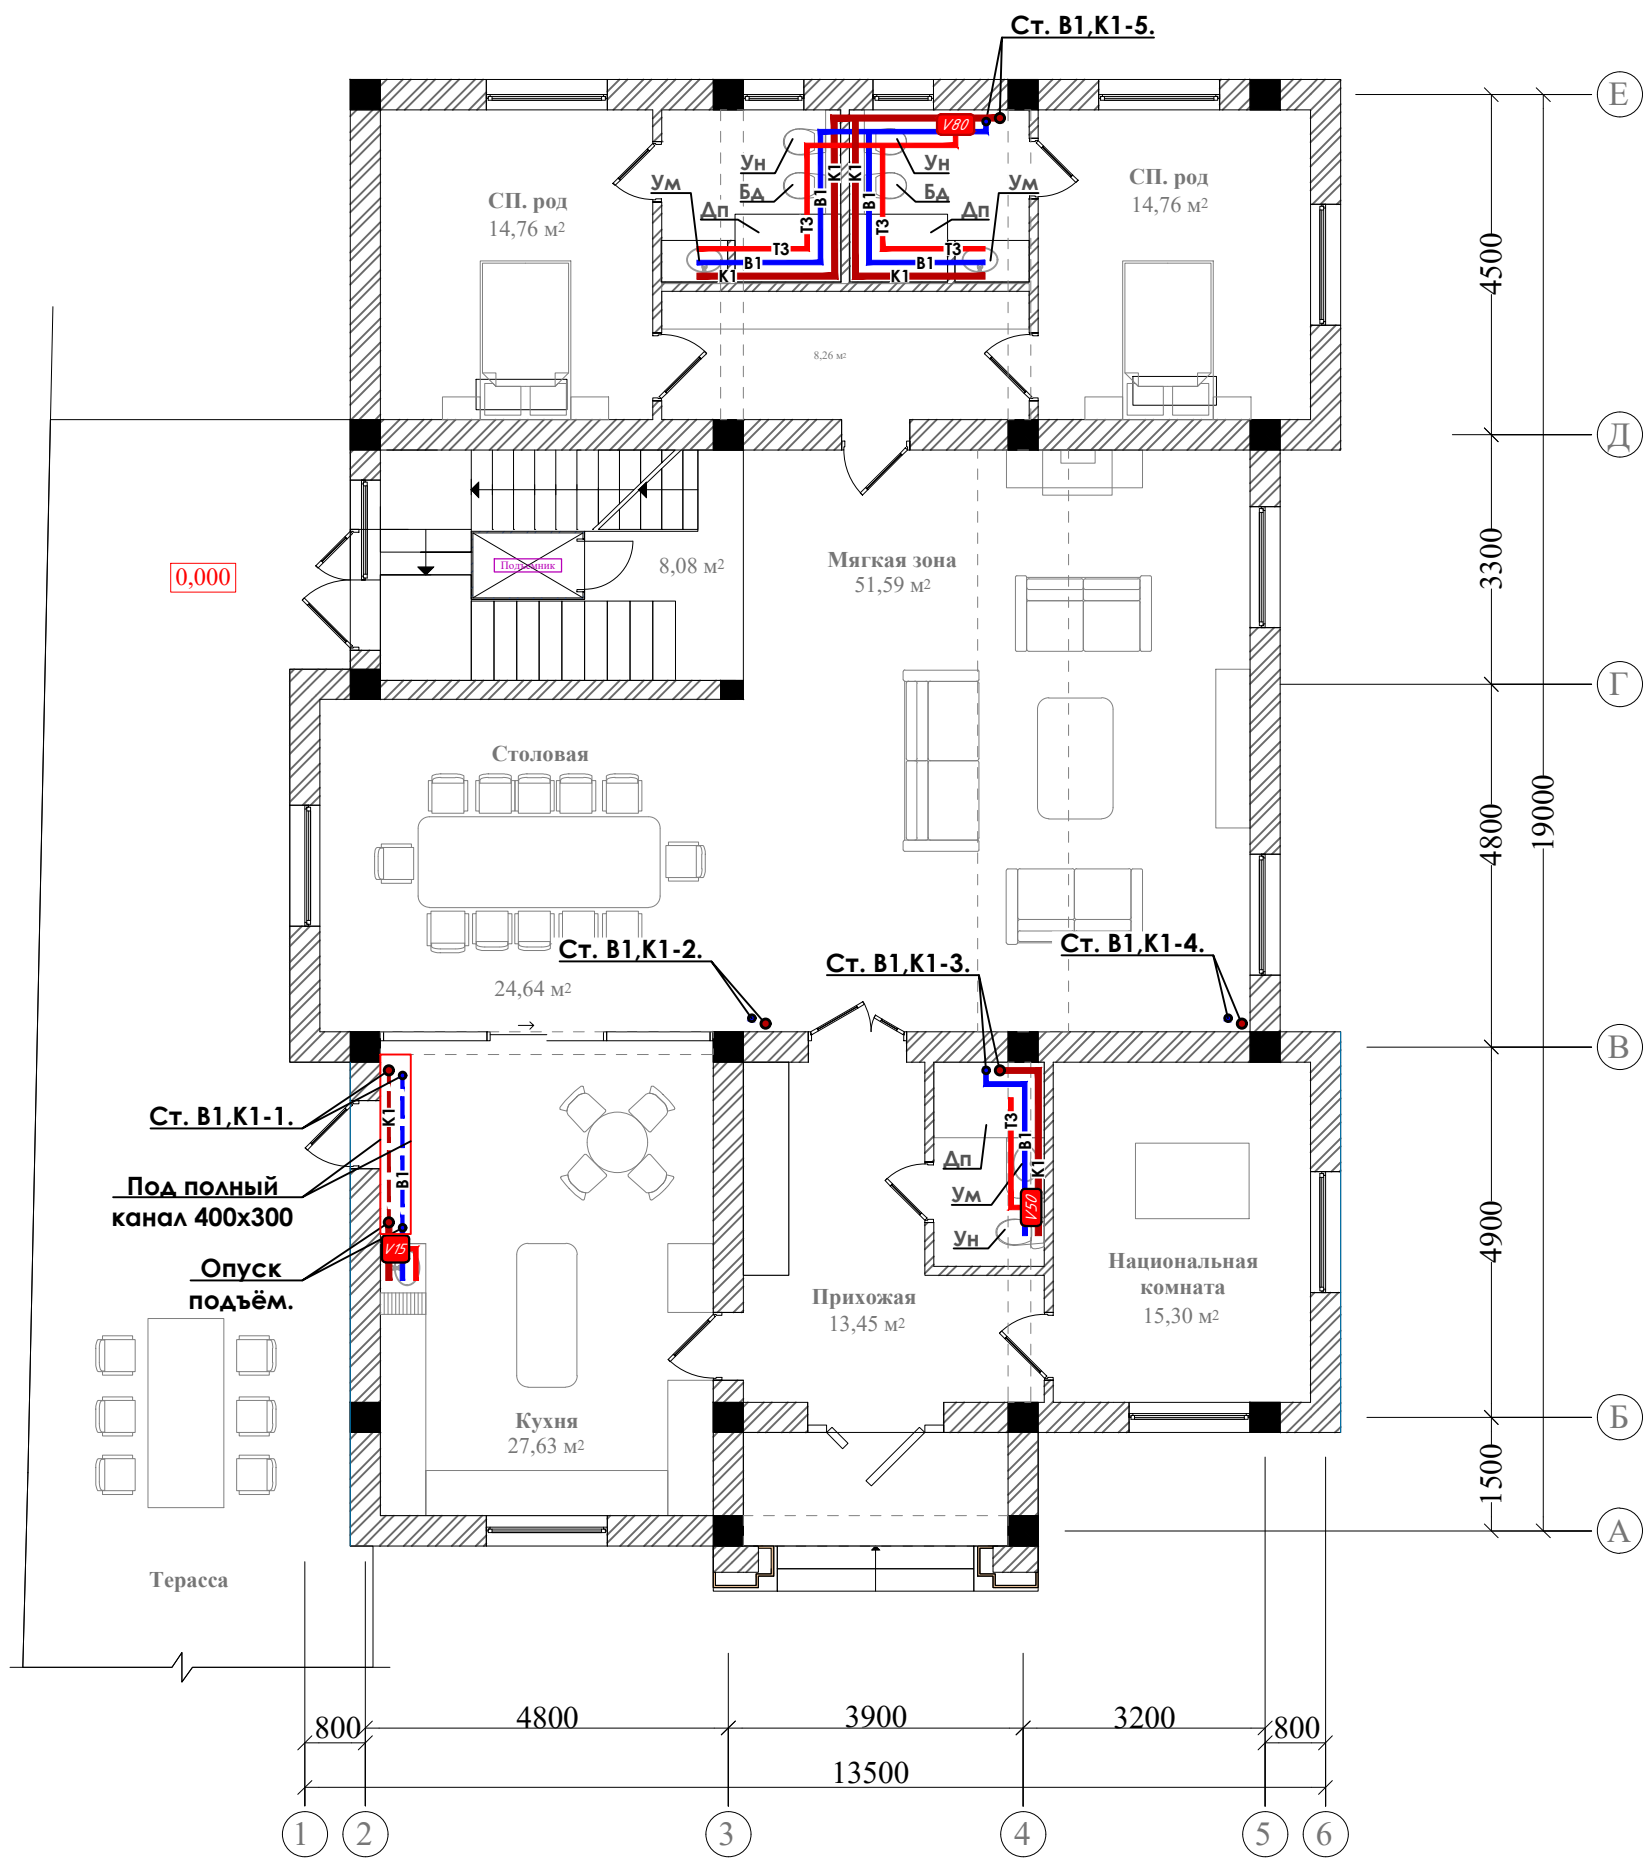


						ВК			
						"Соҳтмони биноҳои истикомати (Котедж)"			
Изм.	Кол.	Лист	№ док.	Подпись	Дата				
						Кисми обтаъминкуни ва корези.	Стадия	Лист	Листов
ГИП		00000			2026		РП	3	7
Разраб.		Халимов С			2026				

План 2-го этажа нп отм. +3,750


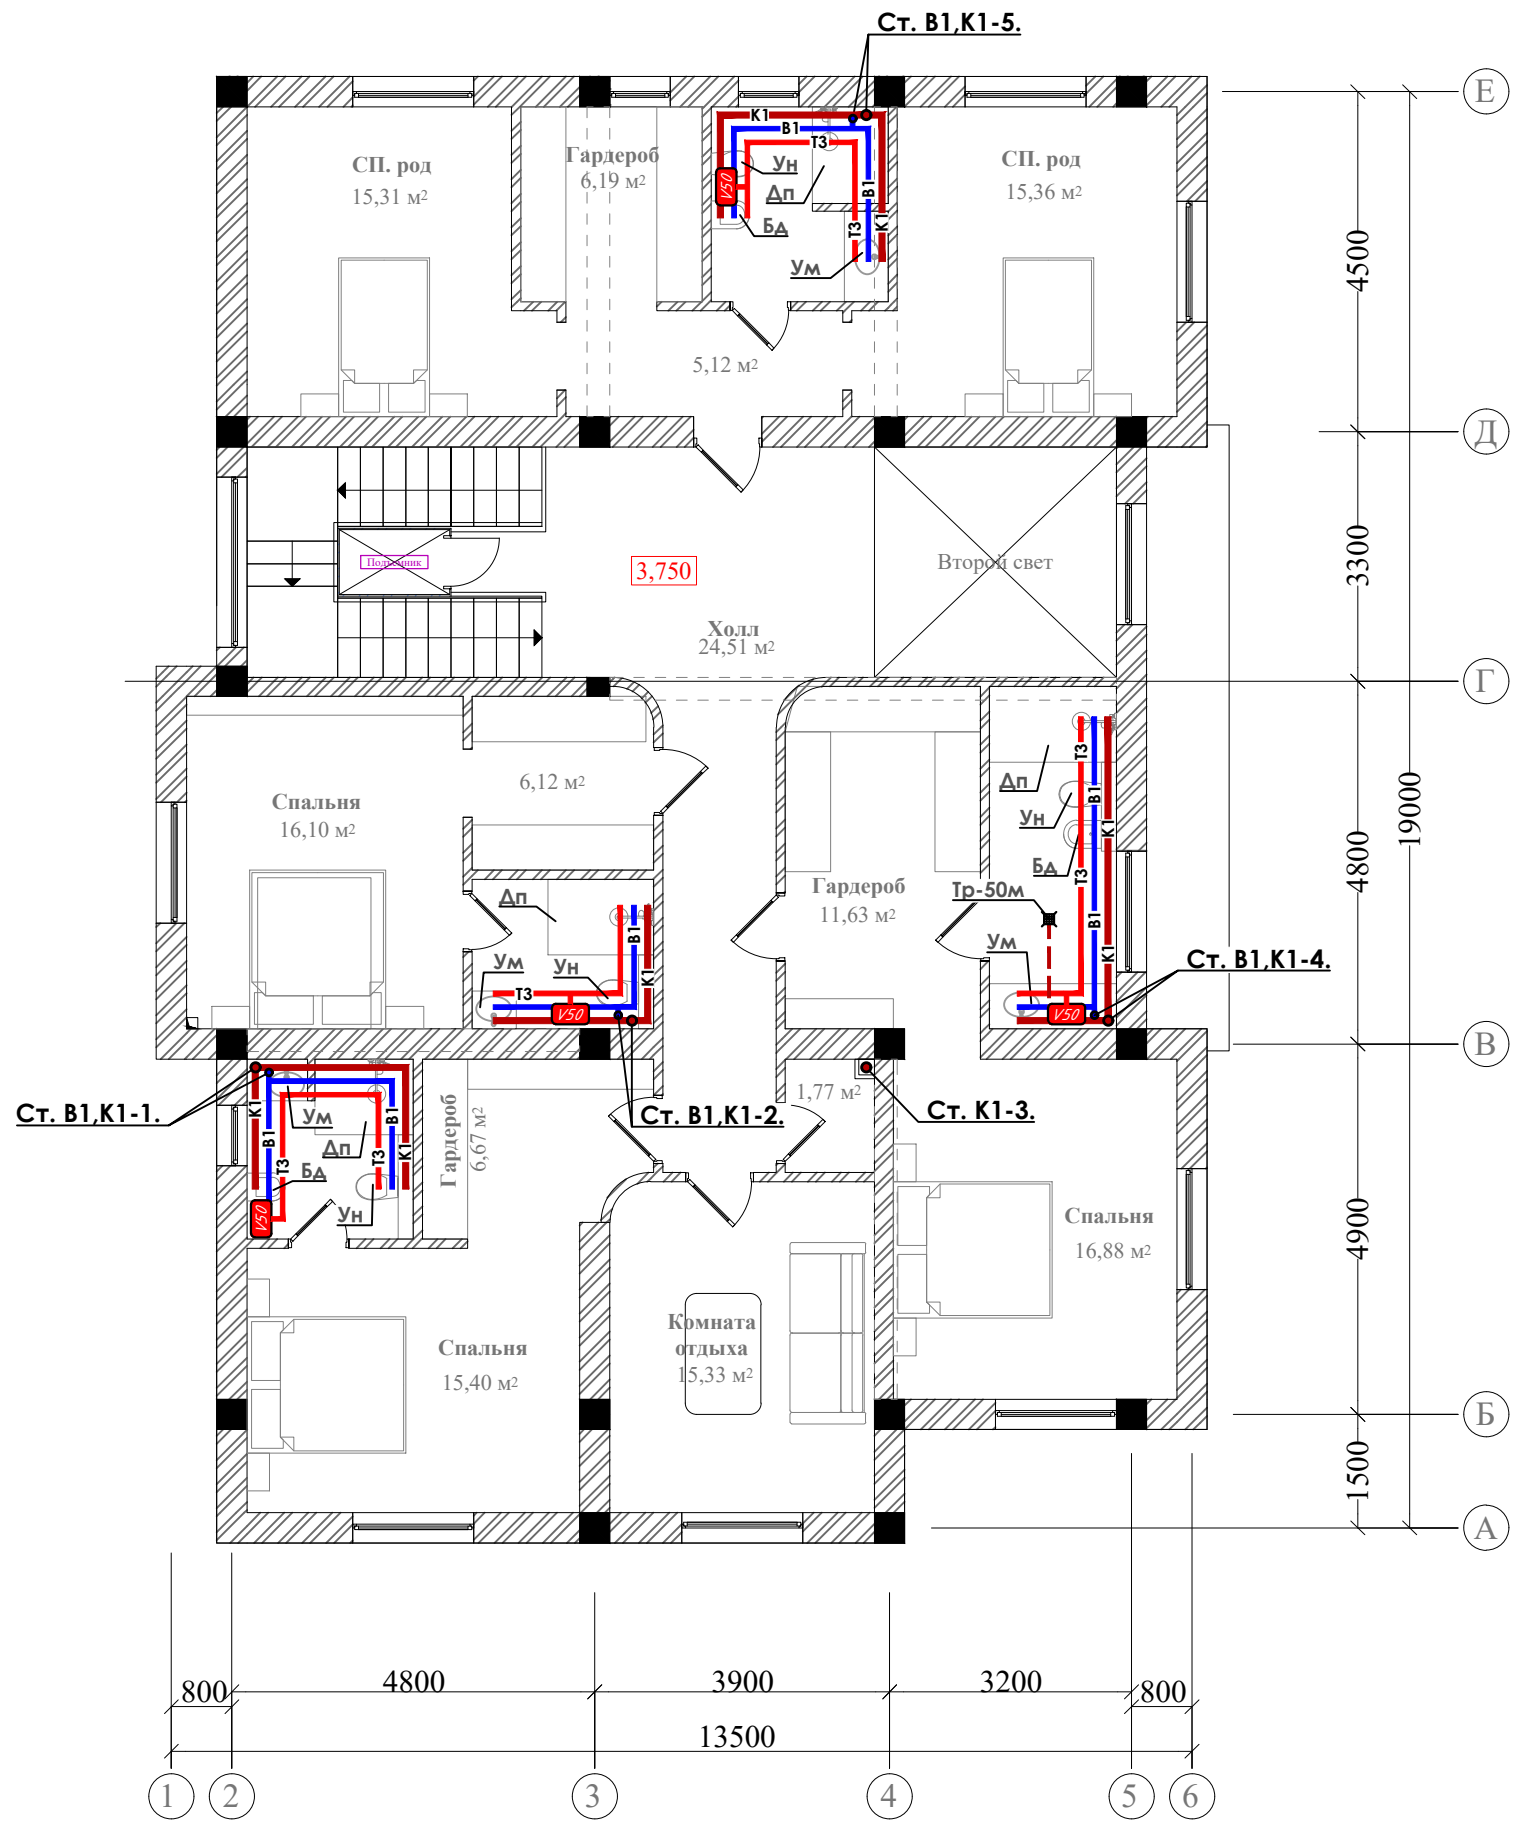


						ВК			
						"Соҳтмони биноҳои истикомати (Котедж)"			
Изм.	Кол.	Лист	№ док.	Подпись	Дата	Кисми обтаъминкуни ва корези.	Стадия	Лист	Листов
ГИП		00000			2026		РП	4	7
Разраб.		Халимов С			2026				

План кровли

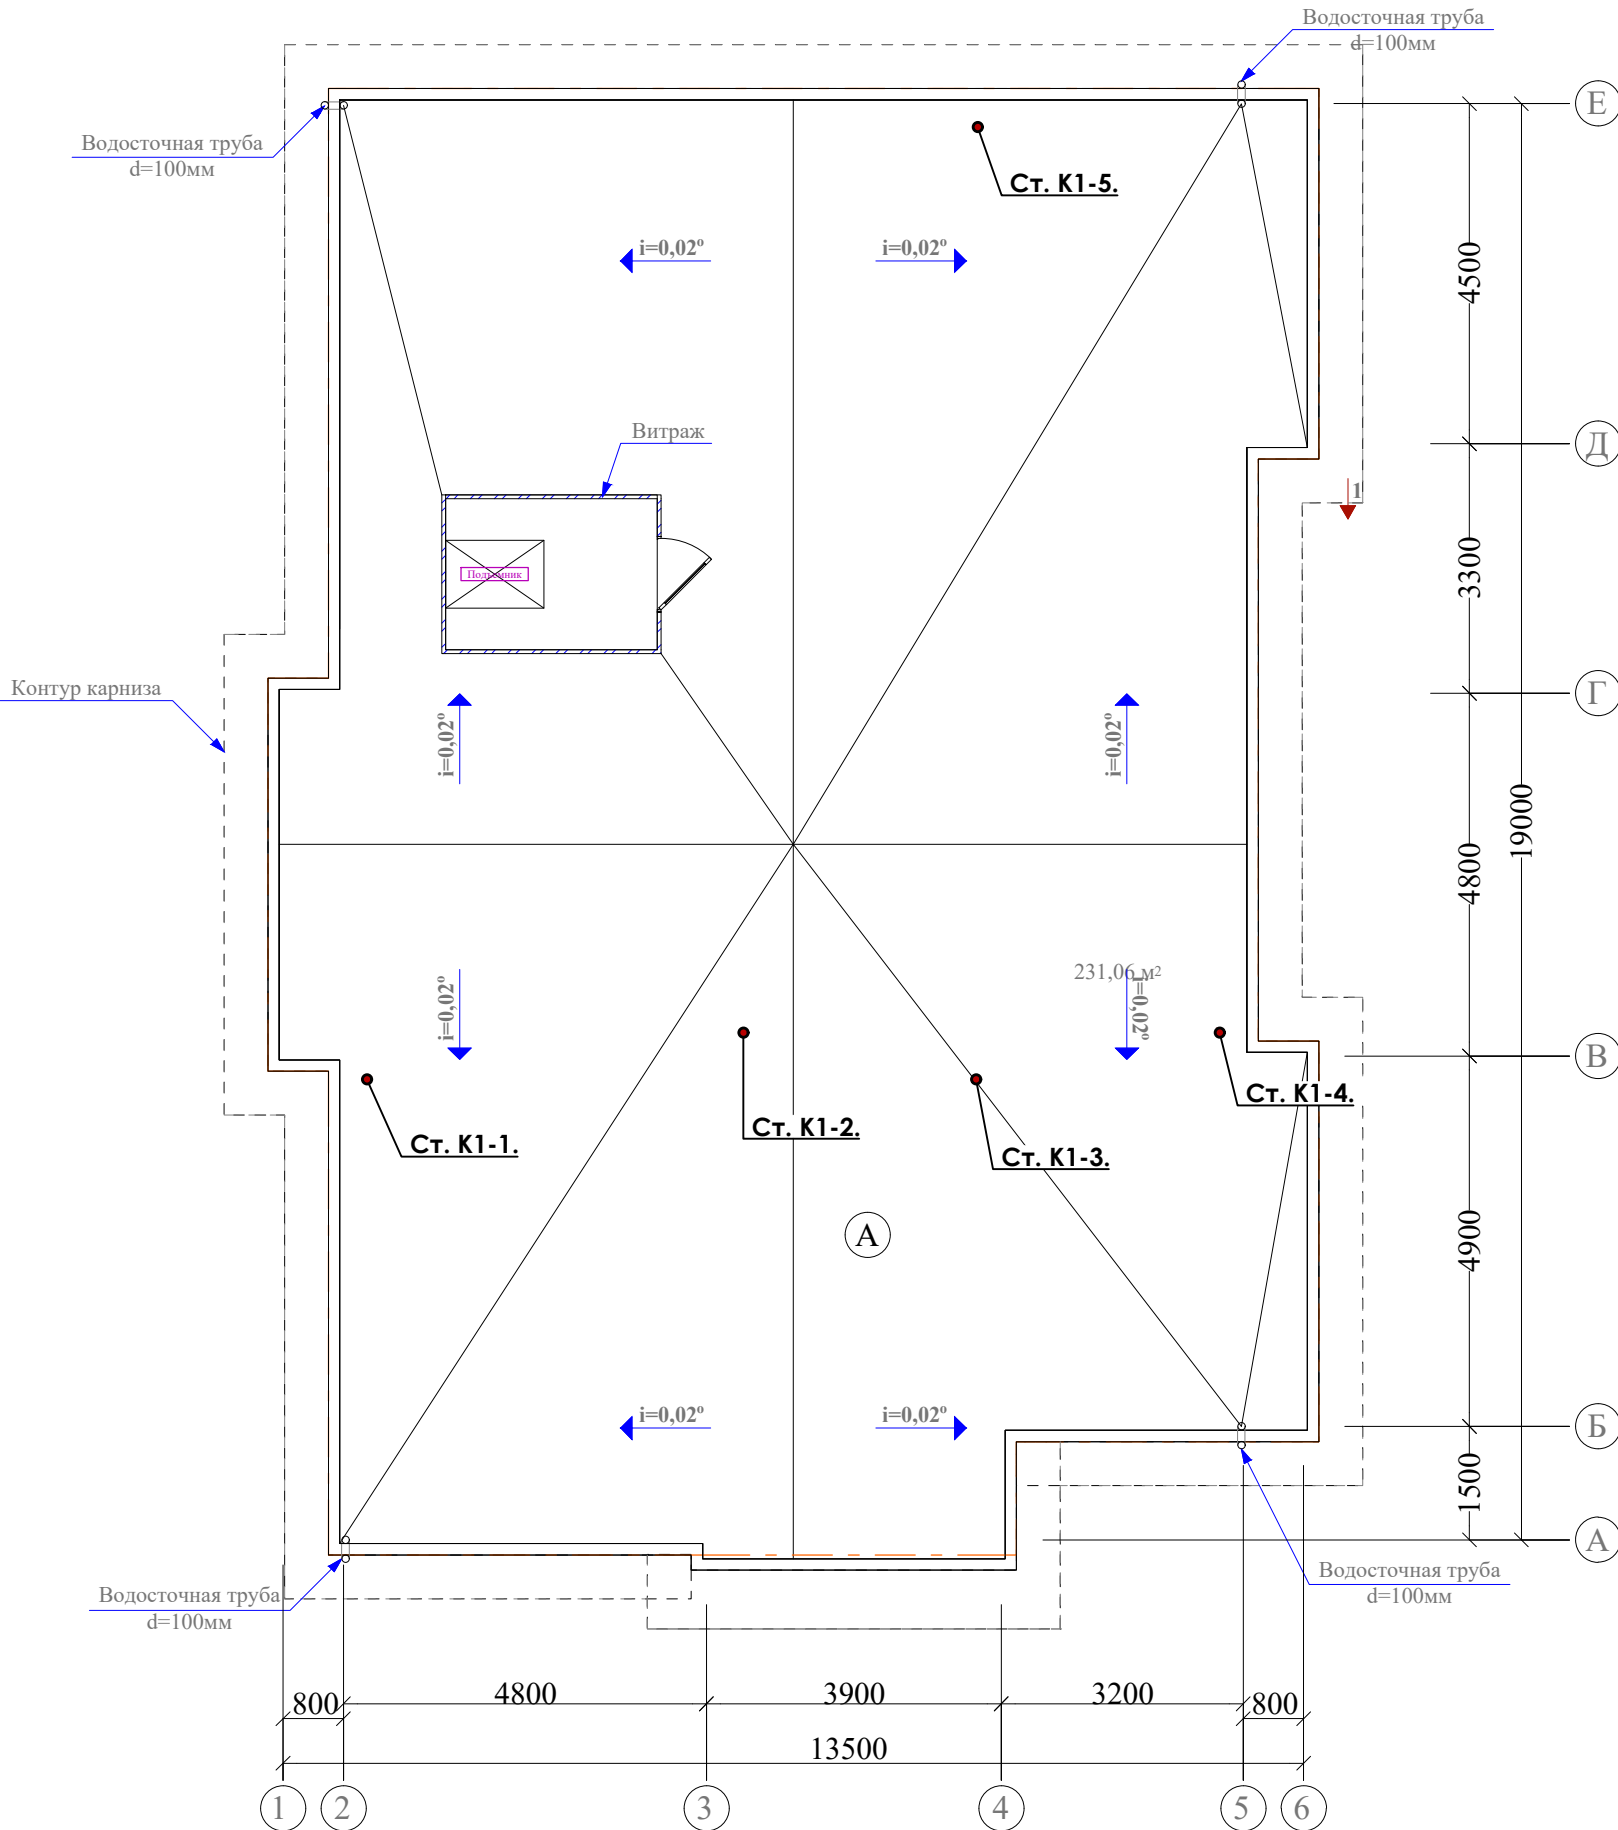


						ВК			
						"Соҳтмони биноҳои истикомати (Котедж)"			
Изм.	Кол.	Лист	№ док.	Подпись	Дата	Кисми обтаъминкуни ва корези.	Стадия	Лист	Листов
	ГИП	00000			2026		РП	5	7
	Разраб.	Халимов С			2026				

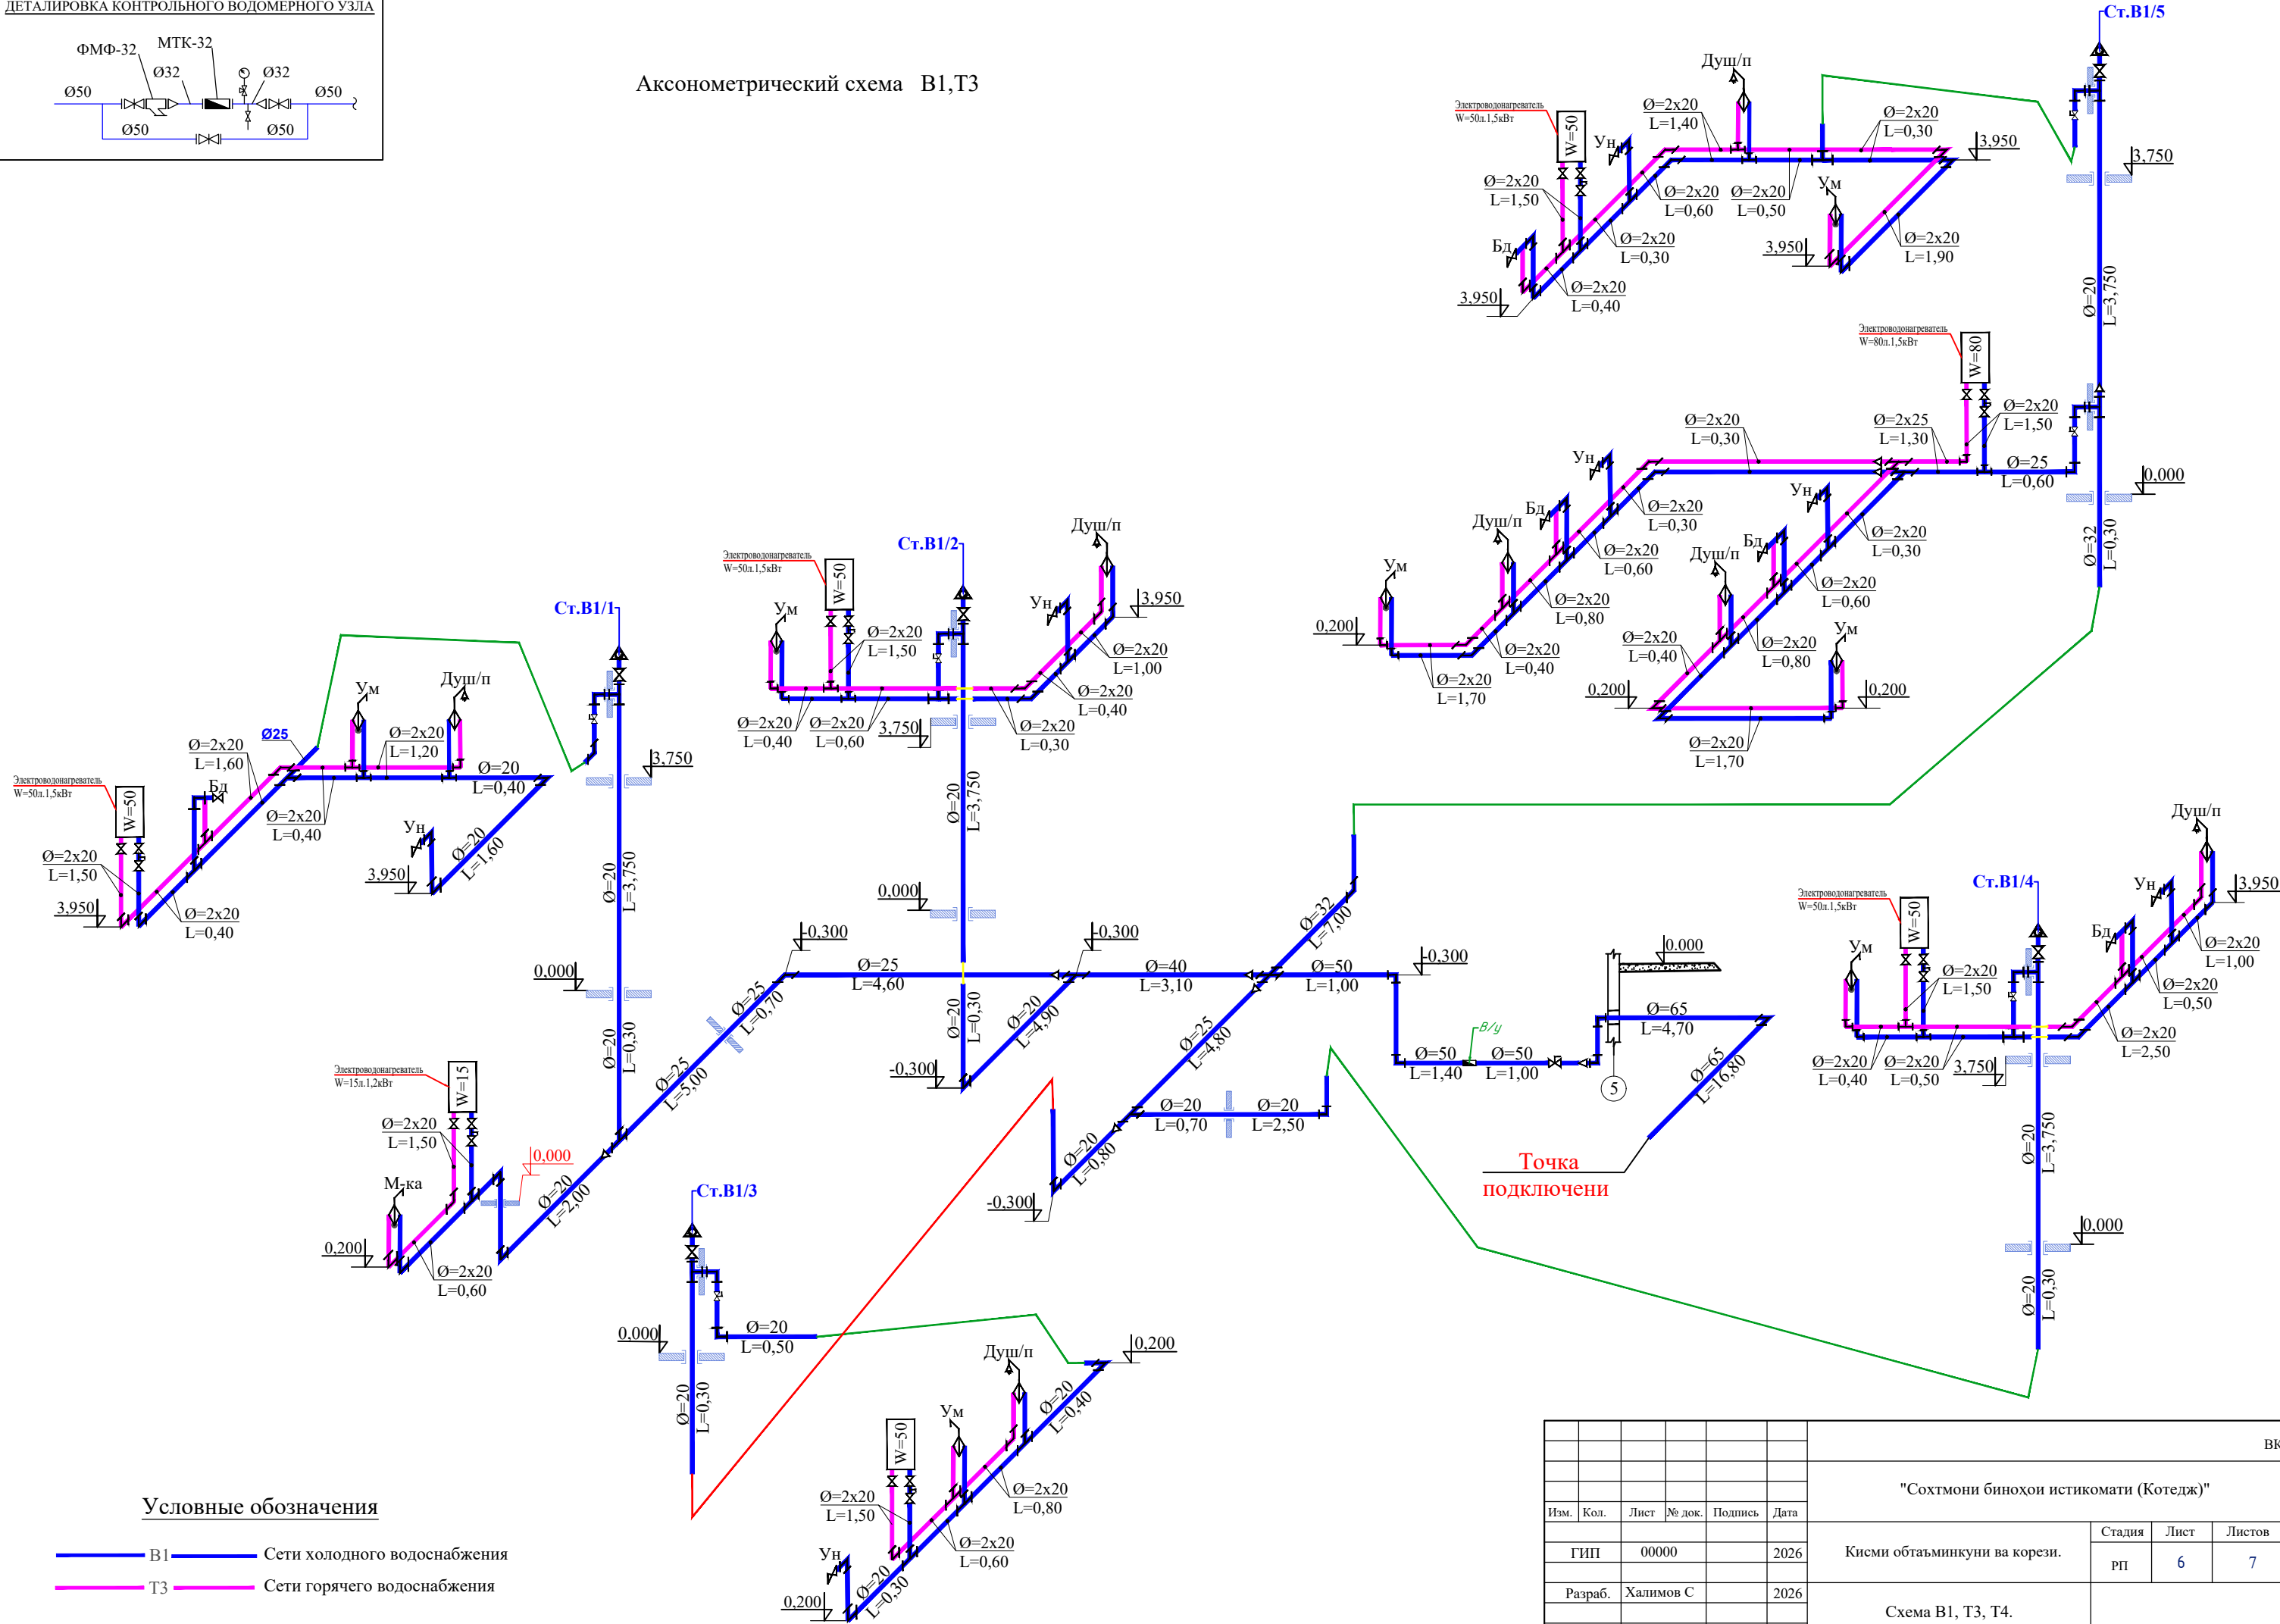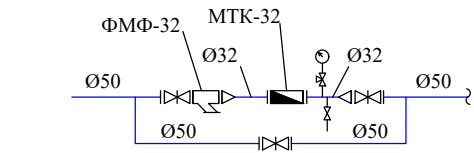

Условные обозначения

- В1 — Сети холодного водоснабжения
— Т3 — Сети горячего водоснабжения

						ВК			
						"Соҳтмони биноҳои истикомати (Котедж)"			
Изм.	Кол.	Лист	№ док.	Подпись	Дата	Кисми обтаъминкуни ва корези.	Стадия	Лист	Листов
	ГИП	00000			2026		РП	6	7
	Разраб.	Халимов С			2026				
						Схема В1, Т3, Т4.			

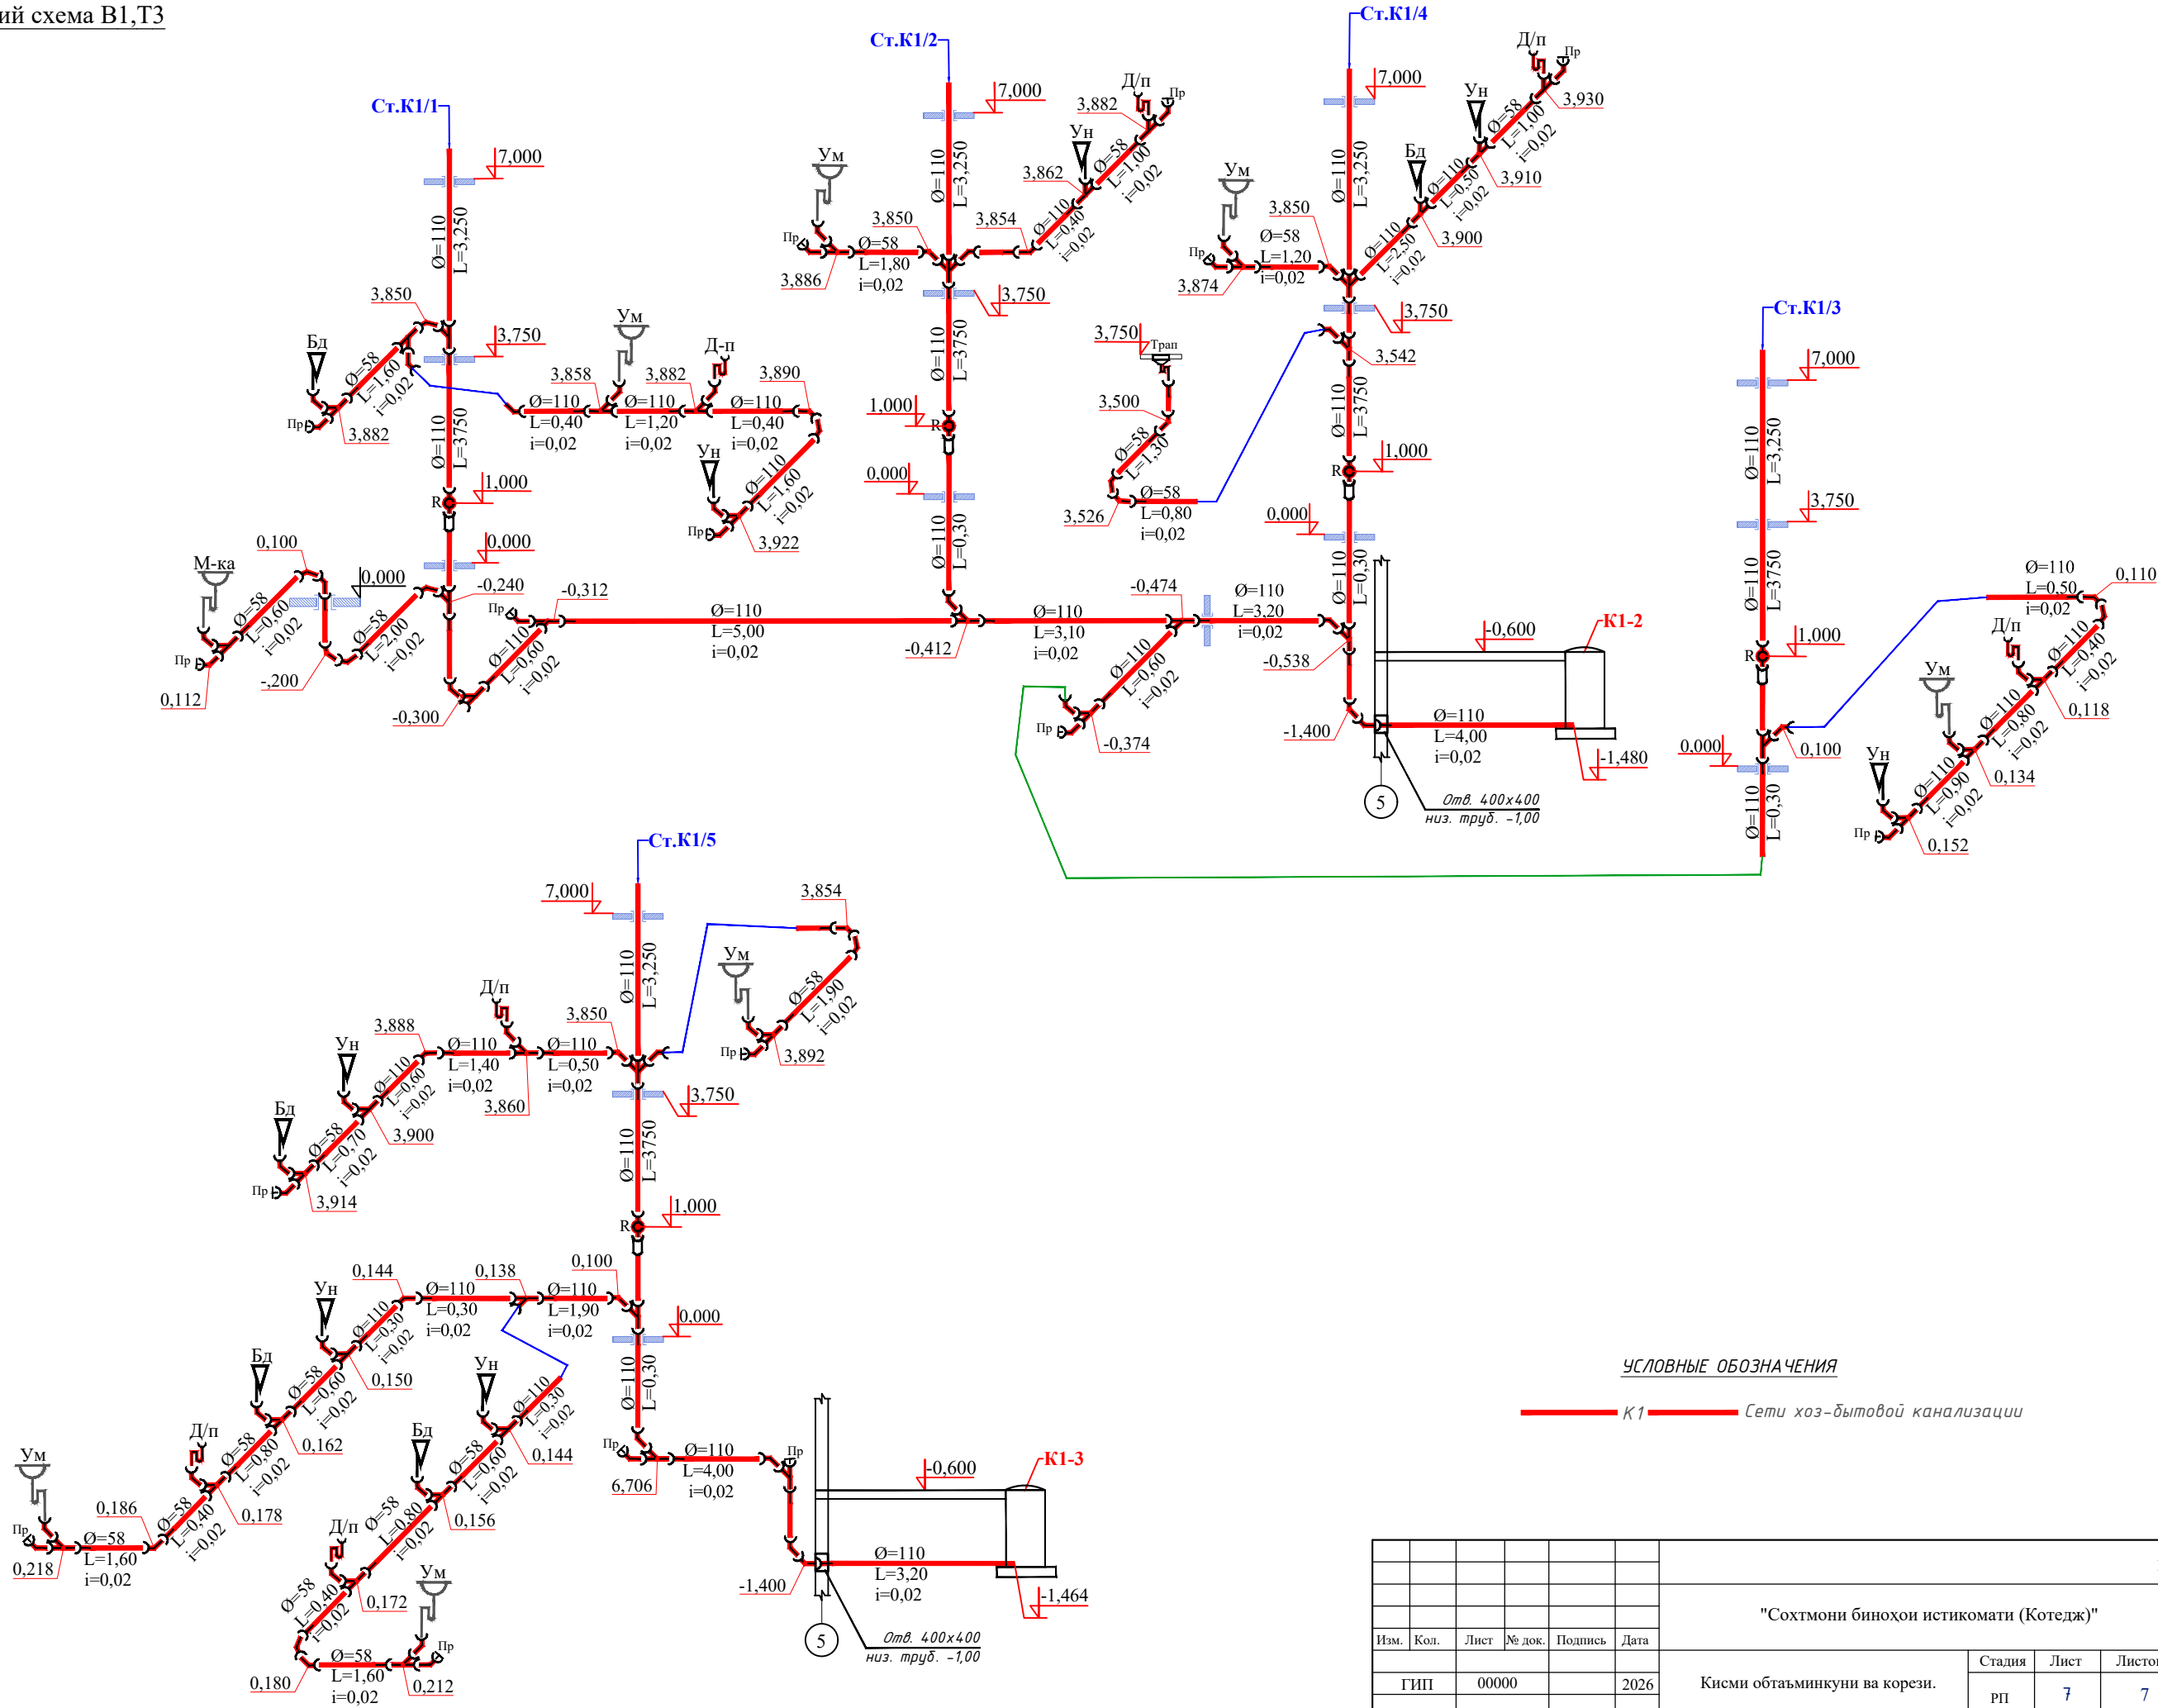

Изм. №	Изм. №
Подп. и дата	Подп. и дата
Изм. №	Изм. №

						ВК			
						"Соҳтмони биноҳои истикомати (Котедж)"			
Изм.	Кол.	Лист	№ док.	Подпись	Дата	Кисми обтаъминкуни ва корези.	Стадия	Лист	Листов
ГИП		00000		2026			РП	7	7
Разраб.		Халимов С		2026					
Схема К1.									

[illegible]

СОГЛАСОВАНО	Позиция	Наименование и техническая характеристика оборудования и материалов Завод изготовитель (для импортного оборудования - страна, фирма)	Тип, марка оборудования. Обозначение документа и номер опросного листа	Единица измерения1		Код завод изготовителя	Код оборудования материалов	Цена единицы оборудования тыс.сом.	Количество	Масса единицы оборудования кг.	
				Наименование	Код						
	1	1	3	4	5	6	7	8	9	10	
	Оборудования и материалы К1										
	1	Труба канализационная с муфтой Ø=110х5,3мм SILENTA	-	мм	-	—	M9000110200	-	95,80	-	
	2	Труба канализационная с муфтой Ø=58х4,0мм SILENTA	-	мм	-	-	M9000058100	-	29,60	-	
	3	Колено SILENTA 45° Ø=110х5,3мм	-	шт	-	-	T9001110045	-	48	-	
	4	Колено SILENTA 45° Ø=58х4,0мм	-	шт	-	-	T9001110045	-	52	-	
	5	Тройник раструбные SILENTA 45° 110х110х110мм		шт	-	-	T9452110110	-	22	-	
	6	Тройник раструбные SILENTA 45° 110х58х110мм		шт	-	-	T9452110110	-	8	-	
	7	Тройник раструбные SILENTA 45° 58х58х58мм		шт	-	-	T9452050058	-	15	-	
	8	Крестовина раструбные SILENTA 45° 110х110х110мм		шт	-	-	-	-	3	-	
	9	Редуктор SILENTA 110х58мм		шт	-	-	T9003110050	-	10	-	
	10	Ревизия с крышкой ПВХ 110мм		шт	-	-	T9006000110	-	5	-	
	11	Патрубок компенсационный 110мм		шт	-	-	T9008000110	-	5	-	
12	Прочистка Ø110мм		шт	-	-	-	-	10	-		
13	Прочистка Ø58мм		шт	-	-	-	-	12	-		
14	Хомут с гайками SILENTA 110мм	-	шт	-	-	T90080000110	-	92	-		
15	Хомут с гайками SILENTA 58мм	-	шт	-	-	T900800058	-	26	-		
Инв.№ подл.	Подпись и дата.	Взам. инв.№									
				Изм.Кал.чЛист № док.Погн. gamma				Спецификация оборудования и материалов К1.		Лист	
										3	